

COURSE: TECHNICAL OFFICE G46

Name: Ibrahim Mohamed Read

Eng: Amr Mamdouh

Task: 1

Notes:

1. THE COPYRIGHT OF THIS DRAWING IS VESTED IN YOURSPREADSHEETS AND IT MAY NOT BE REPRODUCED IN WHOLE OR PART OR USED FOR THE MANUFACTURE OF ANY ARTICLE WITHOUT THE EXPRESS PERMISSION OF THE COPYRIGHT HOLDERS.
2. WORK TO DIMENSIONS ONLY.

Key plane

Before

Instructor :

YourSpreadsheets

Address line 1
Address line 2
Telephone line 1
Fax line 1
www.YourSpreadsheets.co.uk

CLIENT: BAH i CLIENT
3 Mossadak, Ad Doqi, Dokki,
Giza Governorate, Giza,
Egypt

ARCHITECT: Amr Mamdoh
40 Mossadak, Ad Doqi, Dokki,
Giza Governorate, Giza,
Egypt

SITE: 31 ROVER ROAD
BLOCK A AND B

TITLE: RC DETAILS AND SECTIONS
OF GROUND BEAMS

SCALE AT A2: 1:50, 1:100	DATE: 05/09/13	DRAWN: DJ	CHECKED: DJ
PROJECT NO: 24567	DRAWING NO: A2/248	REVISION: C	

عمل مقايستة تشمينية لأعمال الحفر والردم والاحلال؟؟؟

م	بيان الأعمال	الوحدة	الكمية	الفئة	اجمالي
١	البند: بند أعمال الحفر والردم والاحلال				
١ - ١	بالمتر المكعب إزالة المخلفات من الموقع والتسوية قبل البدء في التنفيذ والبند شامل النقل للمقالب العمومية والفئة تشمل كل ما يلزم لنهو العمل طبقاً للمواصفات الفنية والرسومات وأصول الصناعة وطبقاً لتعليمات المهندس المشرف مما جميعه بالمتر المكعب	م ^٣	٤٠٠		
١ - ٢	بالمتر المكعب حفر لزوم الأساسات في جميع أنواع التربة هذا الصخر طبقاً لتقرير التربة وبالأبعاد المبينة على الرسومات والقياس الهندسي كما يشمل الحفر بين رموس الخوازيق وعلى المقاول معاينة وفحص التربة قبل وضع أسعاره والفئة تشمل سند جوانب الحفر طبقاً للمواصفات وطبقاً للكود المصري وبحسب طبيعة الموقع والمباني المجاورة وكذا الشوارع التي يطل عليها موقع المشروع والفئة تشمل عمل ميزانية شبكية بالموقع ونقل أي أتربة زائدة للمقالب العمومية وطبقاً لتعليمات المهندس المشرف والمواصفات الفنية مما جميعه بالمتر المكعب	م ^٣	٥٠٠		
١ - ٣	بالمتر المكعب ردم برمل سابسي نظيف وذلك بالأبعاد المبينة على الرسومات والبند يشمل الرش بالمياه والدمك الميكانيكي على أن يتم الردم على طبقات لا يزيد سمك أي منها عن ٢٥ سم والفئة تشمل كذلك إجراء تجارب الدمك اللازمة طبقاً للمواصفات الفنية والرسومات وأصول الصناعة وطبقاً لتعليمات المهندس المشرف مما جميعه بالمتر المكعب	م ^٣	٦٠٠		
١ - ٤	بالمتر المكعب توريد وعمل طبقة إحلال من تربة مكونة من الرمل النظيف موردة من خارج الموقع على أن توضع على طبقات كل طبقة (٢٥ سم) مع الرش والدمك لزوم طبقة الإحلال وعمل كافة الاختبارات اللازمة للوصول لمعدل دمك لا يقل عن (٩٥ %) باستخدام بروكتور المعدل والفئة تشمل كل ما يلزم لنهو الأعمال طبقاً للمواصفات الفنية وتعليمات المهندس المشرف مما جميعه بالمتر المكعب	م ^٣	٦٠٠		
	إجمالي قيمة بند أعمال الحفر والردم والاحلال				

Notes:

1. THE COPYRIGHT OF THIS DRAWING IS VESTED IN YOURSPREADSHEETS AND IT MAY NOT BE REPRODUCED IN WHOLE OR PART OR USED FOR THE MANUFACTURE OF ANY ARTICLE WITHOUT THE EXPRESS PERMISSION OF THE COPYRIGHT HOLDERS.
2. WORK TO DIMENSIONS ONLY.

Key plane

Before

Instructor :

YourSpreadsheets

Address line 1
Address line 2
Telephone line 1
Fax line 1
www.YourSpreadsheets.co.uk

CLIENT: BAHİ CLIENT
3 Mossadak, Ad Doqi, Dokki,
Giza Governorate, Giza,
Egypt

ARCHITECT: Amr Mamdoh
40 Mossadak, Ad Doqi, Dokki,
Giza Governorate, Giza,
Egypt

SITE: 31 ROVER ROAD
BLOCK A AND B

TITLE: RC DETAILS AND SECTIONS
OF GROUND BEAMS

SCALE AT A2: 1:50, 1:100	DATE: 05/09/13	DRAWN: DJ	CHECKED: DJ
PROJECT NO: 24567	DRAWING NO: A2/248	REVISION: C	

عمل مقايستة تجميعية لجميع بنود أعمال الخرسانة (الخرسانة العادية) ؟؟؟

م	بيان الأعمال	الوحدة	الكمية	الفئة	اجمالي
١	البند: بند أعمال الخرسانة العادية				
١ - ١	بالمتر المكعب توريد وصب خرسانة عادية لزوم عمل لبشة لأساسات المبنى طبقا للرسومات مكونة من ٣م ٠,٨٠ زلط + ٣م ٠,٤ رمل + ٢٥٠ كجم أسمنت بورتلاندي عادي طبقا للمناسيب والأبعاد الموضحة بالرسومات التنفيذية والفئة تشمل كل ما يلزم لنهوا العمل طبقا للمواصفات الفنية والرسومات و أصول الصناعة مما جميعه بالمتر المكعب	٣م	١٤٠		
٢ - ١	بالمتر المكعب توريد وصب خرسانة عادية لزوم دكة أسفل التبليطات للبدروم والمنحدرات واسفل تبليطات الارصفة والبردورات وخلافة سمك (١٥ سم) مكونة من ٣م ٠,٨٠ زلط + ٣م ٠,٤ رمل + ٢٠٠ كجم أسمنت بورتلاندي عادي والفئة تشمل كل ما يلزم لنهوا العمل طبقا للمواصفات الفنية والرسومات و أصول الصناعة مما جميعه بالمتر المكعب	٣م	٧٠		
٣ - ١	بالمتر المسطح توريد وعمل أرضيات من ترابيع خرسانة عادية مصبوبة على بيتها بسمك (١٠ سم) تصب أعلا الدكة الخرسانية (المحسوبة على حده) وتتكون من (٠,٨) متر مكعب زلط رقيق (فينو)، ٠,٤ متر مكعب رمل (٣٠٠ كجم) أسمنت بورتلاندي عادي تقسم إلى مسطحات حوالي (٢,٠٠ x ٢,٠٠) متر مسطح مع ترك فواصل بين الترابيع بعرض حوالي (١ سم) وبكامل العمق والفئة تشمل تسوية وجه البلاطات بالمناسيب المطلوبة وخدمة سطحها جيدا وتغطيتها بطبقة من الرمل المشبع بالماء وكذا ملء الفواصل بين الترابيع بعجينة الإسفلت والمقاس لمسطح البلاطات بما في ذلك الفواصل طبقاً للمواصفات الفنية والرسومات وأصول الصناعة وطبقاً لتعليمات المهندس المشرف مما جميعه بالمتر المسطح	٢م	٤٠٠		
٤ - ١	بالمتر المسطح توريد وصب دكة من الخرسانة العادية مكونة من ٣م ٠,٨ كسر حجر خفيف (س) + ٣م ٠,٤ رمل + ٢٠٠ كجم أسمنت بورتلاندي عادي لزوم ميول الأسطح فوق الطبقة العازلة وبسمك متوسط ٧ سم ولا يقل عن ٣ سم لتخليق الميول نحو الميزراب والفئة تشمل عمل وزرة مائلة حول الدراوي من نفس الخرسانة لتثبيت بلاط الوزرة عليها والمقاس هندسي حسب المسقط الأفقي دون علاوة نظير الميول والوزرة لنهوا العمل طبقا للمواصفات الفنية والرسومات و أصول الصناعة مما جميعه بالمتر المسطح	٢م	٣٣٠		
	إجمالي قيمة بند أعمال الخرسانة العادية				

عمل مقايستة تميمينيتة لجميع بنود أعمال الخرسانات (الخرسانة المسلحة) ؟؟؟

م	بيان الأعمال	الوحدة	الكمية	الفئة	اجمالي
١	البند: بند أعمال الخرسانة المسلحة				
١ - ١	بالمتر المكعب توريد وتنفيذ خرسانة مسلحة لزوم الأساسات (لبشة مسلحة) لزوم المبنى والسور (قواعد وميدات) طبقا للأبعاد والقطاعات والتسليح الموضحة بالرسومات والخرسانة مكونة من ٠,٨٠ م ٣ زلط متدرج + ٣ م ٠,٤ رمل نظيف + ٣٥٠ كجم أسمنت بورتلاندي عادي والخلط ميكانيكي باستخدام خلاط وهزاز ميكانيكي وان تراعى أصول الصناعة للوصول بالخلطات للإجهاد المطلوب والفئة تشمل دهان الاسطح الخرسانية بثلاث أوجه بمستحلب بيتوميني مطاطي عازل للرطوبة على البارد من عينة تعتمد قبل التوريد وكل ما يلزم لنهوا العمل طبقا للمواصفات الفنية والرسومات و أصول الصناعة مما جميعه بالمتر المكعب	٣م	٢٠٠		
١ - ٢	بالمتر المكعب توريد وصب خرسانة مسلحة لزوم الأعمدة والكمرات وبلاطات السقف والدرابي والأعتاب والسلالم وأعمدة السور والطبانات وخلافه مكونة من ٠,٨ م ٣ زلط + ٣ م ٠,٤ رمل + ٣٥٠ كجم أسمنت بورتلاندي عادي والخليط ميكانيكي باستخدام خلاط وهزاز ميكانيكي وان تراعى أصول الصناعة للوصول بالخلطات للإجهاد المطلوب والفئة تشمل كل ما يلزم لنهوا العمل طبقا للمواصفات الفنية والرسومات و أصول الصناعة مما جميعه بالمتر المكعب	٣م	٤٧٠		
	إجمالي قيمة بند أعمال الخرسانة المسلحة				



Notes:

1. THE COPYRIGHT OF THIS DRAWING IS VESTED IN YOURSPREADSHEETS AND IT MAY NOT BE REPRODUCED IN WHOLE OR PART OR USED FOR THE MANUFACTURE OF ANY ARTICLE WITHOUT THE EXPRESS PERMISSION OF THE COPYRIGHT HOLDERS.
2. WORK TO DIMENSIONS ONLY.

Key plane

Before

Instructor :

YourSpreadsheets

Address line 1
Address line 2
Telephone line 1
Fax line 1
www.YourSpreadsheets.co.uk

CLIENT: BAH i CLIENT
3 Mossadak, Ad Doqi, Dokki,
Giza Governorate, Giza,
Egypt

ARCHITECT: Amr Mamdoh
40 Mossadak, Ad Doqi, Dokki,
Giza Governorate, Giza,
Egypt

SITE: 31 ROVER ROAD
BLOCK A AND B

TITLE: RC DETAILS AND SECTIONS
OF GROUND BEAMS

SCALE AT AS: 1:50, 1:100	DATE: 05/09/13	DRAWN: DJ	CHECKED: DJ
PROJECT NO: 24567	DRAWING NO: A2/248	REVISION: C	

عمل مقايستة تشمينية لبنود التشطيبات؟؟؟



Notes:

1. THE COPYRIGHT OF THIS DRAWING IS VESTED IN YOURSPREADSHEETS AND IT MAY NOT BE REPRODUCED IN WHOLE OR PART OR USED FOR THE MANUFACTURE OF ANY ARTICLE WITHOUT THE EXPRESS PERMISSION OF THE COPYRIGHT HOLDERS.
2. WORK TO DIMENSIONS ONLY.

Key plane

Before

Instructor :

YourSpreadsheets

Address line 1
Address line 2
Telephone line 1
Fax line 1
www.YourSpreadsheets.co.uk

CLIENT: BAH i CLIENT
3 Mossadak, Ad Doqi, Dokki,
Giza Governorate, Giza,
Egypt

ARCHITECT: Amr Mamdoh
40 Mossadak, Ad Doqi, Dokki,
Giza Governorate, Giza,
Egypt

SITE: 31 ROVER ROAD
BLOCK A AND B
TITLE: RC DETAILS AND SECTIONS
OF GROUND BEAMS

SCALE AT AS: 1:50, 1:100	DATE: 05/09/13	DRAWN: DJ	CHECKED: DJ
PROJECT NO: 24567	DRAWING NO: A2/248	REVISION: C	

م	بيان الأعمال	الوحدة	الكمية	الفئة	اجمالي
١	البند: بند أعمال المباني				
١ - ١	بالمتر المكعب توريد وعمل مباني بالطوب الطفلي المثقب الذي لا يزيد وزن المتر المكعب منه عن ١٢٠٠ كجم بسمك ٢٥ x ١٢ x ٦ سم بمونة ٣٠٠ كجم أسمنت بورتلاندي / ٣م رمل والفئة تشمل كل ما يلزم لنهوا العمل طبقاً للمواصفات الفنية والرسومات وأصول الصناعة مما جميعه بالمتر المكعب	٣م	١٥٠		
	إجمالي قيمة بند أعمال المباني				
٢	البند: بند أعمال البياض				
١ - ٢	بالمتر المسطح - توريد وعمل بياض تخشين للحوائط والأسقف الداخلية مكونة من طبقة طرطشة بمونة ٤٥٠ كجم أسمنت / ٣م رمل وبسمك ٠,٥ سم ثم عمل طبقة بياض بمونة مكونة من ٣٠٠ كجم أسمنت بورتلاندي عادي / ٣م رمل ومحمل على البند توريد وتركيب شبكة من الفايبر عند اتصال العناصر الخرسانية مع الحوائط مع تأميم الفتحات وبلسقات الشبابيك ، ويشمل البند أيضاً استلام بؤج وأوتار السقف باستخدام ميزان القامة مع نهو وتشطيب الأعمال طبقاً لأصول الصناعة وحسب المواصفات والكود المصري وتعليمات المهندس المشرف كاملاً مما جميعه بالمتر المسطح	٢م	٢٠٠		
	إجمالي قيمة بند أعمال البياض				
٣	البند: بند أعمال الدهانات				
١ - ٣	بالمتر المسطح - توريد وعمل دهان بلاستيك للأسقف والحوائط الداخلية من بلاستيك أكريليك داخلي (أنتاج شركة ACC أو ما يماثله) باللون المطلوب وهو عباره عن وجه تحضير من السير المائي الشفاف وعدد ٢ وجه معجون من نفس شركة الدهانات المعتمدة ملونتان بألوان مختلفة إحداهما أفقي والسكينة الأخرى رأسية مع الصنفرة وعدد ٣ أوجه ببوية البلاستيك الجاهزة عدد واحد وجه بطانه بلاستيك برتقالي (أبيض) + عدد ٢ وجه بلاستيك اكسترا (ألوان) باللون المطلوب وعلى المقاول اعتماد عينة البوية شاملة المعجون طبقاً للمواصفات والبند يشمل كل ما يلزم لنهوا الأعمال طبقاً للمواصفات والكود المصري وأصول الصناعة وتعليمات المهندس المشرف كاملاً مما جميعه بالمتر المسطح	٢م	٢٠٠		
	إجمالي قيمة بند أعمال الدهانات				

عمل مقايست تشمينيت لبنود التشطيبات؟؟؟



Notes:

1. THE COPYRIGHT OF THIS DRAWING IS VESTED IN YOURSPREADSHEETS AND IT MAY NOT BE REPRODUCED IN WHOLE OR PART OR USED FOR THE MANUFACTURE OF ANY ARTICLE WITHOUT THE EXPRESS PERMISSION OF THE COPYRIGHT HOLDERS.
2. WORK TO DIMENSIONS ONLY.

Key plane

Before

Instructor :

YourSpreadsheets

Address line 1
Address line 2
Telephone line 1
Fax line 1
www.YourSpreadsheets.co.uk

CLIENT: BAH E CLIENT
3 Mossadak, Ad Doqi, Dokki,
Giza Governorate, Giza,
Egypt

ARCHITECT: Amr Mamdoh
40 Mossadak, Ad Doqi, Dokki,
Giza Governorate, Giza,
Egypt

SITE: 31 ROVER ROAD
BLOCK A AND B
TITLE: RC DETAILS AND SECTIONS
OF GROUND BEAMS

SCALE AT A2: 1:50, 1:100	DATE: 05/09/13	DRAWN: DJ	CHECKED: DJ
PROJECT NO: 24567	DRAWING NO: A2/248	REVISION: C	

م	بيان الأعمال	الوحدة	الكمية	الفئة	اجمالي
٤	البند: بند أعمال العزل				
١ - ٤	بالمتر المسطح توريد وعمل طبقة عزل رطوبة للحمامات بلفائف البيتومين المعدل والمسلح بالبولي إستر سمك ٤ مم الملحومة باللهب من إنتاج شركة بيتونيل p5 او ما يعادلها وتشمل عمل وجه تحضري من البرايمر الخاص بالشركة المنتجة ويشمل البند عمل ركوب ١٠ سم مع امتداد العزل رأسياً حتى منسوب أعلى البلاط بمقدار ١٥ سم وكذلك عمل طبقة لياسة أسمنتية سمك ٣ سم لحماية العزل بمونة مكونة من ٢٥٠ كجم أسمنت / م ٣ رمل ومحمل على البند عمل رقبة زجاجة أسمنتية من نفس مكونات مونة اللياسة مع عمل اختبار ملء المياه بسمك حوالى ١٠ سم لمدة ٤٨ ساعة للتأكد من عدم التسريب ونهو وتشطيب الأعمال طبقاً للمواصفات والكود المصرى وأصول الصناعة وتعليمات المهندس المشرف كاملاً مما جميعه بالمتر المسطح	م ٢	٤٠٠		
	إجمالي قيمة بند أعمال العزل				
٥	البند: بند أعمال الأبواب				
١ - ٥	بالعدد توريد وتركيب أبواب خشب زان بجميع مشتملاتها على ان يتكون من ١- الحلق من الخشب الزان بقطاع ٢ x ٦ ٢- الراس العليا من الخشب الزان بقطاع ٢ x ٤ ٣- الراس السفلى من الخشب الزان بقطاع ٢ x ٦ ٤- القوائم من الخشب الزان بقطاع ٢ x ٤ ٥- العوارض من الخشب الزان بقطاع ٢ x ٢٢/١ ٦- الحشوات من الخشب الزان بقطاع ٣/٤ ٧- تجليد ابلكاش زان سمك ٥ سم وقشرة قرو ٨- الباككات من الخشب زان بقطاع ٣/٤ x ٣/٤ ٩- البرور من الخشب الزان بقطاع ٣/٤ x ٢٢/١ والفئة تشمل توريد وتركيب حلق ثانوي من الخشب الموسيقى - بقطاع ١ x ٦ وكل ما يلزم لنهو الاعمال طبقاً للمواصفات الفنية وأصول الصناعة وتعليمات المهندس المشرف على التنفيذ مما جميعه بالعدد	بالعدد	١٣		
	إجمالي قيمة بند أعمال الأبواب				

عمل مقايست تشمينيت لبنود التشطيبات؟؟؟

م	بيان الأعمال	الوحدة	الكمية	الفئة	اجمالي
٦	البند: بند أعمال الالومنتال				
٦ - ١	بالعدد توريد وتركيب شبك الوميتال ٢ ضلفة فارغ زجاج منزلق مقاس (١,٥٠*١,٢٠) متر والفئة تشمل كل ما يلزم لنهو الأعمال طبقا للمواصفات الفنية وأصول الصناعة وتعليمات المهندس المشرف على التنفيذ مما جميعه بالعدد	بالعدد	١٣		
	إجمالي قيمة بند أعمال الالومنتال				



Notes:

1. THE COPYRIGHT OF THIS DRAWING IS VESTED IN YOURSPREADSHEETS AND IT MAY NOT BE REPRODUCED IN WHOLE OR PART OR USED FOR THE MANUFACTURE OF ANY ARTICLE WITHOUT THE EXPRESS PERMISSION OF THE COPYRIGHT HOLDERS.
2. WORK TO DIMENSIONS ONLY.

Key plane

Before

Instructor :

YourSpreadsheets

Address line 1
Address line 2
Telephone line 1
Fax line 1
www.YourSpreadsheets.co.uk

CLIENT: BAH i CLIENT
3 Mossadak, Ad Doqi, Dokki,
Giza Governorate, Giza,
Egypt

ARCHITECT: Amr Mamdoh
40 Mossadak, Ad Doqi, Dokki,
Giza Governorate, Giza,
Egypt

SITE: 31 ROVER ROAD
BLOCK A AND B

TITLE: RC DETAILS AND SECTIONS
OF GROUND BEAMS

SCALE AT A2: 1:50, 1:100	DATE: 05/09/13	DRAWN: DJ	CHECKED: DJ
PROJECT NO: 24567	DRAWING NO: A2/248	REVISION: C	

THE END

COURSE: TECHNICAL OFFICE G46

Name: Ibrahim Mohamed Read

Eng: Amr Mamdouh

Lecture: 4

Task: 2

Arvil Group
CONSTRUCTION & TRAINING COMPANY

1. THE COPYRIGHT OF THIS DRAWING IS VESTED IN TONSPOGROSHETS AND IT MAY NOT BE REPRODUCED IN WHOLE OR PART OR USED FOR THE MANUFACTURE OF ANY ARTICLE WITHOUT THE EXPRESS PERMISSION OF THE COPYRIGHT HOLDERS.

2. WORK TO FIGURED DIMENSIONS ONLY.

Before

Address line 1
Address line 2
Telephone line 1
Fax line 1
www.YourSpreadsheets.co.uk

SCALE AT A2: 1:50, 1:100	DATE: 05/09/13	DRAWN: DJ	CHECKED: DJ
PROJECT NO: 24567	DRAWING NO: A2/248	REVISION: C	

[illegible]

الحصر الهندسي لبند الحضر ؟؟؟



Notes:

1. THE COPYRIGHT OF THIS DRAWING IS VESTED IN YOURSPREADSHEETS AND IT MAY NOT BE REPRODUCED IN WHOLE OR PART OR USED FOR THE MANUFACTURE OF ANY ARTICLE WITHOUT THE EXPRESS PERMISSION OF THE COPYRIGHT HOLDERS.
2. WORK TO DIMENSIONS ONLY.

Key plane

Before

Instructor :

YourSpreadsheets

Address line 1
Address line 2
Telephone line 1
Fax line 1
www.YourSpreadsheets.co.uk

CLIENT: BAH i CLIENT
3 Mossadak, Ad Doqi, Dokki,
Giza Governorate, Giza,
Egypt

ARCHITECT: Amr Mamdoh
40 Mossadak, Ad Doqi, Dokki,
Giza Governorate, Giza,
Egypt

SITE: 31 ROVER ROAD
BLOCK A AND B

TITLE: RC DETAILS AND SECTIONS
OF GROUND BEAMS

SCALE AT A2: 1:50, 1:100	DATE: 05/09/13	DRAWN: DJ	CHECKED: DJ
PROJECT NO: 24567	DRAWING NO: A2/248	REVISION: C	

رقم البند	نوع الأعمال و التوريدات	وحدة القياس	عدد	مقاسات			مسطحات أو مكعبات		إجمالي بعد التنزيلات	ملاحظات
				الطول	العرض	ارتفاع	اجمالي	تنزيلات		
	البند: بالمتر المكعب حصر حفز لزوم السمات لمشروع car shed									
	بين محور Ax ومحور Bx	م ²	١	٢,٠٧٩	٠,٢٥٠	١,٦	٠,٨٣٢	٠,٠٠٠	٠,٨٣٢	
	محور Bx	م ²	١	٤,٣٢٥	٠,٢٥٠	١,٦	١,٧٣٠	٠,٠٠٠	١,٧٣٠	
	محور Cx	م ²	٢	٦,٣٥٠	٠,٢٥٠	١,٦	٥,٠٨٠	٠,٠٠٠	٥,٠٨٠	
	محور ١x	م ²	١	٣,٤٠٠	٠,٣٠٠	١,٦	١,٦٣٢	٠,٠٠٠	١,٦٣٢	
	محور ٢x	م ²	١	٣,٤٠٠	٠,٢٥٠	١,٦	١,٣٦٠	٠,٠٠٠	١,٣٦٠	
	محور ٣x	م ²	١	٣,٤٠٠	٠,٣٠٠	١,٦	١,٦٣٢	٠,٠٠٠	١,٦٣٢	
	محور ٤x	م ²	١	٦,١٠٠	٠,٣٠٠	١,٦	٢,٩٢٨	٠,٠٠٠	٢,٩٢٨	
	بين محور ٤x ومحور ٥x	م ²	١	٦,١٠٠	٠,٣٠٠	١,٦	٢,٩٢٨	٠,٠٠٠	٢,٩٢٨	
	محور ٥x	م ²	١	٦,١٠٠	٠,٣٠٠	١,٦	٢,٩٢٨	٠,٠٠٠	٢,٩٢٨	

الحصر الفعلي لبند الحفر؟؟؟



Notes:

1. THE COPYRIGHT OF THIS DRAWING IS VESTED IN YOURSPREADSHEETS AND IT MAY NOT BE REPRODUCED IN WHOLE OR PART OR USED FOR THE MANUFACTURE OF ANY ARTICLE WITHOUT THE EXPRESS PERMISSION OF THE COPYRIGHT HOLDERS.
2. WORK TO DIMENSIONS ONLY.

Key plane

Before

Instructor :

YourSpreadsheets

Address line 1
Address line 2
Telephone line 1
Fax line 1
www.YourSpreadsheets.co.uk

CLIENT: BAH i CLIENT
3 Mossadak, Ad Doqi, Dokki,
Giza Governorate, Giza,
Egypt

ARCHITECT: Amr Mamdoh
40 Mossadak, Ad Doqi, Dokki,
Giza Governorate, Giza,
Egypt

SITE: 31 ROVER ROAD
BLOCK A AND B

TITLE: RC DETAILS AND SECTIONS
OF GROUND BEAMS

SCALE AT A2: 1:50, 1:100	DATE: 05/09/13	DRAWN: DJ	CHECKED: DJ
PROJECT NO: 24567	DRAWING NO: A2/248	REVISION: C	

رقم البند	نوع الأعمال و التوريدات	وحدة القياس	عدد	مقاسات			مسطحات أو مكعبات		إجمالي بعد التنزيلات	ملاحظات
				الطول	العرض	ارتفاع	اجمالي	تنزيلات		
	البند: بالمتر المكعب حصر الكميه الفعليه لبند الحفر لمشروع car shed									
	رفرفه ١متر على كامل المساحة	م ^٢	٢	٢٤٣,٠٩٩	١,٦		٧٧٧,٩١٧	٠,٠٠٠	٧٧٧,٩١٧	
	إجمالي البند: بالمتر المكعب حصر الكميه الفعليه لبند الحفر لمشروع car shed فقط سبعمانه و سبعة و سبعون و (٩١٧/ ١٠٠٠) لاغير									

رقم البند	نوع الأعمال و التوريدات	وحدة القياس	عدد	مقاسات			مسطحات أو مكعبات		إجمالي بعد التنزيلات	ملاحظات				
				الطول	العرض	ارتفاع	اجمالي	تنزيلات						
	البند: بالمتر المكعب حصر الكميه الفعليه لبند الحفر لمشروع car shed													
	رفرفه ١متر على مساحة المبنى	م ^٢	٢	٢٠٤,٣٤٠		١,٦	٦٥٣,٨٨٨	٠,٠٠٠	٦٥٣,٨٨٨					
											٦٥٣,٨٨٨	٠,٠٠٠	٦٥٣,٨٨٨	
	إجمالي البند: بالمتر المكعب حصر الكميه الفعليه لبند الحفر لمشروع car shed فقط ستمائة و ثلاثة و خمسون و (٨٨٨/ ١٠٠٠) لاغير													

٠,١٧	معامل الانتفاش
٦٥٤,٠٥٨	الكميه الفعليه بعد زيادة معامل الاتكماش
١٣٠٧,٩٤٦	الكميه الفعليه بعد إضافة الرفرفه ومعامل الانتفاش
٣,٠٠٠	عدد القلايات المستخدمه
١٠,٠٠٠	تكعيب القلايات
٤٣,٥٩٨	عدد النقلات بالقلاب

Arvil Group
CONSTRUCTION & TRAINING COMPANY

1. THE COPYRIGHT OF THIS DRAWING IS VESTED IN TOWERSPENCER AND IT MAY NOT BE REPRODUCED IN WHOLE OR PART OR USED FOR THE MANUFACTURE OF ANY ARTICLE WITHOUT THE EXPRESS PERMISSION OF THE COPYRIGHT HOLDERS.

2. WORK TO FIGURED DIMENSIONS ONLY.

Before

Address line 1
Address line 2
Telephone line 1
Fax line 1
www.YourSpreadsheets.co.uk

ARCHITECT: Amr Mamdoh
40 Mossadak, Ad Doqi, Dokki,
Giza Governorate, Giza,
Egypt

SCALE AT A2: 1:50, 1:100	DATE: 05/09/13	DRAWN: DJ	CHECKED: DJ
PROJECT NO: 24567	DRAWING NO: A2/248	REVISION: C	

رقم البند	نوع الأعمال و التوريدات	وحدة القياس	عدد	مقاسات			مسطحات أو مكعبات		إجمالي بعد التنزيلات	ملاحظات
				الطول	العرض	ارتفاع	اجمالي	تنزيلات		
	البند: بالمتر المكعب حصر الاحلال لمشروع car shed									
	رفرفه إحلال ٠,٥	م ^٣		١٧٠,٧٧٤	٠,٥		٨٥,٣٨٧	٠,٠٠٠	٨٥,٣٨٧	
								٨٥,٣٨٧	٠,٠٠	٨٥,٣٨٧
	اجمالي البند: بالمتر المكعب حصر الاحلال لمشروع car shed فقط خمسة و ثمانون و (٣٨٧ / ١٠٠٠) لاغير									
اجمالي كمية بند الاحلال م ^٣							٨٥,٣٨٧			

[\[-\]](#)[Top](#)[2D Wireframe](#)



Notes:

1. THE COPYRIGHT OF THIS DRAWING IS VESTED IN TOURSPOONERS AND IT MAY NOT BE REPRODUCED IN WHOLE OR PART OR USED FOR THE MANUFACTURE OF ANY ARTICLE WITHOUT THE EXPRESS PERMISSION OF THE COPYRIGHT HOLDERS.

2. WORK TO FIGURED DIMENSIONS ONLY.

Key plane

Before

Instructor :

YourSpreadsheets

Address line 1
Address line 2
Telephone line 1
Fax line 1
www.YourSpreadsheets.co.uk

CLIENT: **BAH i CLIENT**
3 Mossadak, Ad Doqi, Dokki,
Giza Governorate, Giza,
Egypt

ARCHITECT: Amr Mamdoh
40 Mossadak, Ad Doqi, Dokki,
Giza Governorate, Giza,
Egypt

SITE: 31 ROVER ROAD
BLOCK A AND B

TITLE: RC DETAILS AND SECTIONS
OF GROUND BEAMS

SCALE AT A2: 1:50, 1:100	DATE: 05/09/13	DRAWN: DJ	CHECKED: DJ
PROJECT NO: 24567	DRAWING NO: A2/248		REVISION: C

صور الحصر الفعلي



Notes:

1. THE COPYRIGHT OF THIS DRAWING IS VESTED IN YOURSPREADSHEETS AND IT MAY NOT BE REPRODUCED IN WHOLE OR PART OR USED FOR THE MANUFACTURE OF ANY ARTICLE WITHOUT THE EXPRESS PERMISSION OF THE COPYRIGHT HOLDERS.
2. WORK TO FIGURED DIMENSIONS ONLY.

Key plane

Before

Instructor :

YourSpreadsheets

Address line 1
Address line 2
Telephone line 1
Fax line 1
www.YourSpreadsheets.co.uk




CLIENT: **BAHI CLIENT**
3 Mossadak, Ad Doqi, Dokki,
Giza Governorate, Giza,
Egypt

ARCHITECT: **Amr Mamdoh**
40 Mossadak, Ad Doqi, Dokki,
Giza Governorate, Giza,
Egypt


SITE: **31 ROVER ROAD
BLOCK A AND B**

TITLE: **RC DETAILS AND SECTIONS
OF GROUND BEAMS**

SCALE AT A2: 1:50, 1:100	DATE: 05/09/13	DRAWN: DJ	CHECKED: DJ
PROJECT NO: 24567	DRAWING NO: A2/248	REVISION: C	

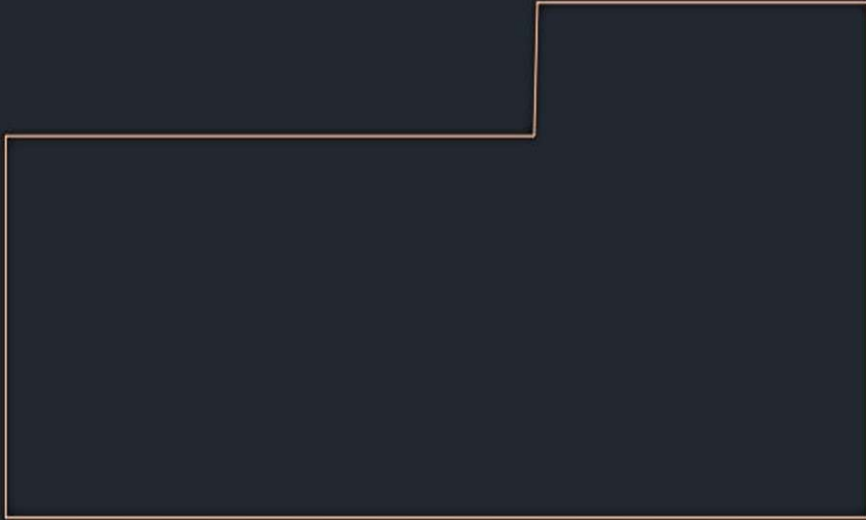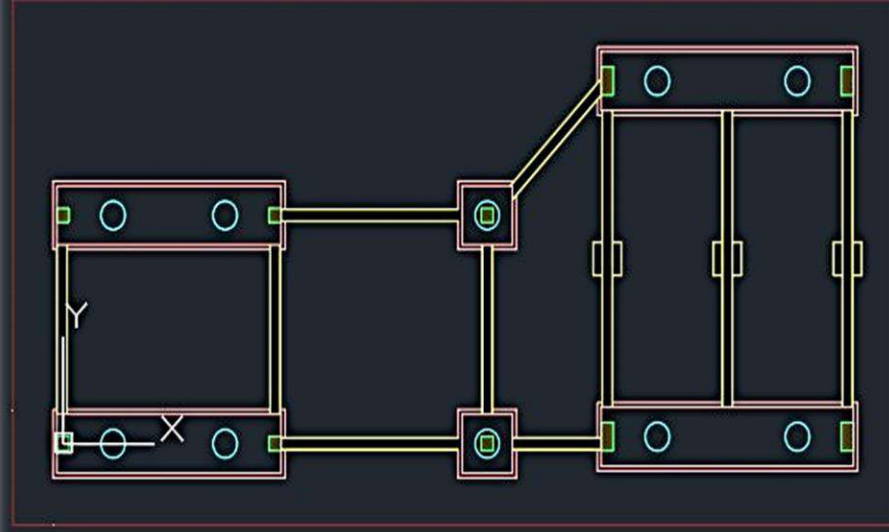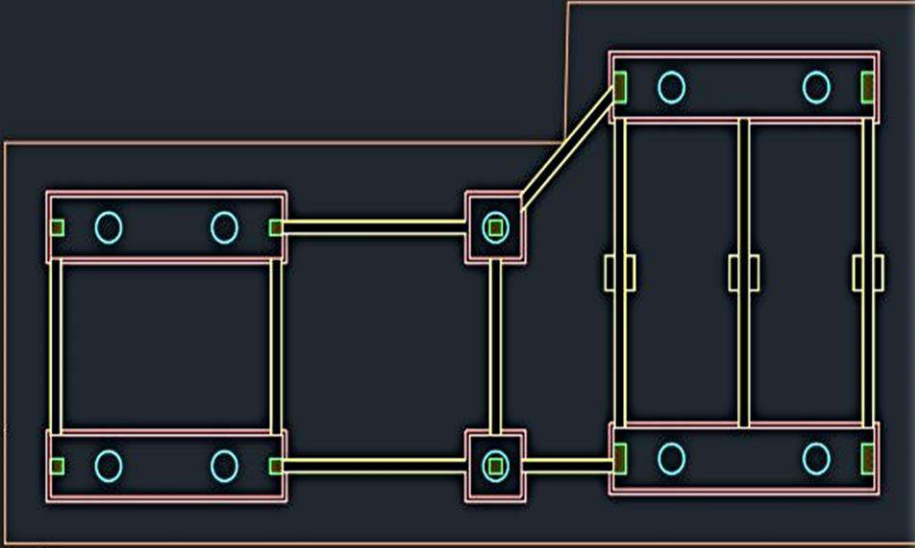

صور الحصر الهندسي للإحلال؟؟؟

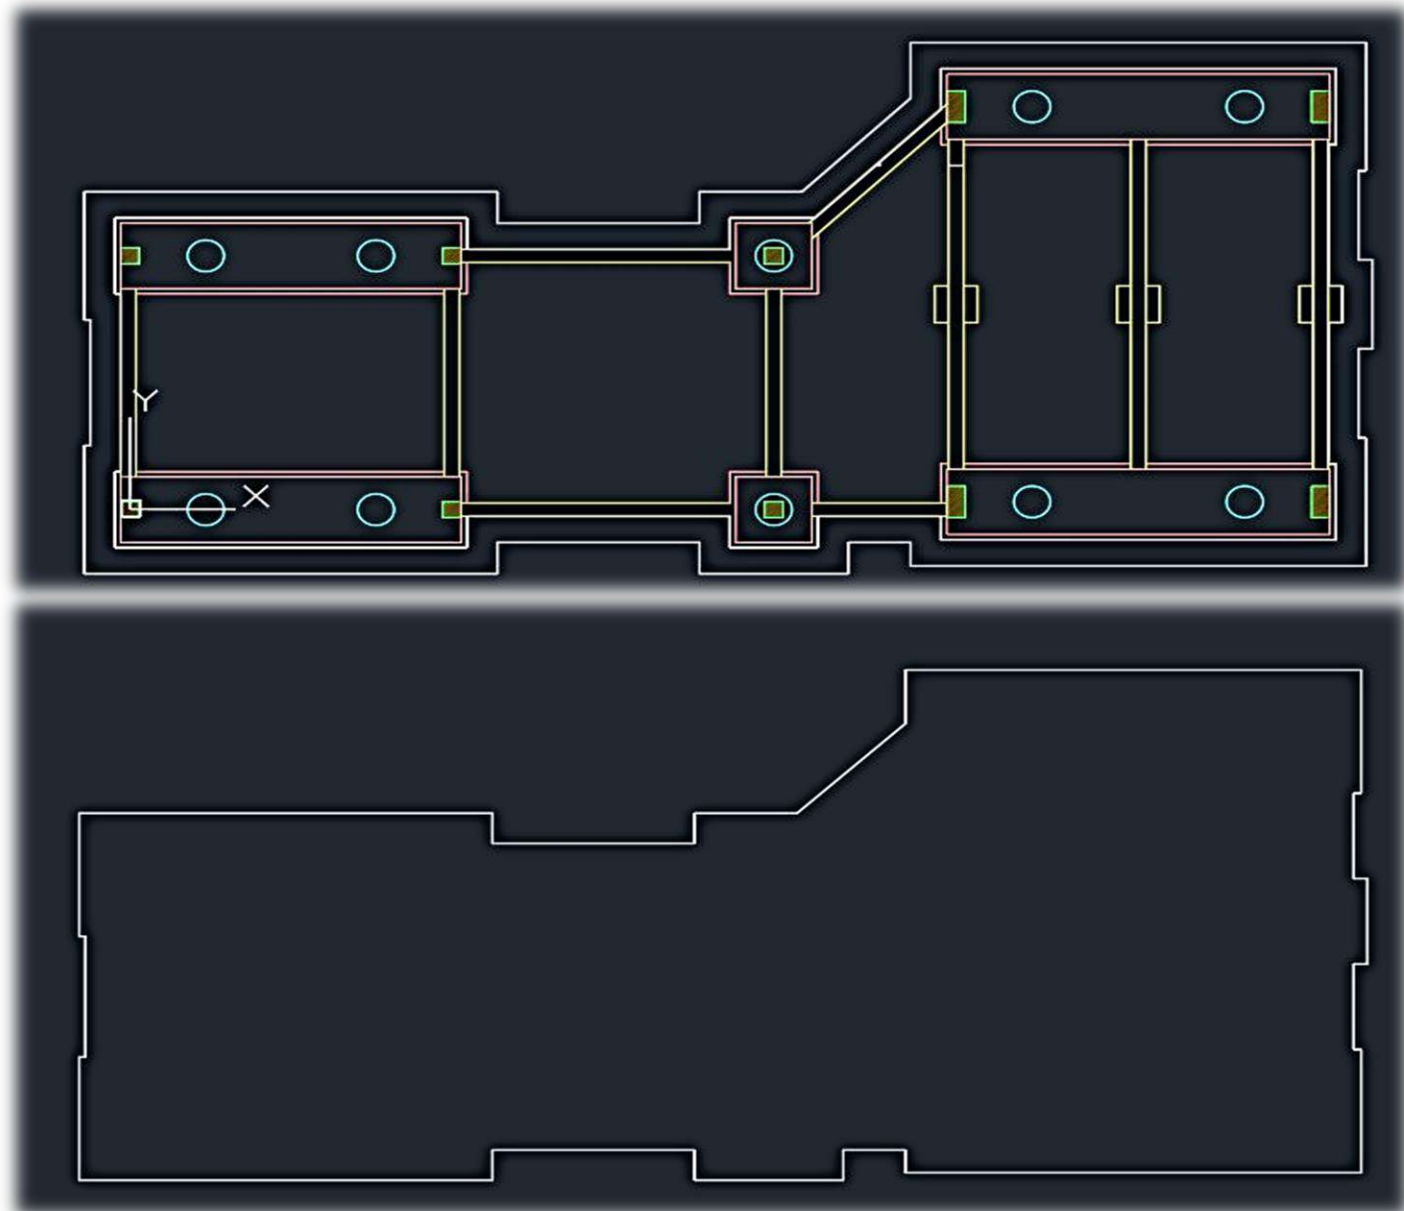

Notes:

1. THE COPYRIGHT OF THIS DRAWING IS VESTED IN YOURSPREADSHEETS AND IT MAY NOT BE REPRODUCED IN WHOLE OR PART OR USED FOR THE MANUFACTURE OF ANY ARTICLE WITHOUT THE EXPRESS PERMISSION OF THE COPYRIGHT HOLDERS.
2. WORK TO FIGURED DIMENSIONS ONLY.

Key plane

Before

Instructor :

YourSpreadsheets

Address line 1
Address line 2
Telephone line 1
Fax line 1
www.YourSpreadsheets.co.uk

CLIENT: **BAHI CLIENT**
3 Mossadak, Ad Doqi, Dokki,
Giza Governorate, Giza,
Egypt

ARCHITECT: **Amr Mamdoh**
40 Mossadak, Ad Doqi, Dokki,
Giza Governorate, Giza,
Egypt

SITE: **31 ROVER ROAD
BLOCK A AND B**

TITLE: **RC DETAILS AND SECTIONS
OF GROUND BEAMS**

SCALE AT A2: 1:50, 1:100	DATE: 05/09/13	DRAWN: DJ	CHECKED: DJ
PROJECT NO: 24567	DRAWING NO: A2/248	REVISION: C	

THE END

COURSE: TECHNICAL OFFICE G46

Name: Ibrahim Mohamed Read

Eng: Amr Mamdouh

Lecture: 5

Task: 3

Arvil Group
CONSTRUCTION & TRAINING COMPANY

1. THE COPYRIGHT OF THIS DRAWING IS VESTED IN TOWERSPENCER AND IT MAY NOT BE REPRODUCED IN WHOLE OR PART OR USED FOR THE MANUFACTURE OF ANY ARTICLE WITHOUT THE EXPRESS PERMISSION OF THE COPYRIGHT HOLDERS.

2. WORK TO FIGURED DIMENSIONS ONLY.

Before

Address line 1
Address line 2
Telephone line 1
Fax line 1
www.YourSpreadsheets.co.uk

ARCHITECT: Amr Mamdoh
40 Mossadak, Ad Doqi, Dokki,
Giza Governorate, Giza,
Egypt

SCALE AT A2: 1:50, 1:100	DATE: 05/09/13	DRAWN: DJ	CHECKED: DJ
PROJECT NO: 24567	DRAWING NO: A2/248	REVISION: C	

[illegible]

Arvil Group
CONSTRUCTION & TRAINING COMPANY

1. THE COPYRIGHT OF THIS DRAWING IS VESTED IN TONSPOODSHEET AND IT MAY NOT BE REPRODUCED IN WHOLE OR PART OR USED FOR THE MANUFACTURE OF ANY ARTICLE WITHOUT THE EXPRESS PERMISSION OF THE COPYRIGHT HOLDERS.

2. WORK TO FIGURED DIMENSIONS ONLY.

Address line 1
Address line 2
Telephone line 1
Fax line 1
www.YourSpreadsheets.co.uk

SCALE AT A2: 1:50, 1:100	DATE: 05/09/13	DRAWN: DJ	CHECKED: DJ
PROJECT NO: 24567	DRAWING NO: A2/248	REVISION: C	

[illegible]

الحصر الهندسي لخرسانة السمات ؟؟؟



Notes:

1. THE COPYRIGHT OF THIS DRAWING IS VESTED IN YOURSPREADSHEETS AND IT MAY NOT BE REPRODUCED IN WHOLE OR PART OR USED FOR THE MANUFACTURE OF ANY ARTICLE WITHOUT THE EXPRESS PERMISSION OF THE COPYRIGHT HOLDERS.
2. WORK TO DIMENSIONS ONLY.

Key plane

Before

Instructor :

YourSpreadsheets

Address line 1
Address line 2
Telephone line 1
Fax line 1
www.YourSpreadsheets.co.uk

CLIENT: BAH i CLIENT
3 Mossadak, Ad Doqi, Dokki,
Giza Governorate, Giza,
Egypt

ARCHITECT: Amr Mamdoh
40 Mossadak, Ad Doqi, Dokki,
Giza Governorate, Giza,
Egypt

SITE: 31 ROVER ROAD
BLOCK A AND B

TITLE: RC DETAILS AND SECTIONS
OF GROUND BEAMS

SCALE AT A2: 1:50, 1:100	DATE: 05/09/13	DRAWN: DJ	CHECKED: DJ
PROJECT NO: 24567	DRAWING NO: A2/248	REVISION: C	

رقم البند	نوع الأعمال و التوريدات	وحدة القياس	عدد	مقاسات			مسطحات أو مكعبات		إجمالي بعد التنزيلات	ملاحظات
				الطول	العرض	ارتفاع	اجمالي	تنزيلات		
	البند: بالمتر المكعب حصر الخرسانة المسلحة للسمات على محاور x مشروع car shed									
	بين محور Ax ومحور Bx	م ^٢	١	٢,٠٧٩	٠,٢٥٠	٠,٥	٠,٢٦٠	٠,٠٠٠	٠,٢٦٠	
	محور Bx	م ^٢	١	٤,٣٢٥	٠,٢٥٠	٠,٥	٠,٥٤١	٠,٠٠٠	٠,٥٤١	
	محور Cx	م ^٢	٢	٦,٣٥٠	٠,٢٥٠	٠,٥	١,٥٨٨	٠,٠٠٠	١,٥٨٨	
	إجمالي البند: بالمتر المكعب حصر الخرسانة المسلحة للسمات على محاور x مشروع car shed فقط اثنان و (٣٨٨ / ١٠٠٠) لاغير									
رقم البند	نوع الأعمال و التوريدات	وحدة القياس	عدد	مقاسات			مسطحات أو مكعبات		إجمالي بعد التنزيلات	ملاحظات
				الطول	العرض	ارتفاع	اجمالي	تنزيلات		
	البند: بالمتر المكعب حصر الخرسانة المسلحة للسمات على محاور y مشروع car shed									
	محور ١x	م ^٢	١	٣,٤٠٠	٠,٣٠٠	٠,٥	٠,٥١٠	٠,٠٠٠	٠,٥١٠	
	محور ٢x	م ^٢	١	٣,٤٠٠	٠,٢٥٠	٠,٥	٠,٤٢٥	٠,٠٠٠	٠,٤٢٥	
	محور ٣x	م ^٢	١	٣,٤٠٠	٠,٣٠٠	٠,٥	٠,٥١٠	٠,٠٠٠	٠,٥١٠	
	محور ٤x	م ^٢	١	٦,١٠٠	٠,٣٠٠	٠,٥	٠,٩١٥	٠,٠٠٠	٠,٩١٥	
	بين محور ٤x ومحور ٥x	م ^٢	١	٦,١٠٠	٠,٣٠٠	٠,٥	٠,٩١٥	٠,٠٠٠	٠,٩١٥	
	محور ٥x	م ^٢	١	٦,١٠٠	٠,٣٠٠	٠,٥	٠,٩١٥	٠,٠٠٠	٠,٩١٥	
	إجمالي البند: بالمتر المكعب حصر الخرسانة المسلحة للسمات على محاور y مشروع car shed فقط أربعة و (١٩٠ / ١٠٠٠) لاغير									
اجمالي كمية الخرسانة المسلحة (قواعد + سمات) م ^٣							٨,٩٦٦			

[\[-\]](#)[\[Top\]](#)[\[2D Wireframe\]](#)



Key plane

Instructor :

Address line 1
Address line 2
Telephone line 1
Fax line 1
www.YourSpreadsheets.co.uk

ARCHITECT: Amr Mamdoh
40 Mossadak, Ad Doqi, Dokki,
Giza Governorate, Giza,
Egypt

TITLE: RC DETAILS AND SECTIONS
OF GROUND BEAMS

SCALE AT A2: 1:50, 1:100	DATE: 05/09/13	DRAWN: DJ	CHECKED: DJ
PROJECT NO: 24567	DRAWING NO: A2/248	REVISION: C	

جزء جدول اللوحة الهندسية المستخدم في الحصر؟؟؟

MODEL	P.C		
	LENGTH	BREDTH	DEPTH
F1	1450	1450	100
F2	1450	5800	100
F3	1450	6500	100

R.C		
LENGTH	BREDTH	DEPTH
1250	1250	500
1250	5600	500
1250	6300	500

Beam ID	Dimensions(mm)	
	b	h
S1	250	500
S2	300	500



Notes:

1. THE COPYRIGHT OF THIS DRAWING IS VESTED IN YOURSPREADSHEETS AND IT MAY NOT BE REPRODUCED IN WHOLE OR PART OR USED FOR THE MANUFACTURE OF ANY ARTICLE WITHOUT THE EXPRESS PERMISSION OF THE COPYRIGHT HOLDERS.
2. WORK TO DIMENSIONS ONLY.

Key plane

Before

Instructor :

YourSpreadsheets

Address line 1
Address line 2
Telephone line 1
Fax line 1
www.YourSpreadsheets.co.uk

CLIENT: BAH i CLIENT
3 Mossadak, Ad Doqi, Dokki,
Giza Governorate, Giza,
Egypt

ARCHITECT: Amr Mamdoh
40 Mossadak, Ad Doqi, Dokki,
Giza Governorate, Giza,
Egypt

SITE: 31 ROVER ROAD
BLOCK A AND B

TITLE: RC DETAILS AND SECTIONS
OF GROUND BEAMS

SCALE AT A2: 1:50, 1:100	DATE: 05/09/13	DRAWN: DJ	CHECKED: DJ
PROJECT NO: 24567	DRAWING NO: A2/248	REVISION: C	

THE END

COURSE: TECHNICAL OFFICE G46

Name: Ibrahim Mohamed Read

Eng: Amr Mamdouh

Lecture: 6

Task: 4

الحصر الهندسي لخرسانة الأعمدة؟؟؟



Notes:

1. THE COPYRIGHT OF THIS DRAWING IS VESTED IN YOURSPREADSHEETS AND IT MAY NOT BE REPRODUCED IN WHOLE OR PART OR USED FOR THE MANUFACTURE OF ANY ARTICLE WITHOUT THE EXPRESS PERMISSION OF THE COPYRIGHT HOLDERS.

2. WORK TO DIMENSIONS ONLY.

Key plane

Before

Instructor :

YourSpreadsheets

Address line 1
Address line 2
Telephone line 1
Fax line 1
www.YourSpreadsheets.co.uk

CLIENT: BAH i CLIENT
3 Mossadak, Ad Doqi, Dokki,
Giza Governorate, Giza,
Egypt

ARCHITECT: Amr Mamdoh
40 Mossadak, Ad Doqi, Dokki,
Giza Governorate, Giza,
Egypt

SITE: 31 ROVER ROAD
BLOCK A AND B

TITLE: RC DETAILS AND SECTIONS
OF GROUND BEAMS


SCALE AT A2: 1:50, 1:100	DATE: 05/09/13	DRAWN: DJ	CHECKED: DJ
PROJECT NO: 24567	DRAWING NO: A2/248	REVISION: C	

رقم البند	نوع الأعمال و التوريدات	وحدة القياس	عدد	مقاسات			مسطحات أو مكعبات		إجمالي بعد التنزيلات	ملاحظات	
				الطول	العرض	ارتفاع	اجمالي	تنزيلات			
	البند: بالمتر المكعب حصر خرسانة الأعمدة مشروع car shed										
	c1	م ^٢	٦	٠,٣٠٠	٠,٣٠٠	٤,٤٥	٢,٤٠٣	٠,٠٠٠	٢,٤٠٣		
	c2	م ^٢	١	٠,٣٠٠	٠,٦٠٠	٤,٤٥	٠,٨٠١	٠,٠٠٠	٠,٨٠١		
	c2	م ^٢	٣	٠,٣٠٠	٠,٦٠٠	٥	٢,٧٠٠	٠,٠٠٠	٢,٧٠٠		
									٥,٩٠٤	٠,٠٠٠	٥,٩٠٤
	إجمالي البند: بالمتر المكعب حصر خرسانة الأعمدة مشروع car shed فقط خمسة و (٩٠٤/ ١٠٠٠) لاغير										

اجمالي كمية خرسانة الأعمده م ^٣	٥,٩٠٤
---	-------

رسم توضيحي لحساب ارتفاع العمود؟؟؟

ظهر السقف الخرساني

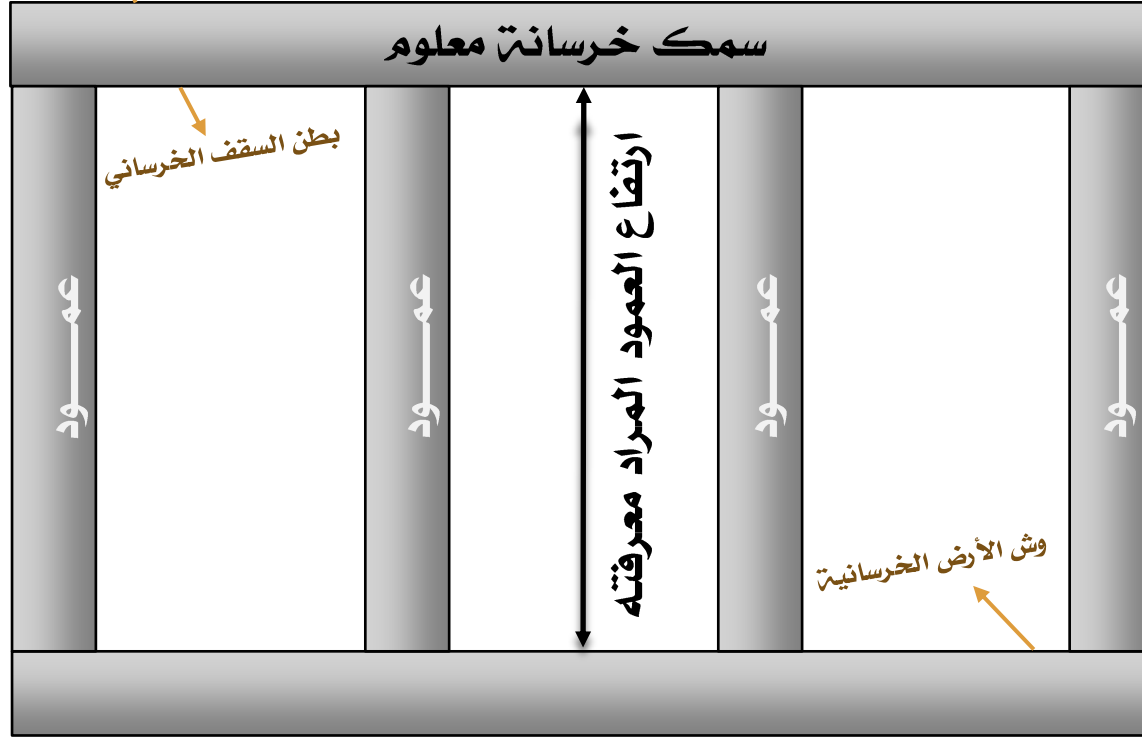

(A) منسوب معلوم

(C) منسوب مجهول

(B) منسوب معلوم

يتم حساب ارتفاع العمود هندسيا

من وش الأرضية الخرسانية الى بطن السقف الخرساني

لذلك لابد من الحصول على المنسوب المجهول (C)

وطرحه من المنسوب المعلوم (B)

المنسوب مجهول (C) = المنسوب معلوم (A) - سمك الخرسانة المعلوم

ارتفاع العمود المراد معرفته = المنسوب مجهول (C) - المنسوب المعلوم (B)

يتم ذلك في الحصر الهندسي ولا يتم في الحصر الفعلي



Notes:

1. THE COPYRIGHT OF THIS DRAWING IS VESTED IN YOURSPREADSHEETS AND IT MAY NOT BE REPRODUCED IN WHOLE OR PART OR USED FOR THE MANUFACTURE OF ANY ARTICLE WITHOUT THE EXPRESS PERMISSION OF THE COPYRIGHT HOLDERS.
2. WORK TO DIMENSIONED DIMENSIONS ONLY.

Key plane

Before

Instructor :

YourSpreadsheets

Address line 1
Address line 2
Telephone line 1
Fax line 1
www.YourSpreadsheets.co.uk

CLIENT: BAH i CLIENT
3 Mossadak, Ad Doqi, Dokki,
Giza Governorate, Giza,
Egypt

ARCHITECT: Amr Mamdoh
40 Mossadak, Ad Doqi, Dokki,
Giza Governorate, Giza,
Egypt

SITE: 31 ROVER ROAD
BLOCK A AND B

TITLE: RC DETAILS AND SECTIONS
OF GROUND BEAMS

SCALE AT A2: 1:50, 1:100	DATE: 05/09/13	DRAWN: DJ	CHECKED: DJ
PROJECT NO: 24567	DRAWING NO: A2/248	REVISION: C	

اللوحة الهندسية؟؟؟



Notes:

1. THE COPYRIGHT OF THIS DRAWING IS VESTED IN YOURSPREADSHEETS AND IT MAY NOT BE REPRODUCED IN WHOLE OR PART OR USED FOR THE MANUFACTURE OF ANY ARTICLE WITHOUT THE EXPRESS PERMISSION OF THE COPYRIGHT HOLDERS.
2. WORK TO DIMENSIONED DIMENSIONS ONLY.

Key plane

Before

Instructor :

YourSpreadsheets

Address line 1
Address line 2
Telephone line 1
Fax line 1
www.YourSpreadsheets.co.uk



CLIENT: **BAHI CLIENT**
3 Mossadak, Ad Doqi, Dokki,
Giza Governorate, Giza,
Egypt

ARCHITECT: **Amr Mamdoh**
40 Mossadak, Ad Doqi, Dokki,
Giza Governorate, Giza,
Egypt

SITE: **31 ROVER ROAD
BLOCK A AND B**

TITLE: **RC DETAILS AND SECTIONS
OF GROUND BEAMS**

SCALE AT A2: 1:50, 1:100	DATE: 05/09/13	DRAWN: DJ	CHECKED: DJ
PROJECT NO: 24567	DRAWING NO: A2/248	REVISION: C	

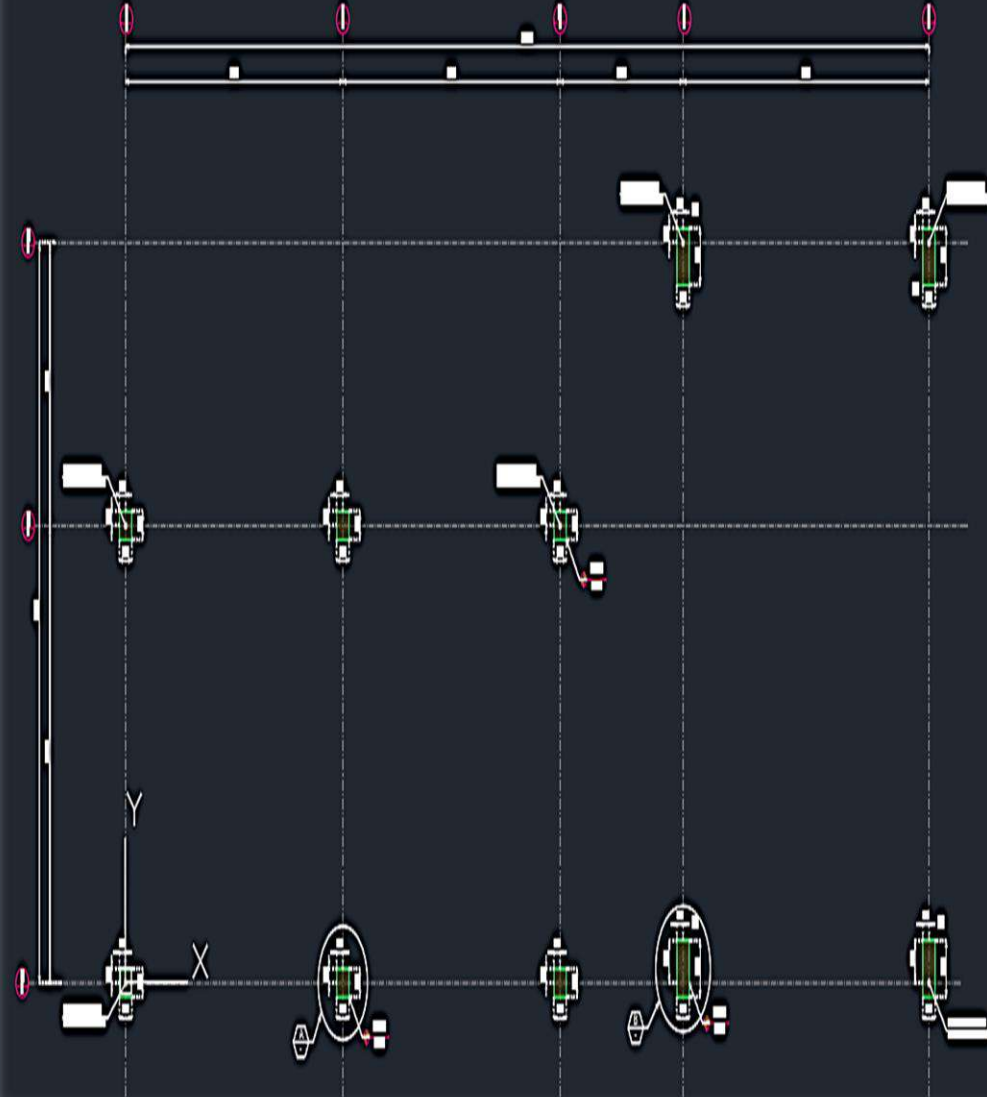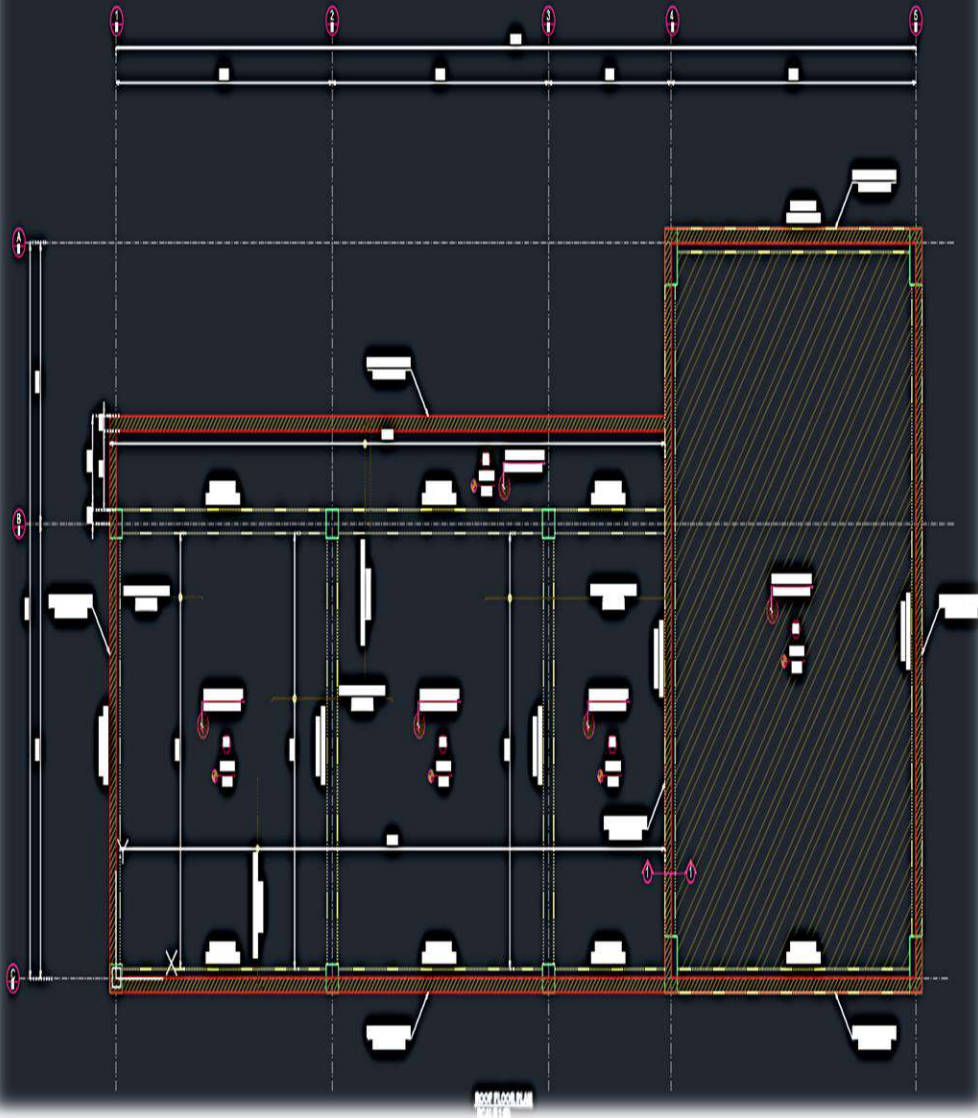


لوحة السكشن موضح عليها المناسيب والبيانات وجداول اللوحة الهندسية المستخدم في الحصر؟؟؟

MODEL	P.C				R.C			
	LENGTH	BREDTH	DEPTH	T.O.PC	LENGTH	BREDTH	DEPTH	T.O.C
F1	1450	1450	100	(-1.50)	1250	1250	500	(-1.00)
F2	1450	5800	100	(-1.50)	1250	5600	500	(-1.00)
F3	1450	6500	100	(-1.50)	1250	6300	500	(-1.00)




C1 (300X300)

A DETAIL (C1)
Scale 1 : 25

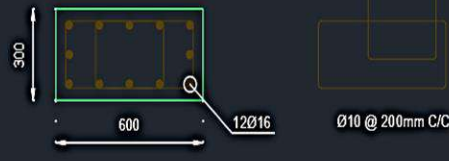

C2 (300X600)

B DETAIL (C2)
Scale 1 : 25

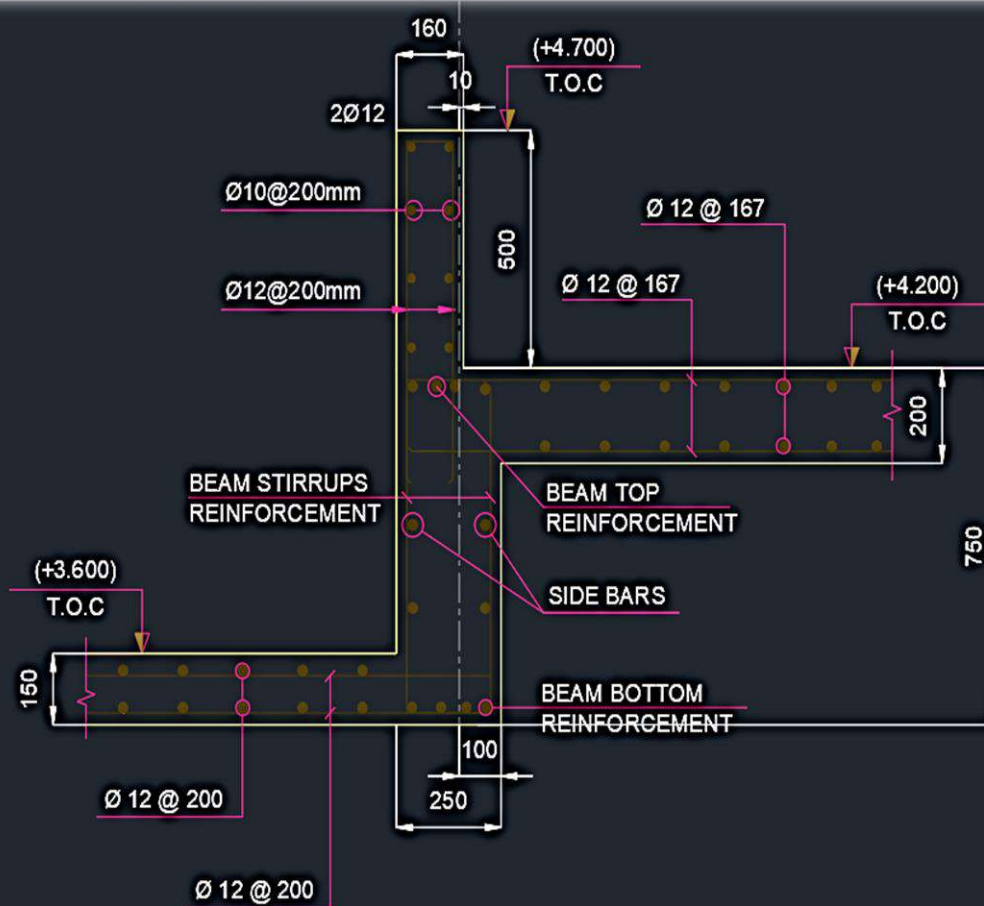

Notes:

1. THE COPYRIGHT OF THIS DRAWING IS VESTED IN YOURSPREADSHEETS AND IT MAY NOT BE REPRODUCED IN WHOLE OR PART OR USED FOR THE MANUFACTURE OF ANY ARTICLE WITHOUT THE EXPRESS PERMISSION OF THE COPYRIGHT HOLDERS.
2. WORK TO DIMENSIONS ONLY.

Key plane

Before

Instructor :

YourSpreadsheets

Address line 1
Address line 2
Telephone line 1
Fax line 1
www.YourSpreadsheets.co.uk

CLIENT: **BAHI CLIENT**
3 Mossadak, Ad Doqi, Dokki,
Giza Governorate, Giza,
Egypt

ARCHITECT: **Amr Mamdoh**
40 Mossadak, Ad Doqi, Dokki,
Giza Governorate, Giza,
Egypt

SITE: **31 ROVER ROAD
BLOCK A AND B**

TITLE: **RC DETAILS AND SECTIONS
OF GROUND BEAMS**

SCALE AT A2: 1:50, 1:100	DATE: 05/09/13	DRAWN: DJ	CHECKED: DJ
PROJECT NO: 24567	DRAWING NO: A2/248	REVISION: C	

THE END

Course: Technical Office G46

NAME: IBRAHIM MOHAMED READ

ENG: AMR MAMDOUH

LECTURE: 7

TASK: 5



الحصر الهندسي لخرسانتة سقف Solid Slab

رقم البند	نوع الأعمال و التوريدات	وحدة القياس	عدد	مقاسات الإضافة		إجمالي المكعبات المضافة	مقاسات التتريلات		إجمالي التتريلات	إجمالي بعد التتريلات	ملاحظات
				المسطح	السمك		المسطح	السمك			
	البند: بالمتر المكعب حصر خرسانة سقف Solid slab على ملف Solid slab										
	البلاطات	م ^٢		٣٣٨١,٨٤٥	٠,١٦	٥٤١,٠٩٥			٠,٠٠٠	٥٤١,٠٩٥	
	باكيتة س ١ سمك ١٤	م ^٢				٠,٠٠٠	٣٢,٢٩٩	٠,٢٠٠	٦,٤٦٠	٦,٤٦٠	
	باكيتة س ٢ سمك ١٤	م ^٢				٠,٠٠٠	٣٢,٢٩٩	٠,٢٠٠	٦,٤٦٠	٦,٤٦٠	
	باكيتة س ٣ سمك ١٤	م ^٢				٠,٠٠٠	٣٢,٢٩٩	٠,٢٠٠	٦,٤٦٠	٦,٤٦٠	
	باكيتة س ٤ سمك ١٤	م ^٢				٠,٠٠٠	٣٢,٤١٩	٠,٢٠٠	٦,٤٨٤	٦,٤٨٤	
	باكيتة س ٥ سمك ١٤	م ^٢				٠,٠٠٠	١١,٢١٦	٠,٢٠٠	٢,٢٤٣	٢,٢٤٣	
	باكيتة س ٦ سمك ١٤	م ^٢				٠,٠٠٠	١١,٢١٦	٠,٢٠٠	٢,٢٤٣	٢,٢٤٣	
	باكيتة س ٧ سمك ١٤	م ^٢				٠,٠٠٠	١١,٢١٦	٠,٢٠٠	٢,٢٤٣	٢,٢٤٣	
	باكيتة س ٨ سمك ١٤	م ^٢				٠,٠٠٠	١١,٢٥٦	٠,٢٠٠	٢,٢٥١	٢,٢٥١	
	باكيتة س ٩ سمك ١٤	م ^٢				٠,٠٠٠	٣١,١٥٤	٠,٢٠٠	٦,٢٣١	٦,٢٣١	



Notes:

1. THE COPYRIGHT OF THIS DRAWING IS VESTED IN YOURSPREADSHEETS AND IT MAY NOT BE REPRODUCED IN WHOLE OR IN PART OR USED FOR THE MANUFACTURE OF ANY ARTICLE WITHOUT THE EXPRESS PERMISSION OF THE COPYRIGHT HOLDERS.
2. WORK TO REQUIRED DIMENSIONS ONLY.

Key plane

Before

Instructor :

YourSpreadsheets

Address line 1
Address line 2
Telephone line 1
Fax line 1
www.YourSpreadsheets.co.uk

CLIENT: BAH & CLIENT
3 Mossadah, Ad Doui, Dokki,
Giza Governorate, Giza,
Egypt

ARCHITECT: Amr Mamdoh
40 Mossadah, Ad Doui, Dokki,
Giza Governorate, Giza,
Egypt

SITE: 31 ROVER ROAD
BLOCK A AND B

TITLE: RC DETAILS AND SECTIONS
OF GROUND BEAMS

SCALE AT A2: 1:50, 1:100	DATE: 05/09/13	DRAWN: DJ	CHECKED: DJ
PROJECT NO: 24567	DRAWING NO: A2/248	REVISION: C	

الحصر الهندسي لخرسانة سقف Solid Slab

	٢,٢٧٧-	٢,٢٧٧	٠,١٦٠	١٤,٢٢٩	٠,٠٠٠			م	سلم من ١٠ سمك ٢٠	
	٢,٣٩٢-	٢,٣٩٢	٠,٢٠٠	١١,٩٦٠	٠,٠٠٠			م	فواتير من ١١ سمك ١٤	
	٥,٦٩٤-	٥,٦٩٤	٠,٢٠٠	٢٨,٤٧٢	٠,٠٠٠			م	باكيت من ١٢ سمك ١٤	
	٥,٦٧٨-	٥,٦٧٨	٠,٢٠٠	٢٨,٣٩٠	٠,٠٠٠			م	باكيت من ١٣ سمك ١٤	
	٥,٦٨٢-	٥,٦٨٢	٠,٢٠٠	٢٨,٤١١	٠,٠٠٠			م	باكيت من ١٤ سمك ١٤	
	٦,٧٩٥-	٦,٧٩٥	٠,٢٠٠	٣٣,٩٧٦	٠,٠٠٠			م	باكيت من ١٥ سمك ١٤	
	١,٨٠٧-	١,٨٠٧	٠,٢٠٠	٩,٠٣٥	٠,٠٠٠			م	باكيت من ١٦ سمك ١٤	
	١,٨٠٩-	١,٨٠٩	٠,٢٠٠	٩,٠٤٧	٠,٠٠٠			م	باكيت من ١٧ سمك ١٤	
	٤,٦٩٦-	٤,٦٩٦	٠,٢٠٠	٢٣,٤٧٩	٠,٠٠٠			م	باكيت من ١٨ سمك ١٤	
	١٣,٧٩٠	٠,٠٠٠			١٣,٧٩٠	٠,٦	٢٢,٩٨٣	م	باكيت من ١٩ سمك ٢٢	
	١,٦٧٥-	١,٦٧٥	٠,٢٠٠	٨,٣٧٤	٠,٠٠٠			م	باكيت من ٢٠ سمك ١٤	
	٦٥,٧٩٢-	٦٥,٧٩٢	١٦,٠٠٠	٤,١١٢	٠,٠٠٠			م	فتحات من ٢١	
	٤٠٩,٥١٣	١٤٥,٣٧		٣٢,٣٠	٥٥٤,٨٨٥					
					إجمالي البنود: بالمتر المكعب حصر خرسانة سقف Solid slab على ملف Solid slab فقط أربعمائة وتسعة و (١٠٠٠/ ٥١٣) لاغير					
٤٠٩,٥١٣					إجمالي كمية خرسانة سقف Solid Slab على ملف Solid Slab ٣م					



Notes:

1. THE COPYRIGHT OF THIS DRAWING IS VESTED IN YOURSPREADSHEETS AND IF ANY NOT BE REPRODUCED IN WHOLE OR IN PART OR USED FOR THE MANUFACTURE OF ANY ARTICLE WITHOUT THE EXPRESS PERMISSION OF THE COPYRIGHT HOLDERS.

2. WORK TO REQUIRED DIMENSIONS ONLY.

Key plane

Before

Instructor :

YourSpreadsheets

Address line 1
Address line 2
Telephone line 1
Fax line 1
www.YourSpreadsheets.co.uk

CLIENT: BAH & CLIENT
3 Mossadeh, Ad Dora, Dokki,
Giza Governorate, Giza,
Egypt

ARCHITECT: Amr Mamdoh
40 Mossadeh, Ad Dora, Dokki,
Giza Governorate, Giza,
Egypt

DATE: 31 ROVER ROAD
BLOCK A AND B

TITLE: RC DETAILS AND SECTIONS
OF GROUND BEAMS

SCALE AT A2: 1:50, 1:100	DATE: 05/09/13	DRAWN: DJ	CHECKED: DJ
PROJECT NO: 24567	DRAWING NO: A2/248	REVISION: C	

الحصر الهندسي لكمرات سقف Solid Slab ؟؟؟



Notes:

1. THE COPYRIGHT OF THIS DRAWING IS VESTED IN YOURSPREADSHEETS AND IF ANY NOT BE REPRODUCED IN WHOLE OR IN PART OR USED FOR THE MANUFACTURE OF ANY ARTICLE WITHOUT THE EXPRESS PERMISSION OF THE COPYRIGHT HOLDERS.
2. WORK TO REQUIRED DIMENSIONS ONLY.

Key plane

Before

Instructor :

YourSpreadsheets

Address line 1
Address line 2
Telephone line 1
Fax line 1
www.YourSpreadsheets.co.uk

CLIENT: BAH & CLIENT
3 Mossadeh, Ad Dami, Dokki,
Giza Governorate, Giza,
Egypt

ARCHITECT: Amr Mamedoh
40 Mossadeh, Ad Dami, Dokki,
Giza Governorate, Giza,
Egypt

SITE: 31 ROVER ROAD
BLOCK A AND B

TITLE: RC DETAILS AND SECTIONS
OF GROUND BEAMS

SCALE AT A2: 1:50, 1:100	DATE: 05/09/13	DRAWN: DJ	CHECKED: DJ
PROJECT NO: 24567	DRAWING NO: A2/248	REVISION: C	

رقم البند	نوع الأعمال و التوريدات	وحدة القياس	عدد	مقاسات			الإجمالي	التنزيلات	إجمالي بعد التنزيلات	ملاحظات
				الطول	العرض	السمك				
	البند: بالمتر المكعب حصر كمرات سقف Solid slab على محاور x على ملف Solid slab									
	محور ١ - ١	م ^٢		٣٧,٢٧	٠,٢٥٠	٠,٥٤	٥,٠٣١	٠,٠٠٠	٥,٠٣١	
	محور ٢ - ٢	م ^٢		٤٧,٥٨	٠,٢٥٠	٠,٥٤	٦,٤٢٣	٠,٠٠٠	٦,٤٢٣	
	محور ٣ - ٣	م ^٢		٦٠,٢٨٨	٠,٢٥٠	٠,٥٤	٨,١٣٩	٠,٠٠٠	٨,١٣٩	
	محور ٤ - ٤	م ^٢		٦٢,٥٤	٠,٢٥٠	٠,٥٤	٨,٤٤٣	٠,٠٠٠	٨,٤٤٣	
	محور ٥ - ٥	م ^٢		٦٥,٦١	٠,٢٥٠	٠,٥٤	٨,٨٥٧	٠,٠٠٠	٨,٨٥٧	
	بين محور ٥ - ٥ ومحور ٦ - ٦	م ^٤		٦,٩٤٢	٠,٢٥٠	٠,٥٤	٠,٩٣٧	٠,٠٠٠	٠,٩٣٧	
	محور ٦ - ٦	م ^٢		٥٩,٦٦	٠,٢٥٠	٠,٥٤	٨,٠٥٤	٠,٠٠٠	٨,٠٥٤	
	محور ٧ - ٧	م ^٢		٤٧,١٨	٠,٢٥٠	٠,٥٤	٦,٣٦٩	٠,٠٠٠	٦,٣٦٩	
	محور ٧ - ٧	م ^٢		٣,٢١	٠,١٢٠	٠,٥٤	٠,٢٠٨	٠,٠٠٠	٠,٢٠٨	
	محور ٨ - ٨	م ^٢		٤٤,٩٨	٠,٢٥٠	٠,٥٤	٦,٠٧٢	٠,٠٠٠	٦,٠٧٢	
	محور ١٠	م ^٢		٦,٨١	٠,٣٠٠	٠,٥٤	١,١٠٣	٠,٠٠٠	١,١٠٣	
	بين محور ١٠ ومحور ١١	م ^٢		٠,٨٣١	٠,١٢٠	٠,٥٤	٠,٠٥٤	٠,٠٠٠	٠,٠٥٤	

الحصر الهندسي لكمرات سقف Solid Slab ؟؟؟

	١,٠٩٥	٠,٠٠٠	١,٠٩٥	٠,٥٤	٠,٣٠٠	٦,٧٦		م ^٢	محور ١١	
	٠,٠٥٤	٠,٠٠٠	٠,٠٥٤	٠,٥٤	٠,١٢٠	٠,٨٣٤		م ^٢	بين محور ١١ ومحور ١٢	
	١,٠٩٥	٠,٠٠٠	١,٠٩٥	٠,٥٤	٠,٣٠٠	٦,٧٦		م ^٢	محور ١٢	
	٠,٠٥٤	٠,٠٠٠	٠,٠٥٤	٠,٥٤	٠,١٢٠	٠,٨٣٣		م ^٢	بين محور ١٢ ومحور ١٣	
	١,٠٩٥	٠,٠٠٠	١,٠٩٥	٠,٥٤	٠,٣٠٠	٦,٧٦		م ^٢	محور ١٣	
	٠,١٠٩	٠,٠٠٠	٠,١٠٩	٠,٥٤	٠,١٢٠	١,٦٨٦		م ^٢	بين محور ١٣ ومحور ١٤	
	٣,١١٠	٠,٠٠٠	٣,١١٠	٠,٥٤	٠,٢٥٠	٢٣,٠٤		م ^٢	محور ١٤	
	٢,٠٥٢	٠,٠٠٠	٢,٠٥٢	٠,٥٤	٠,٢٥٠	١٥,٢		م ^٢	محور ٢٠	
	٢,٩٥٩	٠,٠٠٠	٢,٩٥٩	٠,٥٤	٠,٢٥٠	٢١,٩٢		م ^٢	محور ٢١	
	٢,٩١١	٠,٠٠٠	٢,٩١١	٠,٥٤	٠,٢٥٠	٢١,٥٦		م ^٢	محور ٢٢	
	٧٤,٢٢٧	٠,٠٠	٧٤,٢٢٧							
			إجمالي البنود: بالمتر المكعب حصر كمرات سقف Solid slab على محاور x على ملف Solid slab فقط أربعة وسبعون و (٢٢٧ / ١٠٠٠) لاغير							
٧٤,٢٢٧				اجمالي كمية حصر كمرات سقف Solid slab على محاور x على ملف Solid slab م ^٣						



Notes:

1. THE COPYRIGHT OF THIS DRAWING IS VESTED IN YOURSPREADSHEETS AND IF ANY NOT BE REPRODUCED IN WHOLE OR IN PART OR USED FOR THE MANUFACTURE OF ANY ARTICLE WITHOUT THE EXPRESS PERMISSION OF THE COPYRIGHT HOLDERS.

2. WORK TO REQUIRED DIMENSIONS ONLY.

Key plane

Before

Instructor :

YourSpreadsheets

Address line 1
Address line 2
Telephone line 1
Fax line 1
www.YourSpreadsheets.co.uk

CLIENT: BAH & CLIENT
3 Mossadeh, Ad Dami, Dokki,
Giza Governorate, Giza,
Egypt

ARCHITECT: Amr Mamdoh
40 Mossadeh, Ad Dami, Dokki,
Giza Governorate, Giza,
Egypt

SITE: 31 ROVER ROAD
BLOCK A AND B

TITLE: RC DETAILS AND SECTIONS
OF GROUND BEAMS

SCALE AT A2: 1:50: 1:100	DATE: 05/09/13	DRAWN: DJ	CHECKED: DJ
PROJECT NO: 24567	DRAWING NO: A2/248	REVISION: C	

الحصر الهندسي لكمرات سقف Solid Slab ؟؟؟

رقم البند	نوع الأعمال و التوريدات	وحدة القياس	عدد	مقاسات			الإجمالي	التنزيلات	إجمالي بعد التنزيلات	ملاحظات
				الطول	العرض	السمك				
	البند: بالمتر المكعب حصر كمرات سقف Solid slab على محاور y على ملف Solid slab									
	محور أ - أ	م ^٢		٤٧,٩	٠,٢٥٠	٠,٥٤	٦,٤٦٧	٠,٠٠٠	٦,٤٦٧	
	محور ب - ب	م ^٢		٤٦,٦٣	٠,٣٠٠	٠,٥٤	٧,٥٥٤	٠,٠٠٠	٧,٥٥٤	
	محور ج - ج	م ^٢		٤٦,٦٣	٠,٣٥٠	٠,٥٤	٨,٨١٣	٠,٠٠٠	٨,٨١٣	
	محور د - د	م ^٢		٤٦,٦٣	٠,٣٥٠	٠,٥٤	٨,٨١٣	٠,٠٠٠	٨,٨١٣	
	محور هـ - هـ	م ^٢		٤٦,٦٣	٠,٣٥٠	٠,٥٤	٨,٨١٣	٠,٠٠٠	٨,٨١٣	
	محور و - و	م ^٢		٤٦,٦٣	٠,٣٠٠	٠,٥٤	٧,٥٥٤	٠,٠٠٠	٧,٥٥٤	
	محور ز - ز	م ^٢		٤٧	٠,٢٥٠	٠,٥٤	٦,٣٤٥	٠,٠٠٠	٦,٣٤٥	
	محور ح - ح	م ^٤		٣٩,٧٥	٠,٢٥٠	٠,٥٤	٥,٣٦٦	٠,٠٠٠	٥,٣٦٦	
	محور ي - ي	م ^٢		٤٠,٩٥	٠,٣٠٠	٠,٥٤	٦,٦٣٤	٠,٠٠٠	٦,٦٣٤	



Notes:

1. THE COPYRIGHT OF THIS DRAWING IS VESTED IN YOURSPREADSHEETS AND IF ANY NOT BE REPRODUCED IN WHOLE OR IN PART OR USED FOR THE MANUFACTURE OF ANY ARTICLE WITHOUT THE EXPRESS PERMISSION OF THE COPYRIGHT HOLDER.

2. WORK TO FOLLOW DRAWING ONLY.

Key plane

Before

Instructor :

YourSpreadsheets

Address line 1
Address line 2
Telephone line 1
Fax line 1
www.YourSpreadsheets.co.uk

CLIENT: BAH & CLIENT
3 Mossadeh, Ad Doui, Dokki,
Giza Governorate, Giza,
Egypt

ARCHITECT: Amr Mamdoh
40 Mossadeh, Ad Doui, Dokki,
Giza Governorate, Giza,
Egypt

SITE: 31 ROVER ROAD
BLOCK A AND B

TITLE: RC DETAILS AND SECTIONS
OF GROUND BEAMS

SCALE AT A2: 1:50, 1:100	DATE: 05/09/13	DRAWN: DJ	CHECKED: DJ
PROJECT NO: 24567	DRAWING NO: A2/248	REVISION: C	

الحصر الهندسي لكمرات سقف Solid Slab ؟؟؟



Notes:

1. THE COPYRIGHT OF THIS DRAWING IS VESTED IN YOURSPREADSHEETS AND IT MAY NOT BE REPRODUCED IN WHOLE OR IN PART OR USED FOR THE MANUFACTURE OF ANY ARTICLE WITHOUT THE EXPRESS PERMISSION OF THE COPYRIGHT HOLDER.

2. WORK TO FOLLOW DRAWING ONLY.

Key plane

Before

محور ك - ك	م ^٣	٢,٦٨	٠,٢٥٠	٠,٥٤	٠,٣٦٢	٠,٠٠٠	٠,٣٦٢
محور ل - ل	م ^٣	٣٣,٦	٠,٢٥٠	٠,٥٤	٤,٥٣٦	٠,٠٠٠	٤,٥٣٦
بين محور ل - ل ومحور م - م	م ^٤	٠,٧٣١	٠,٢٥٠	٠,٥٤	٠,٠٩٩	٠,٠٠٠	٠,٠٩٩
محور م - م	م ^٣	٢٤,٨٢	٠,٣٠٠	٠,٥٤	٤,٠٢١	٠,٠٠٠	٤,٠٢١
محور ن - ن	م ^٣	٢٢,١٨	٠,٢٥٠	٠,٥٤	٢,٩٩٤	٠,٠٠٠	٢,٩٩٤
بين محور ش - ش ومحور س - س	م ^٣	٢,٢٢٣	٠,٢٥٠	٠,٥٤	٠,٣٠٠	١,٠٠٠	٠,٧٠٠

٧٨,٣٧١	٠,٠٠٠	٧٨,٣٧١	
--------	-------	--------	--

إجمالي البند: بالمتر المكعب حصر كمرات سقف Solid slab على محاور y على ملف Solid slab فقط ثمانية وسبعون و (٣٧١ / ١٠٠٠) لاغير			
--	--	--	--

إجمالي كمية حصر كمرات سقف Solid slab على محاور y على ملف Solid slab م ^٣	٧٨,٣٧١
--	--------

إجمالي كمية حصر كمرات سقف Solid slab على جميع المحاور على ملف Solid slab م ^٣	١٥٢,٥٩٧
---	---------

إجمالي كمية خرسانة بلاطة Solid slab م ^٣	٥٦٢,١١٠
--	---------

Instructor :

YourSpreadsheets

Address line 1
Address line 2
Telephone line 1
Fax line 1
www.YourSpreadsheets.co.uk

CLIENT: BAH i CLIENT
3 Mossadeh, Ad Doui, Dokki,
Giza Governorate, Giza,
Egypt

ARCHITECT: Amr Mamdoh
40 Mossadeh, Ad Doui, Dokki,
Giza Governorate, Giza,
Egypt

SITE: 31 ROVER ROAD
BLOCK A AND B

TITLE: RC DETAILS AND SECTIONS
OF GROUND BEAMS

SCALE AT A2: 1:50, 1:100	DATE: 05/09/13	DRAWN: DJ	CHECKED: DJ
PROJECT NO: 24567	DRAWING NO: A2/248	REVISION: C	

اللوحة الهندسية Solid slab



Notes:

1. THE COPYRIGHT OF THIS DRAWING IS VESTED IN YOURSPREADSHEETS AND IF ANY NOT BE REPRODUCED IN WHOLE OR IN PART OR USED FOR THE MANUFACTURE OF ANY ARTICLE WITHOUT THE EXPRESS PERMISSION OF THE COPYRIGHT HOLDERS.
2. WORK TO REQUIRED DIMENSIONS ONLY.

Key plane

Before

Instructor :

YourSpreadsheets

Address line 1
Address line 2
Telephone line 1
Fax line 1
www.YourSpreadsheets.co.uk


CLIENT: BAH i CLIENT
3 Mossadeh, Ad Doui, Dokki,
Giza Governorate, Giza,
Egypt

ARCHITECT: Amr Mamdouh
40 Mossadeh, Ad Doui, Dokki,
Giza Governorate, Giza,
Egypt

DATE: 31 ROVER ROAD
BLOCK A AND B

TITLE: RC DETAILS AND SECTIONS
OF GROUND BEAMS

SCALE AT A2: 1:50, 1:100	DATE: 05/09/13	DRAWN: DJ	CHECKED: DJ
PROJECT NO: 24567	DRAWING NO: A2/248	REVISION: C	

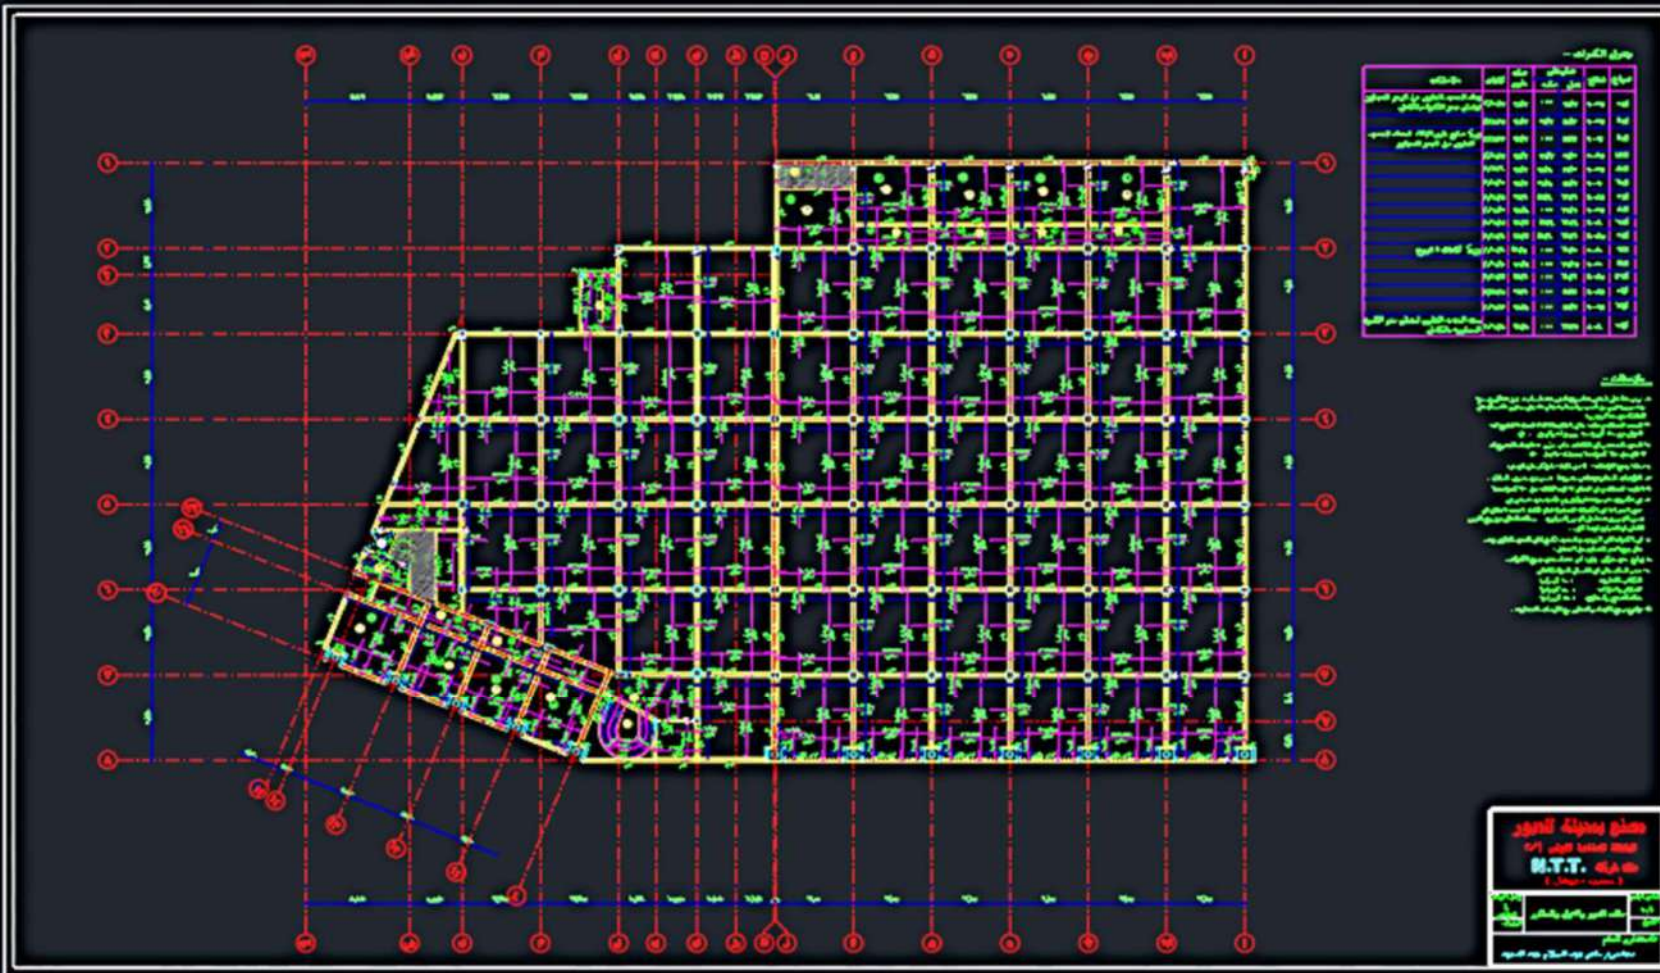

Polyline لمحيط اللوحة ومحيط الكمرات التي يختلف سمكها عن ٠,١٦ ومحيط السلم والفتحات في لوحة Solid Slab ؟؟؟



Notes:

1. THE COPYRIGHT OF THIS DRAWING IS VESTED IN YOURSPREADSHEETS AND IF ANY NOT BE REPRODUCED IN WHOLE OR IN PART OR USED FOR THE MANUFACTURE OF ANY ARTICLE WITHOUT THE EXPRESS PERMISSION OF THE COPYRIGHT HOLDERS.

2. WORK TO FIGURED DIMENSIONS ONLY.

Key plane

Before

Instructor :

YourSpreadsheets

Address line 1
Address line 2
Telephone line 1
Fax line 1
www.YourSpreadsheets.co.uk




CLIENT: BAH CLIENT
3 Mossadeh, Ad Doui, Dokki,
Giza Governorate, Giza,
Egypt

ARCHITECT: Amr Mamdoh
40 Mossadeh, Ad Doui, Dokki,
Giza Governorate, Giza,
Egypt

SITE: 31 ROVER ROAD
BLOCK A AND B

TITLE: RC DETAILS AND SECTIONS
OF GROUND BEAMS

SCALE AT A2: 1:50, 1:100	DATE: 05/09/13	DRAWN: DJ	CHECKED: DJ
PROJECT NO: 24567	DRAWING NO: A2/248	REVISION: C	

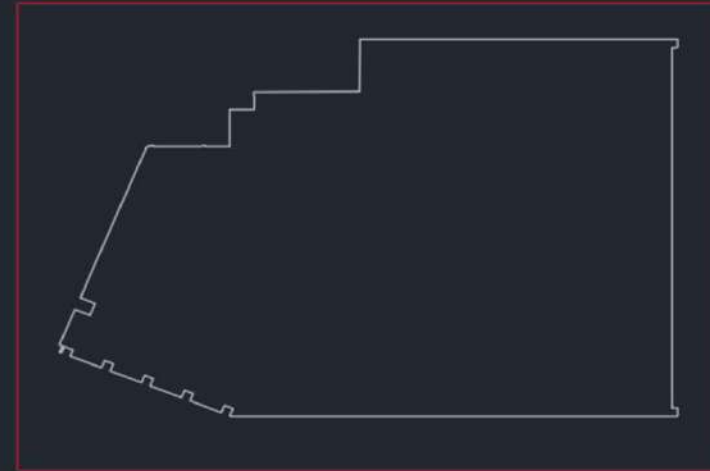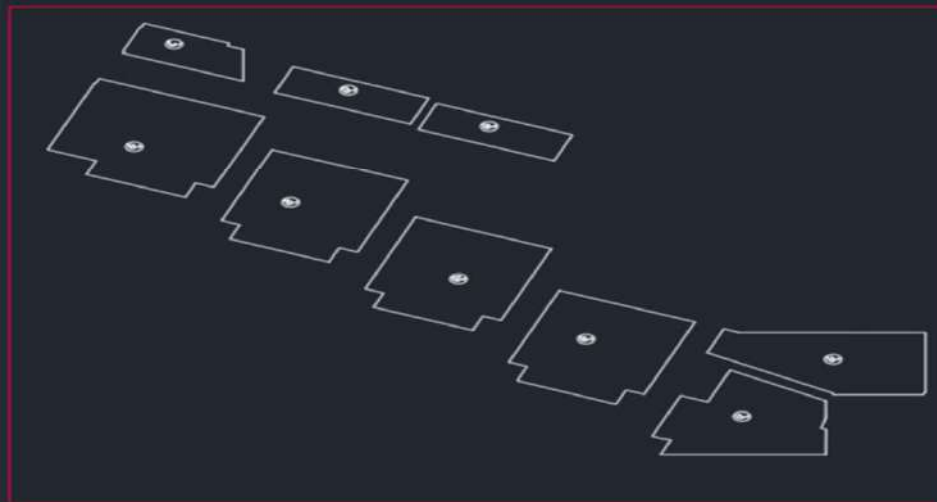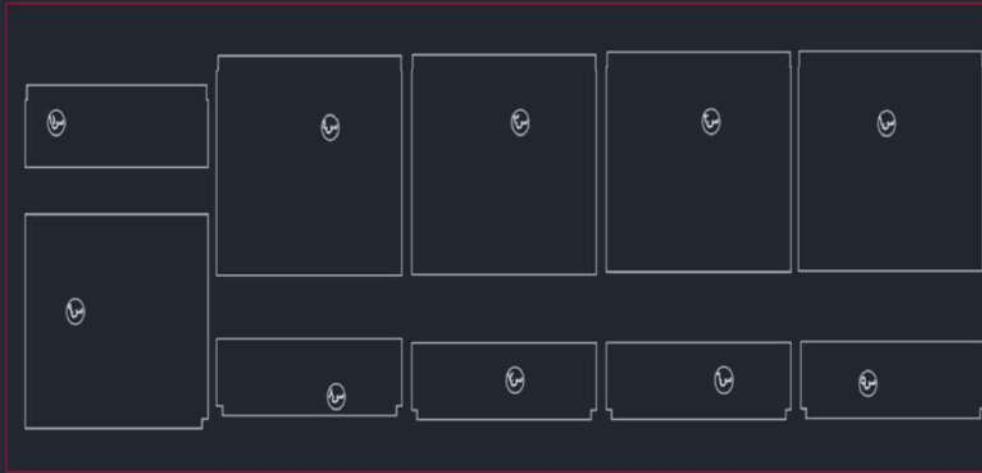

الحصر الهندسي لخرسانتة سقف Flat Slab ؟؟؟



Notes:

1. THE COPYRIGHT OF THIS DRAWING IS VESTED IN YOURSPREADSHEETS AND IT MAY NOT BE REPRODUCED IN WHOLE OR IN PART OR USED FOR THE MANUFACTURE OF ANY ARTICLE WITHOUT THE EXPRESS PERMISSION OF THE COPYRIGHT HOLDER.

2. WORK TO REQUIRED DIMENSIONS ONLY.

Key plane

Before

Instructor :

YourSpreadsheets

Address line 1
Address line 2
Telephone line 1
Fax line 1
www.YourSpreadsheets.co.uk

CLIENT: BAH i CUENT
3 Mossadeh, Ad Doui, Dokki,
Giza Governorate, Giza,
Egypt

ARCHITECT: Amr Mamdoh
40 Mossadeh, Ad Doui, Dokki,
Giza Governorate, Giza,
Egypt

SITE: 31 ROVER ROAD
BLOCK A AND B

TITLE: RC DETAILS AND SECTIONS
OF GROUND BEAMS

SCALE AT A2: 1:50, 1:100	DATE: 05/09/13	DRAWN: DJ	CHECKED: DJ
PROJECT NO: 24567	DRAWING NO: A2/248	REVISION: C	

رقم البند	نوع الأعمال و التوريدات	وحدة القياس	عدد	مقاسات الإضافة		إجمالي المكعبات المضافة	مقاسات التقريلات		إجمالي التقريلات	إجمالي بعد التقريلات	ملاحظات
				المسطح	المكب		المسطح	المكب			
	البند: بالمتر المكعب حصر خرسانة سقف Flat slab على ملف Flat slab										
	البلاطات	م ^٢		٣٥٢,٠٤٥	١٦,٢	٥٧٠٣,١٣٢				٥٧٠٣,١٣٢	
	المسلم	م ^٢					١٣,٨١١	١٢,٧٣٠	١٧٥,٨٠٩	١٧٥,٨٠٩	
	الفتحات	م ^٢						٤,٥٦٩	١٥,٠٤٠	٦٨,٧١٥	
						٥٧٠٣,١٣٢		٠,٠٠	٢٤٤,٥٢	٥٤٥٨,٦٠٩	
	إجمالي البند: بالمتر المكعب حصر خرسانة سقف Flat slab على ملف Flat slab فقط خمسة ألف و أربعمائة و ثمانية و خمسون و (١٠٠٠/٦٠٩) لاغير										
إجمالي كمية خرسانة سقف Flat Slab على ملف Flat Slab م ^٢						٥٤٥٨,٦٠٩					

الحصر الهندسي لكمرات سقف Flat Slab ؟؟؟



Notes:

1. THE COPYRIGHT OF THIS DRAWING IS VESTED IN YOURSPOONSHEETS AND IT MAY NOT BE REPRODUCED IN WHOLE OR PART OR USED FOR THE MANUFACTURE OF ANY ARTICLE WITHOUT THE EXPRESS PERMISSION OF THE COPYRIGHT HOLDERS.

2. WORK TO REQUIRED DIMENSIONS ONLY.

Key plane

Before

Instructor :

YourSpreadsheets
Address line 1
Address line 2
Telephone line 1
Fax line 1
www.YourSpreadsheets.co.uk

CLIENT: **BAH i CLIENT**
3 Mossadak, Ad Doqi, Dokki,
Giza Governorate, Giza,

ARCHITECT: Amr Mamdoh
40 Mussedah, Ad Dugl, Duhki,
Giza Governorate, Giza,
Egypt

31 ROVER ROAD
BLOCK A AND B

TITLE RC DETAILS AND SECTIONS
OF GROUND BEAMS

SCALE AT A2: 1:50, 1:100	DATE: 05/09/13	DRAWN: DJ	CHECKED: DJ
PROJECT NO: 24567	DRAWING NO: A2/248	REVISION: C	

رقم البند	نوع الأعمال و التوريدات	وحدة القياس	عدد	مقاسات		الإجمالي	التنزيلات	إجمالي بعد التنزيلات	ملاحظات
				العرض	السمك				
	البند: بالمتر المكعب حصر كمرات سقف Flat slab على محاور x على ملف Flat slab								
	محور أ - أ	م ^٢		٠,١٢٠	٠,٥٤	٠,٢٥١	٠,٠٠٠	٠,٢٥١	
	محور ب - ب	م ^٢		٠,١٢٠	٠,٥٤	٠,٢٥١	٠,٠٠٠	٠,٢٥١	
						٠,٥٠٣	٠,٠٠٠	٠,٥٠٣	
	إجمالي البند: بالمتر المكعب حصر كمرات سقف Flat slab على محاور x على ملف Flat slab فقط و (١٠٠٠/٥٠٣) لاغير								
اجمالي كمية حصر كمرات سقف Flat slab على محاور x على ملف Flat slab ٢م						٠,٥٠٣			

Arvil Group
CONSTRUCTION & TRAINING COMPANY

1. THE COPYRIGHT OF THIS DRAWING IS VESTED IN YOURS PROCEEDINGS AND IT MAY NOT BE REPRODUCED IN WHOLE OR PART OR USED FOR THE MANUFACTURE OF ANY ARTICLE WITHOUT THE EXPRESS PERMISSION OF THE COPYRIGHT HOLDERS.

Before

YourSpreadsheets

Address line 1
Address line 2
Telephone line 1
Fax line 1
www.YourSpreadsheets.co.uk

CLIENT: **BAH i CLIENT**
3 Mossadak, Ad Doqi, Dokki,
Giza Governorate, Giza,

ARCHITECT: Amr Mamdoh
40 Mussadah, Ad Doui, Duhhi,
Giza Governorate, Giza,
Egypt


SITE: 31 ROVER ROAD
BLOCK A AND B

TITLE: RC DETAILS AND SECTIONS
OF GROUND BEAMS

SCALE AT A2: 1:50, 1:100	DATE: 05/09/13	DRAWN: DJ	CHECKED: DJ
PROJECT NO: 24567	DRAWING NO: A2/248	REVISION: C	

رقم البند	نوع الأعمال و التوريدات	وحدة القياس	عدد	مقاسات		الإجمالي	التنزيلات	إجمالي بعد التنزيلات	ملاحظات
				العرض	السمك				
	البند: بالمتر المكعب حصر كميات سقف Flat slab على محاور y على ملف Flat slab								
	محور ١ - ١	م ^٢		٠,١٢٠	٠,٥٤	١,٠٣٠	٠,٠٠٠	١,٠٣٠	
	محور ٢ - ٢	م ^٢		٠,٢٥٠	٠,٥٤	١,٨٦٢	٠,٠٠٠	١,٨٦٢	
	بين محور ١ - ١ ومحور ٢ - ٢	م ^٢		٠,٢٥٠	٠,٥٤	٠,٨٤٥	٠,٠٠٠	٠,٨٤٥	
					٣,٧٣٧	٠,٠٠٠	٣,٧٣٧		
	اجمالي البند: بالمتر المكعب حصر كميات سقف Flat slab على محاور y على ملف Flat slab فقط ثلاثة (٧٣٧ / ١٠٠٠) لا غير								
					اجمالي كمية حصر كميات سقف Flat slab على محاور y على ملف Flat slab م ^٢				
					٣,٧٣٧				
					اجمالي كمية حصر كميات سقف Flat slab على جميع المحاور على ملف Flat slab م ^٢				
					٤,٢٤٠				
					اجمالي كمية خرسانة بلاطة Solid slab م ^٣				
					٥٤٦٢,٨٤٨				

اللوحة الهندسية Flat slab

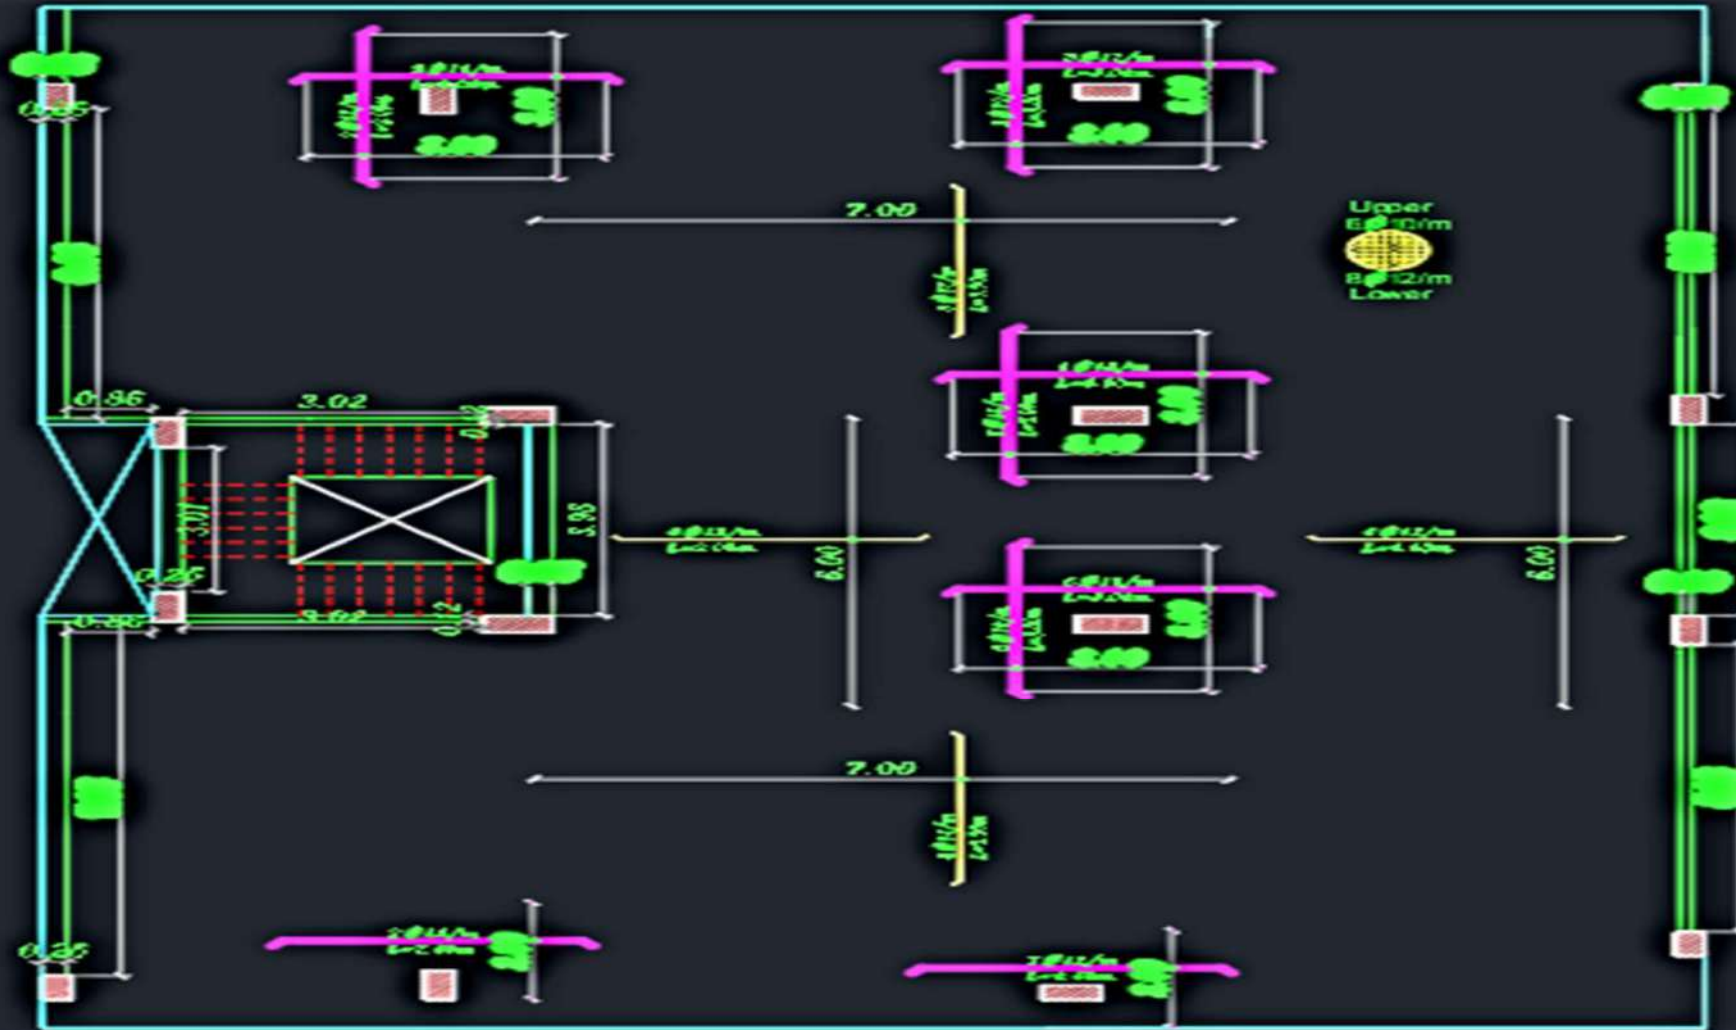

Notes:

1. THE COPYRIGHT OF THIS DRAWING IS VESTED IN YOURSPREADSHEETS AND IF ANY NOT BE REPRODUCED IN WHOLE OR IN PART OR USED FOR THE MANUFACTURE OF ANY ARTICLE WITHOUT THE EXPERT PERMISSION OF THE COPYRIGHT HOLDERS.

2. WORK TO REQUIRED DIMENSIONS ONLY.

Key plane

Before

Instructor :

YourSpreadsheets

Address line 1
Address line 2
Telephone line 1
Fax line 1
www.YourSpreadsheets.co.uk

CLIENT: BAHİ CLIENT
3 Mossadeh, Ad Doui, Dokki,
Giza Governorate, Giza,
Egypt


ARCHITECT: Amr Mamdoh
40 Mossadeh, Ad Doui, Dokki,
Giza Governorate, Giza,
Egypt

SITE: 31 ROVER ROAD
BLOCK A AND B

TITLE: RC DETAILS AND SECTIONS
OF GROUND BEAMS

SCALE AT A2: 1:50: 1:100	DATE: 05/09/13	DRAWN: DJ	CHECKED: DJ
PROJECT NO: 24567	DRAWING NO: A2/248	REVISION: C	

Polyline لمحيط اللوحة ومحيط السلم والفتحات في لوحة Flat Slab ؟؟؟

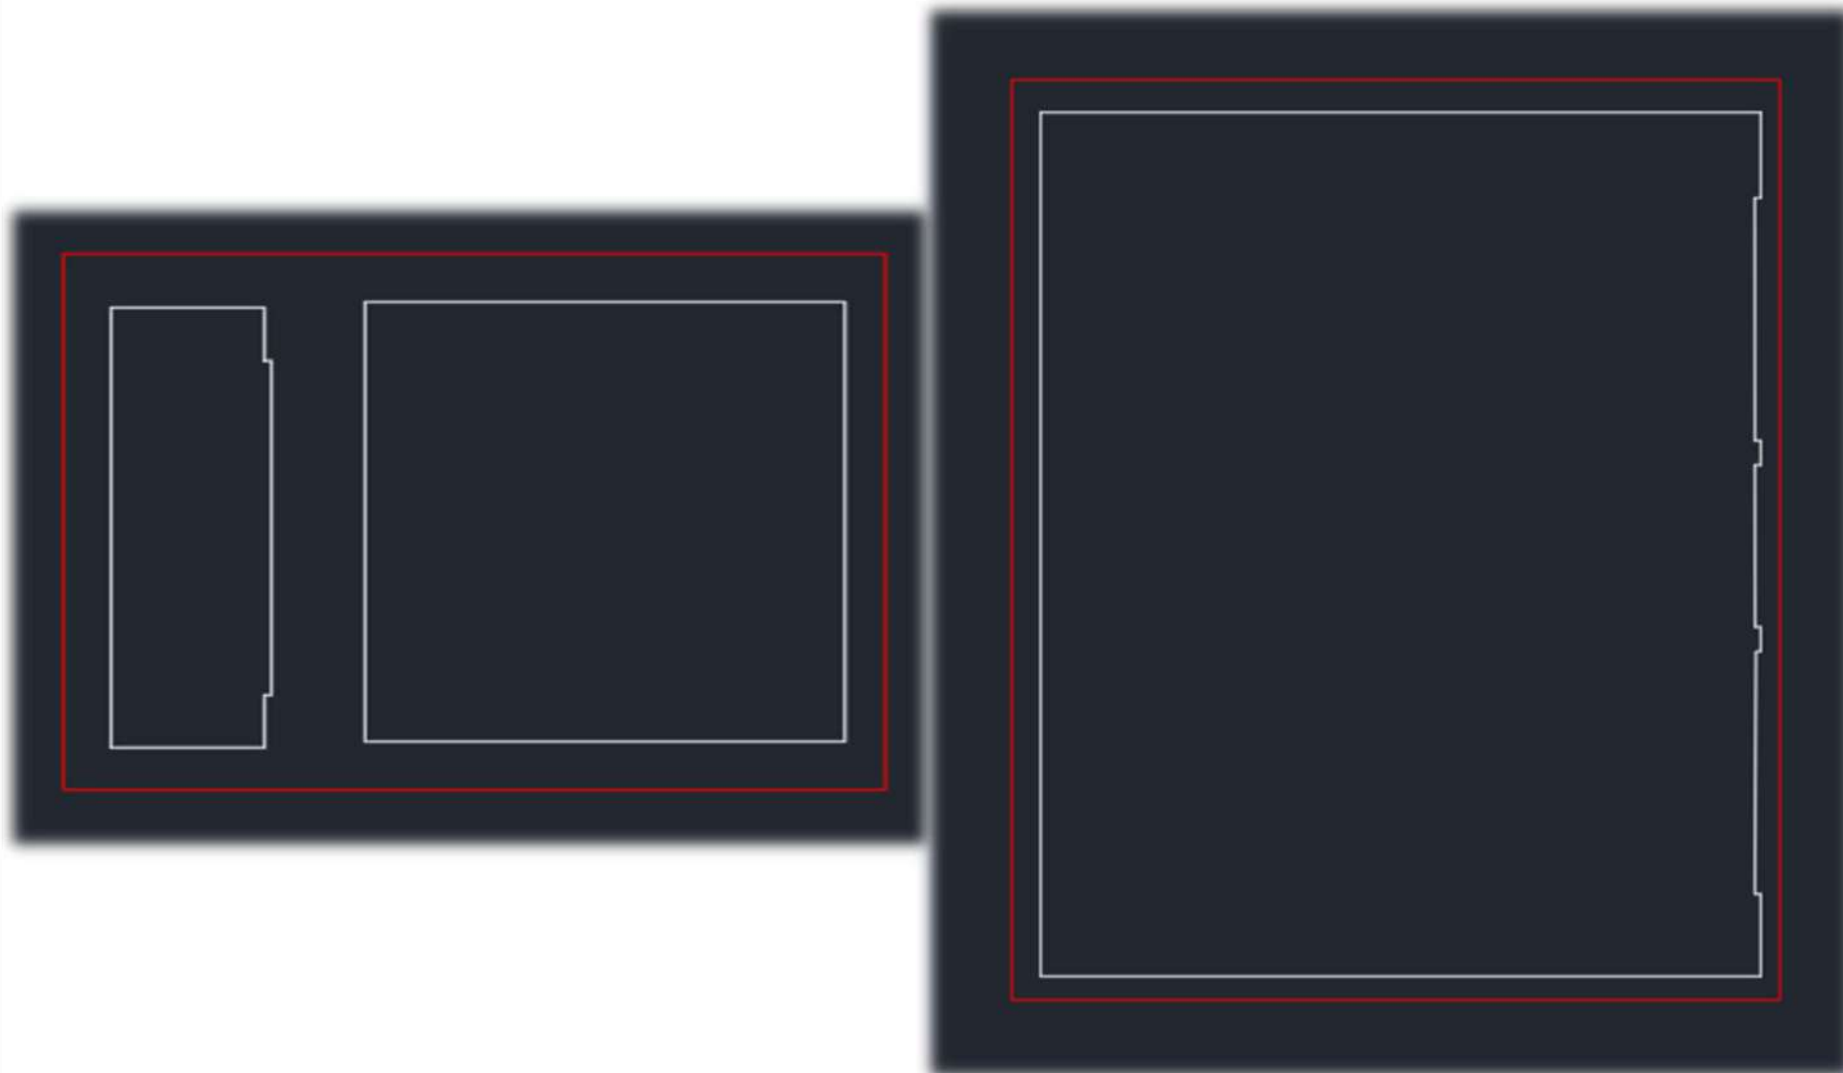

Notes:

1. THE COPYRIGHT OF THIS DRAWING IS VESTED IN YOURSPREADSHEETS AND IF ANY NOT BE REPRODUCED IN WHOLE OR IN PART OR USED FOR THE MANUFACTURE OF ANY ARTICLE WITHOUT THE EXPRESS PERMISSION OF THE COPYRIGHT HOLDER.

2. WORK TO FIGURED DIMENSIONS ONLY.

Key plane

Before

Instructor :

YourSpreadsheets

Address line 1
Address line 2
Telephone line 1
Fax line 1
www.YourSpreadsheets.co.uk


CLIENT: BAHi CLIENT
3 Mossadeh, Ad Doui, Dokki,
Giza Governorate, Giza,
Egypt

ARCHITECT: Amr Mamdoh
40 Mossadeh, Ad Doui, Dokki,
Giza Governorate, Giza,
Egypt

SITE: 31 ROVER ROAD
BLOCK A AND B

TITLE: RC DETAILS AND SECTIONS
OF GROUND BEAMS

SCALE AT A2: 1:50, 1:100	DATE: 05/09/13	DRAWN: DJ	CHECKED: DJ
PROJECT NO: 24567	DRAWING NO: A2/248	REVISION: C	

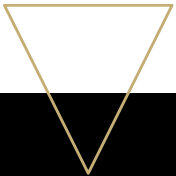

Thank You




Email

em3875050@email.com



Phone

+201012162395

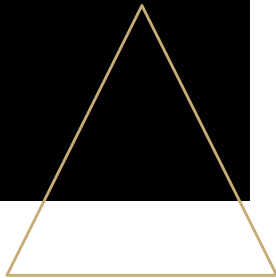

Course: Technical Office G46

NAME: IBRAHIM MOHAMED READ

ENG: AMR MAMDOUH

LECTURE: 8

TASK: 6



Arvil Group
CONSTRUCTION & TRAINING COMPANY

Before

SCALE AT A2: 1:50, 1:100	DATE: 05/09/13	DRAWN: DJ	CHECKED:
PROJECT NO: 24567	DRAWING NO: A2/248	REVISION:	

الحصر الهندسي لخرسانة بلاطة Hollow Block ؟؟

رقم البند	نوع الأعمال و التوريدات	وحدة القياس	عدد	مقاسات			الإضافه	التنزيلات	إجمالي بعد التنزيلات	ملاحظات
				الطول	العرض	السمك				
	البند: بالمتر المكعب حصر كمرات بلاطة Hollow Block على محور x على ملف Hollow Block									
	محور ١ - ١	م ^٣		١٦,٤٩٠	٠,٢٥٠	٠,٢٩٠	١,١٩٦	٠,٠٠٠	١,١٩٦	
	محور ٢ - ٢	م ^٣		١٥,٣٩٠	٠,٢٥٠	٠,٢٩٠	١,١١٦	٠,٠٠٠	١,١١٦	
	كمرات السلم والفتحات	م ^٣		١١,١٨٠	٠,١٢٠	٠,٢٩٠	٠,٣٨٩	٠,٠٠٠	٠,٣٨٩	
							٢,٧٠٠	٠,٠٠٠	٢,٧٠٠	
	اجمالي البند: بالمتر المكعب حصر كمرات بلاطة Hollow Block على محور x على ملف Hollow Block فقط اثنان و (١٠٠٠/٧٠٠) لاغير									
	اجمالي حصر كمرات بلاطة Hollow Block على محور x على ملف Hollow Block ٣م			٢,٧٠٠						

رقم البند	نوع الأعمال و التوريدات	وحدة القياس	عدد	مقاسات			الإضافه	التنزيلات	إجمالي بعد التنزيلات	ملاحظات
				الطول	العرض	السمك				
	البند: بالمتر المكعب حصر كمرات بلاطة Hollow Block على محور y على ملف Hollow Block									
	محور أ - أ	م ^٣		١٨,٨٥٠	٠,٢٥٠	٠,٢٩٠	١,٣٦٧	٠,٠٠٠	١,٣٦٧	
	محور ب - ب	م ^٣		١٩,١٤٠	٠,٢٥٠	٠,٢٩٠	١,٣٨٨	٠,٠٠٠	١,٣٨٨	
	كمرات السلم والفتحات	م ^٣		٩,٢٥٠	٠,١٢٠	٠,٢٩٠	٠,٣٢٢	٠,٠٠٠	٠,٣٢٢	
							٣,٠٧٦	٠,٠٠٠	٣,٠٧٦	
	إجمالي البند: بالمتر المكعب حصر كمرات بلاطة Hollow Block على محور y على ملف Hollow Block فقط ثلاثة و (١٠٠٠/٧٦) لاغير									
	إجمالي حصر كمرات بلاطة Hollow Block على محور y على ملف Hollow Block ٣م			٣,٠٧٦						

	اجمالي حصر خرسانة سقف Hollow Block على ملف Hollow Block ٣م			٨٥,١٤٥						
--	--	--	--	--------	--	--	--	--	--	--



Notes:

1. THE COPYRIGHT OF THIS DRAWING IS VESTED IN YOURSPREADSHEETS AND IF ANY NOT BE REPRODUCED IN WHOLE OR IN PART OR USED FOR THE MANUFACTURE OF ANY ARTICLE WITHOUT THE EXPRESS PERMISSION OF THE COPYRIGHT HOLDER.

2. WORK TO REQUIRED DIMENSIONS ONLY.

Key plane

Before

Instructor :

YourSpreadsheets

Address line 1
Address line 2
Telephone line 1
Fax line 1
www.YourSpreadsheets.co.uk

CLIENT: BAH & CLIENT
3 Mossadeh, Ad Doui, Dokki,
Giza Governorate, Giza,
Egypt


ARCHITECT: Amr Marmoh
40 Mossadeh, Ad Doui, Dokki,
Giza Governorate, Giza,
Egypt

SITE: 31 ROVER ROAD
BLOCK A AND B

TITLE: RC DETAILS AND SECTIONS
OF GROUND BEAMS

SCALE AT A2: 1:50, 1:100	DATE: 05/09/13	DRAWN: DJ	CHECKED: DJ
PROJECT NO: 24567	DRAWING NO: A2/248	REVISION: C	

اللوحة الهندسية Hollow Block

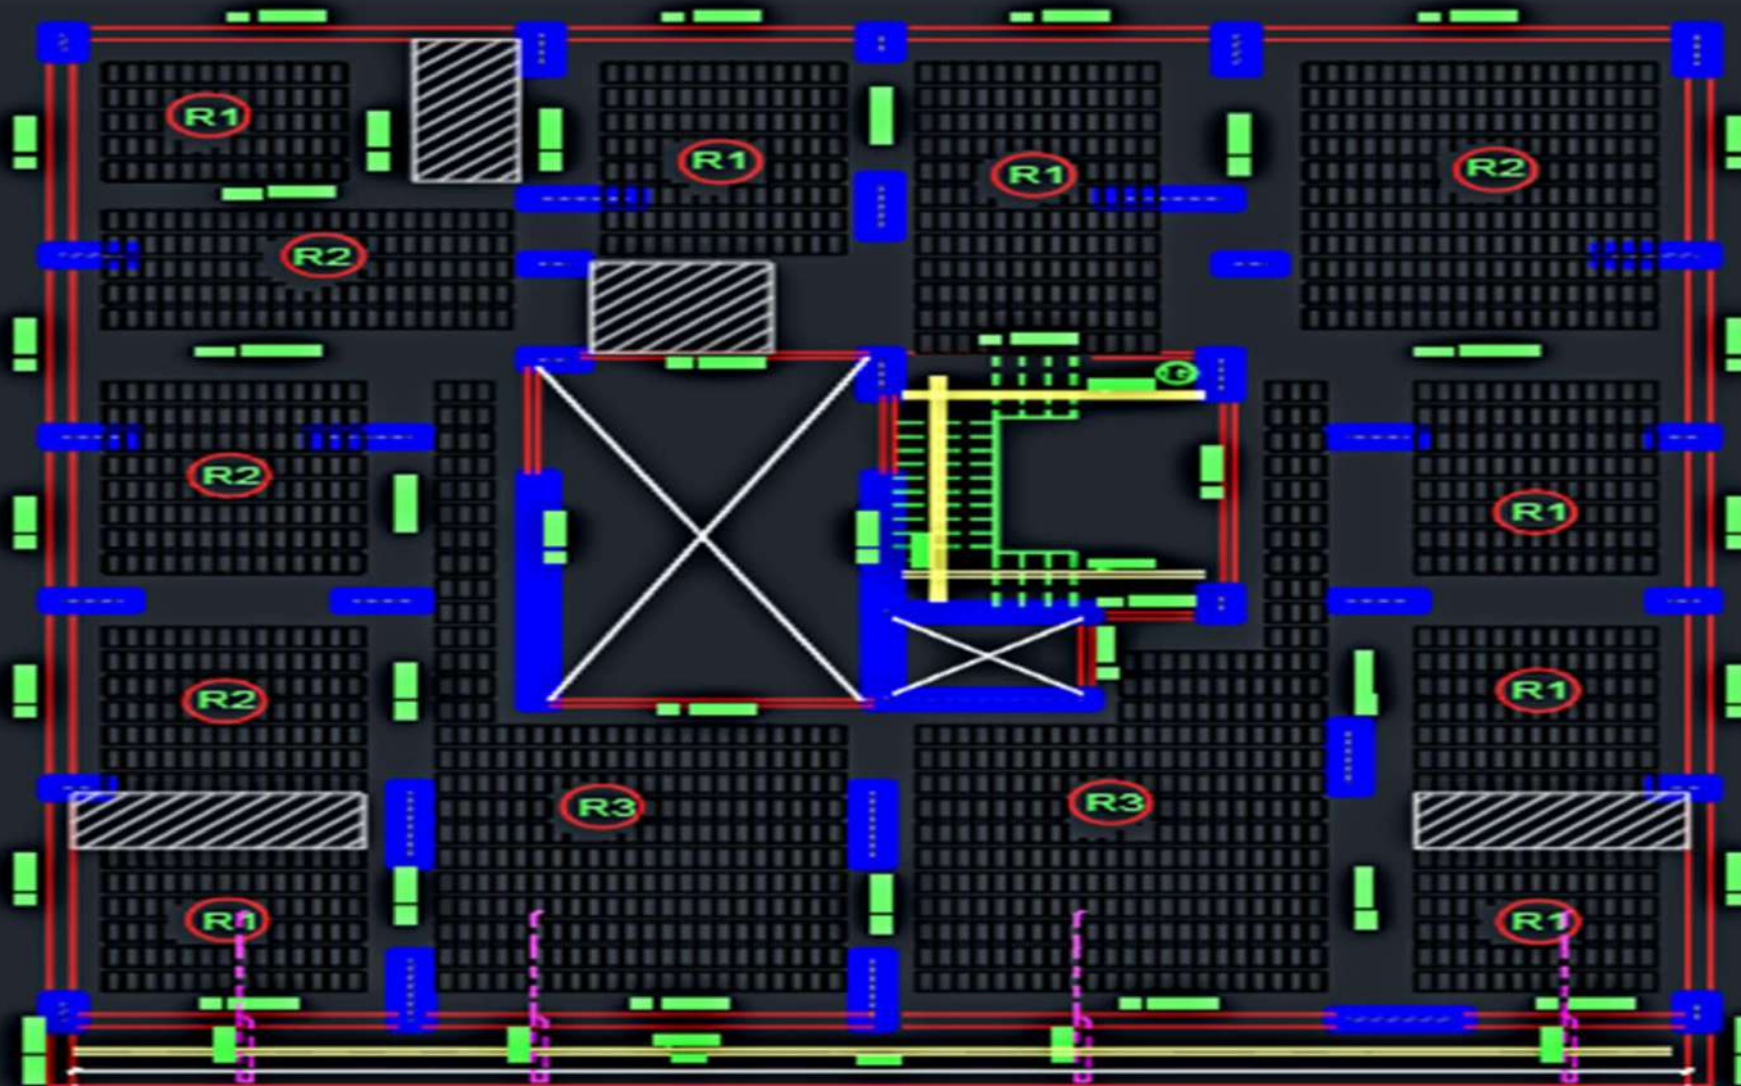

Notes:

1. THE COPYRIGHT OF THIS DRAWING IS VESTED IN YOURSPREADSHEETS AND IF ANY NOT BE REPRODUCED IN WHOLE OR IN PART OR USED FOR THE MANUFACTURE OF ANY ARTICLE WITHOUT THE EXPRESS PERMISSION OF THE COPYRIGHT HOLDER.

2. WORK TO FIGURED DIMENSIONS ONLY.

Key plane

Before

Instructor :

YourSpreadsheets

Address line 1
Address line 2
Telephone line 1
Fax line 1
www.YourSpreadsheets.co.uk

CLIENT: BAHİ CLIENT
3 Mossadeh, Ad Dami, Dokki,
Giza Governorate, Giza,
Egypt


ARCHITECT: Amr Mamdouh
40 Mossadeh, Ad Dami, Dokki,
Giza Governorate, Giza,
Egypt

SITE: 31 ROVER ROAD
BLOCK A AND B

TITLE: RC DETAILS AND SECTIONS
OF GROUND BEAMS

SCALE AT A2: 1:50, 1:100	DATE: 05/09/13	DRAWN: DJ	CHECKED: DJ
PROJECT NO: 24567	DRAWING NO: A2/248	REVISION: C	

Polyline لمحيط اللوحة ومحيط السلم والفتحات والكمرات الهابطة في لوحة Hollow Block ؟؟؟

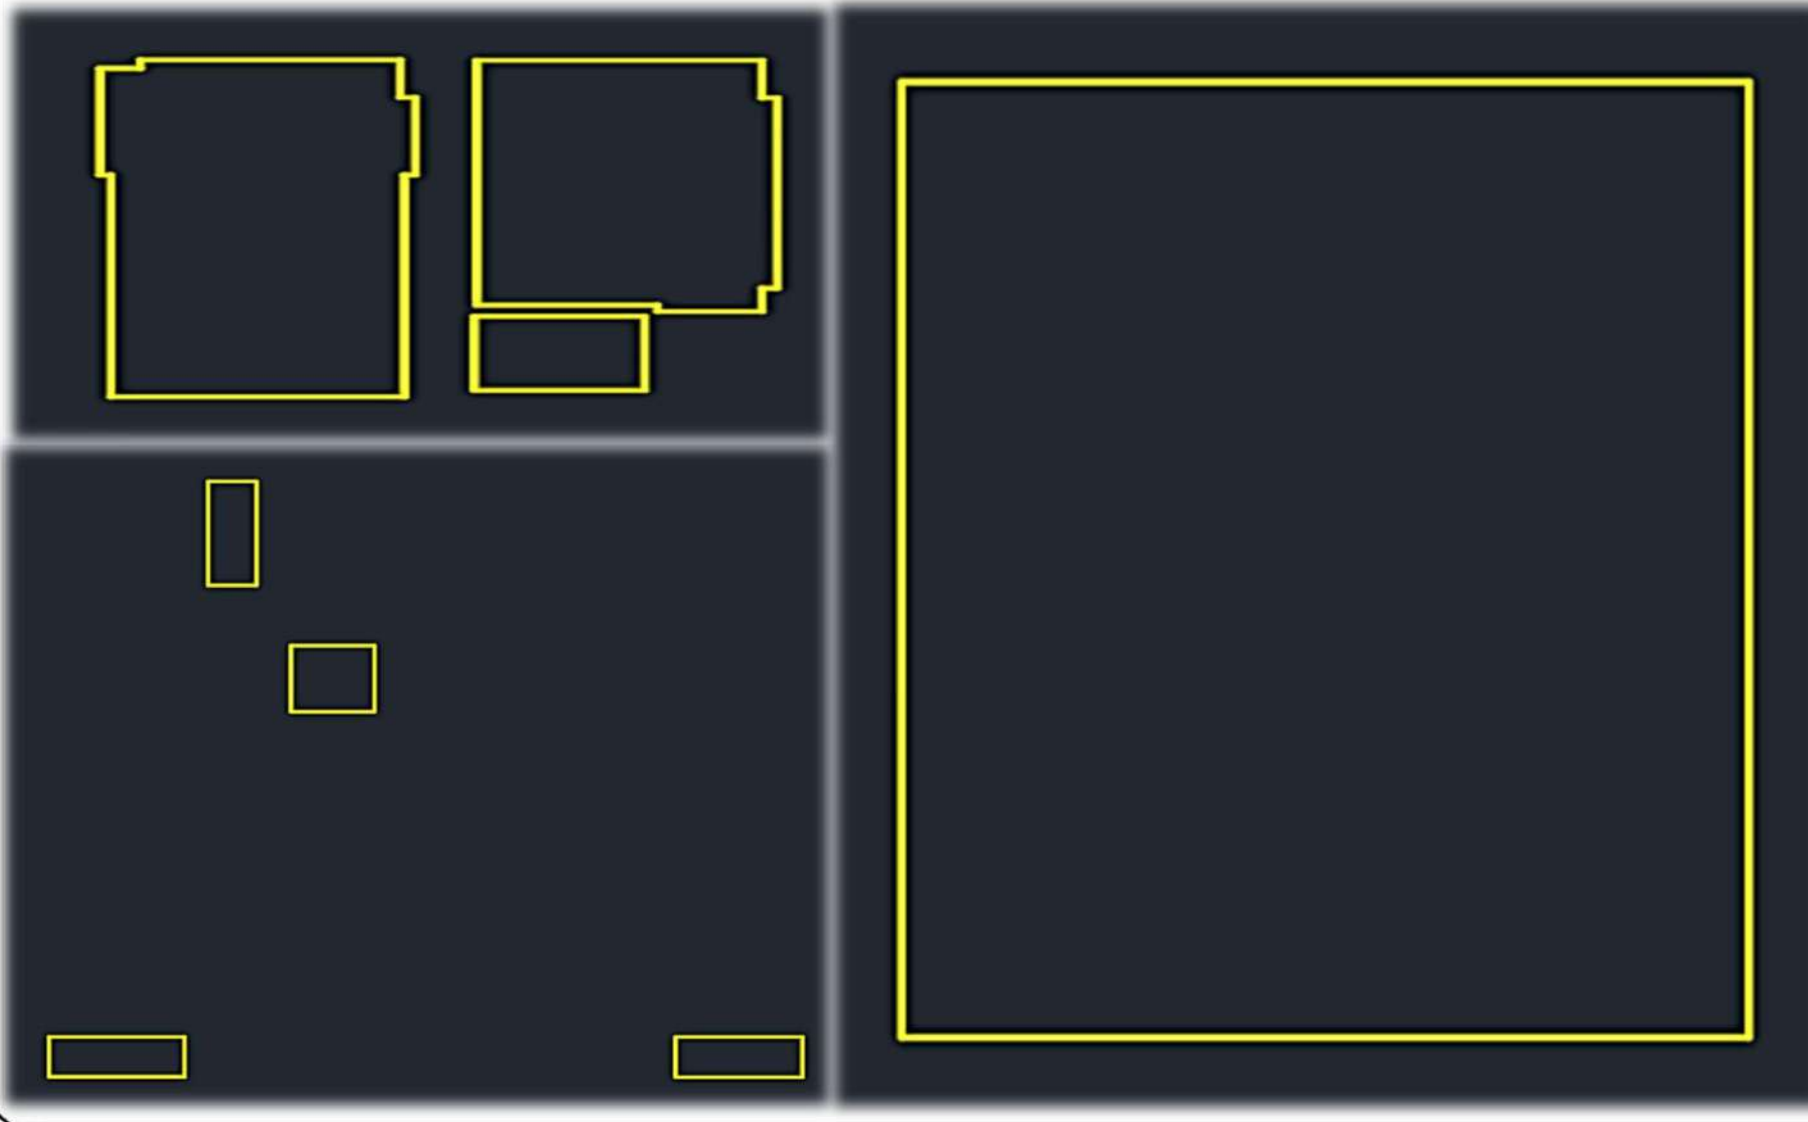

Notes:

1. THE COPYRIGHT OF THIS DRAWING IS VESTED IN YOURSPREADSHEETS AND IT MAY NOT BE REPRODUCED IN WHOLE OR IN PART OR USED FOR THE MANUFACTURE OF ANY ARTICLE WITHOUT THE EXPRESS PERMISSION OF THE COPYRIGHT HOLDERS.

2. WORK TO FIGURED DIMENSIONS ONLY.

Key plane

Before

Instructor :

YourSpreadsheets

Address line 1
Address line 2
Telephone line 1
Fax line 1
www.YourSpreadsheets.co.uk

CLIENT: BAH i CLIENT
3 Mossadeh, Ad Doui, Dokki,
Giza Governorate, Giza,
Egypt

ARCHITECT: Amr Mamdoh
40 Mossadeh, Ad Doui, Dokki,
Giza Governorate, Giza,
Egypt

SITE: 31 ROVER ROAD
BLOCK A AND B

TITLE: RC DETAILS AND SECTIONS
OF GROUND BEAMS

SCALE AT A2: 1:50, 1:100	DATE: 05/09/13	DRAWN: DJ	CHECKED: DJ
PROJECT NO: 24567	DRAWING NO: A2/248	REVISION: C	

الحصر الهندسي لخرسانة الدكة والميول؟؟



Notes:

1. THE COPYRIGHT OF THIS DRAWING IS VESTED IN YOURSPREADSHEETS AND IF ANY NOT BE REPRODUCED IN WHOLE OR IN PART OR USED FOR THE MANUFACTURE OF ANY ARTICLE WITHOUT THE EXPRESS PERMISSION OF THE COPYRIGHT HOLDER.

2. WORK TO REQUIRED DIMENSIONS ONLY.

Key plane

Before

رقم البند	نوع الأعمال و التوريدات	وحدة القياس	عدد	مقاسات		الإضافه	التنزيلات	إجمالي بعد التنزيلات	ملاحظات
				الطول	العرض				
	البند: بالمتر المسطح حصر خرسانة الدكة الأرضية S.O.G على ملف (معماري + انشائي)								
	حصر خرسانة الدكة الأرضية	م ^٢		٨٦,٥١٣		٨٦,٥١٣		٨٦,٥١٣	
	تخصيم الأعمده التي في المنتصف	م ^٢		٠,٤٥٠			٠,٤٥٠	٠,٤٥٠	
				٨٦,٥١٣		٨٦,٥١٣	٠,٤٥	٨٦,٠٦٣	
	اجمالي البند: بالمتر المسطح حصر خرسانة الدكة الأرضية S.O.G على ملف (معماري + انشائي) فقط سنة و ثمانون و (١٠٠٠/٦٣) لاغير								
	اجمالي حصر خرسانة الدكة الأرضية S.O.G على ملف (معماري + انشائي) م ^٢								
	٨٦,٠٦٣								

رقم البند	نوع الأعمال و التوريدات	وحدة القياس	عدد	مقاسات		الإضافه	التنزيلات	إجمالي بعد التنزيلات	ملاحظات
				الطول	العرض				
	البند: بالمتر المسطح حصر خرسانة الميول على ملف (معماري + انشائي)								
	حصر خرسانة الميول	م ^٢		٨٥,٣٩٨		٨٥,٣٩٨		٨٥,٣٩٨	
	تخصيم الفتحات	م ^٢		٥,٤٧٤			٥,٤٧٤	٥,٤٧٤	
						٨٥,٣٩٨	٥,٤٧	٧٩,٩٢٤	
	اجمالي البند: بالمتر المسطح حصر خرسانة الميول على ملف (معماري + انشائي) فقط تسعة و سبعون و (١٠٠٠/٩٢٤) لاغير								
				اجمالي حصر خرسانة الدكة الأرضية S.O.G على ملف (معماري + انشائي) م ^٢					
				٧٩,٩٢٤					

Instructor :

YourSpreadsheets

Address line 1
Address line 2
Telephone line 1
Fax line 1
www.YourSpreadsheets.co.uk

CLIENT: BAH & CLIENT
3 Mossadeh, Ad Doui, Dokki,
Giza Governorate, Giza,
EGYPT


ARCHITECT: Amr Marmoh
40 Mossadeh, Ad Doui, Dokki,
Giza Governorate, Giza,
EGYPT

SITE: 31 ROVER ROAD
BLOCK A AND B

TITLE: RC DETAILS AND SECTIONS
OF GROUND BEAMS

SCALE AT A2: 1:50, 1:100	DATE: 05/09/13	DRAWN: DJ	CHECKED: DJ
PROJECT NO: 24567	DRAWING NO: A2/248	REVISION: C	

اللوحة الهندسية لحصر خرسانة الدكتر + تخصيص الأعمدة التي في المنتصف ؟؟؟

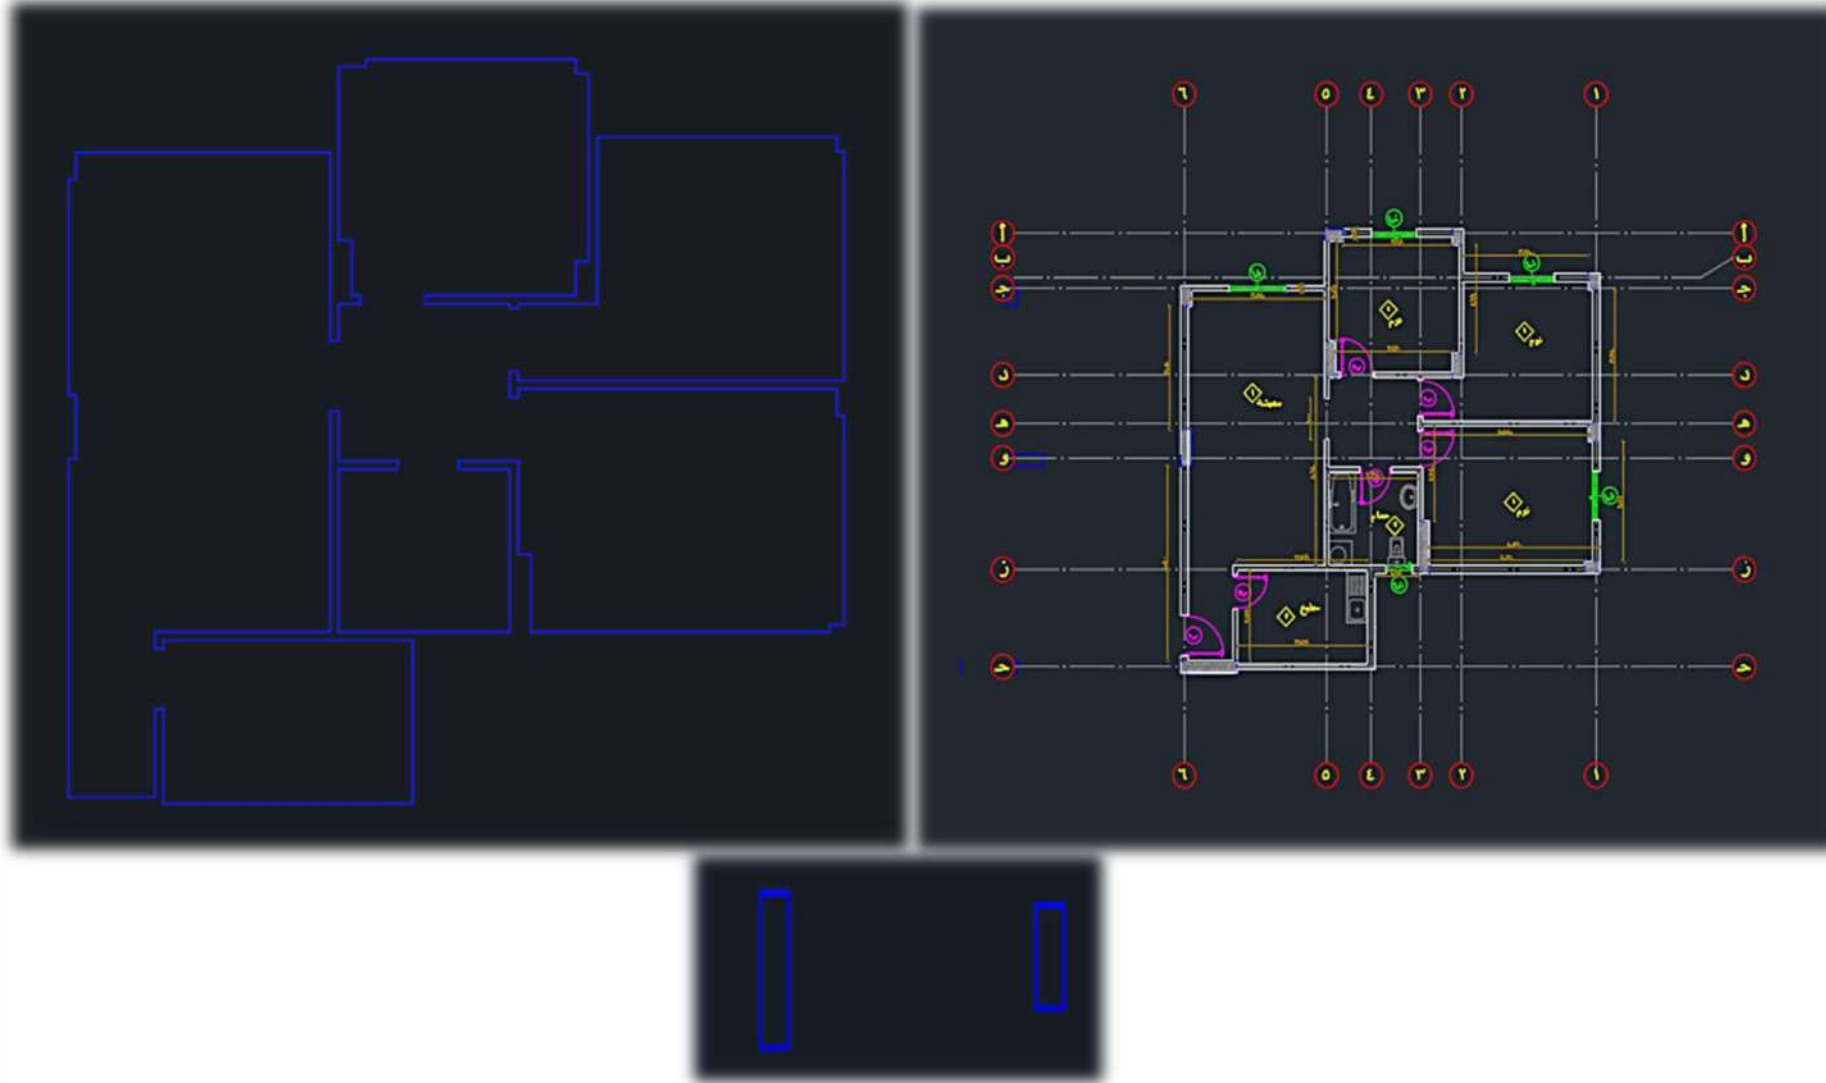

Notes:

1. THE COPYRIGHT OF THIS DRAWING IS VESTED IN YOURSPREADSHEETS AND IF ANY NOT BE REPRODUCED IN WHOLE OR IN PART OR USED FOR THE MANUFACTURE OF ANY ARTICLE WITHOUT THE EXPERT PERMISSION OF THE COPYRIGHT HOLDERS.

2. WORK TO REQUIRED DIMENSIONS ONLY.

Key plane

Before

Instructor :

YourSpreadsheets

Address line 1
Address line 2
Telephone line 1
Fax line 1
www.YourSpreadsheets.co.uk

CLIENT: BAHİ CLIENT
3 Mossadeh, Ad Dami, Dokki,
Giza Governorate, Giza,
Egypt




ARCHITECT: Amr Mamdoh
40 Mossadeh, Ad Dami, Dokki,
Giza Governorate, Giza,
Egypt

SITE: 31 ROVER ROAD
BLOCK A AND B

TITLE: RC DETAILS AND SECTIONS
OF GROUND BEAMS

SCALE AT A2: 1:50, 1:100	DATE: 05/09/13	DRAWN: DJ	CHECKED: DJ
PROJECT NO: 24567	DRAWING NO: A2/248	REVISION: C	

اللوحة الهندسية لحصر خرسانة الميول + تخصيص الفتحات

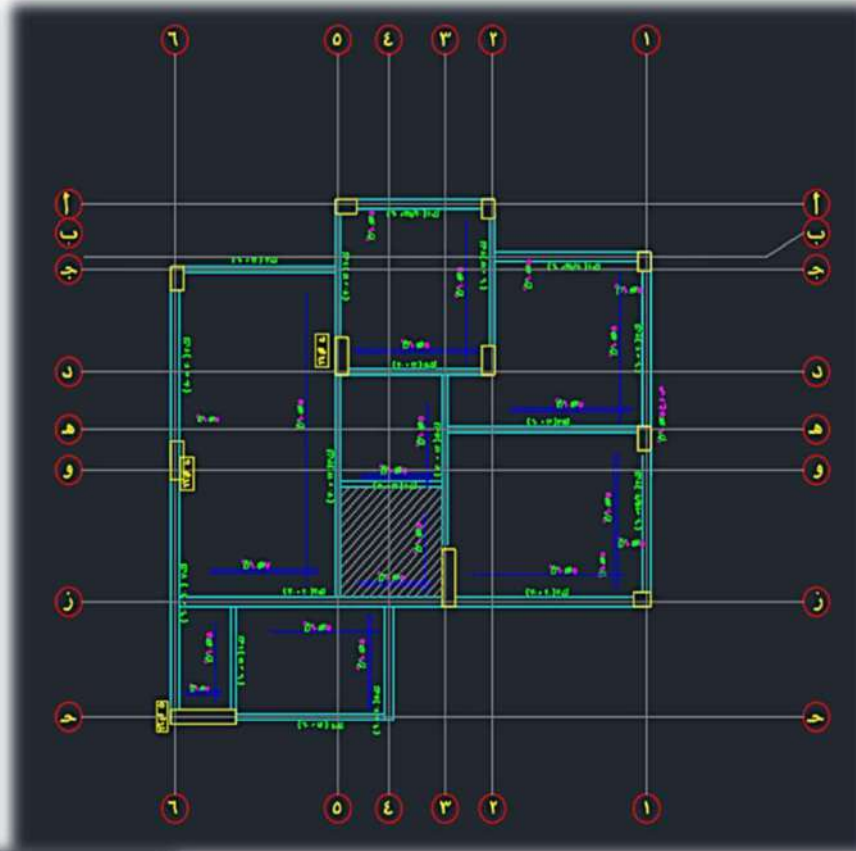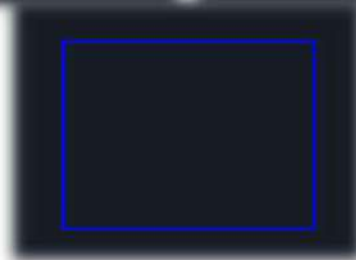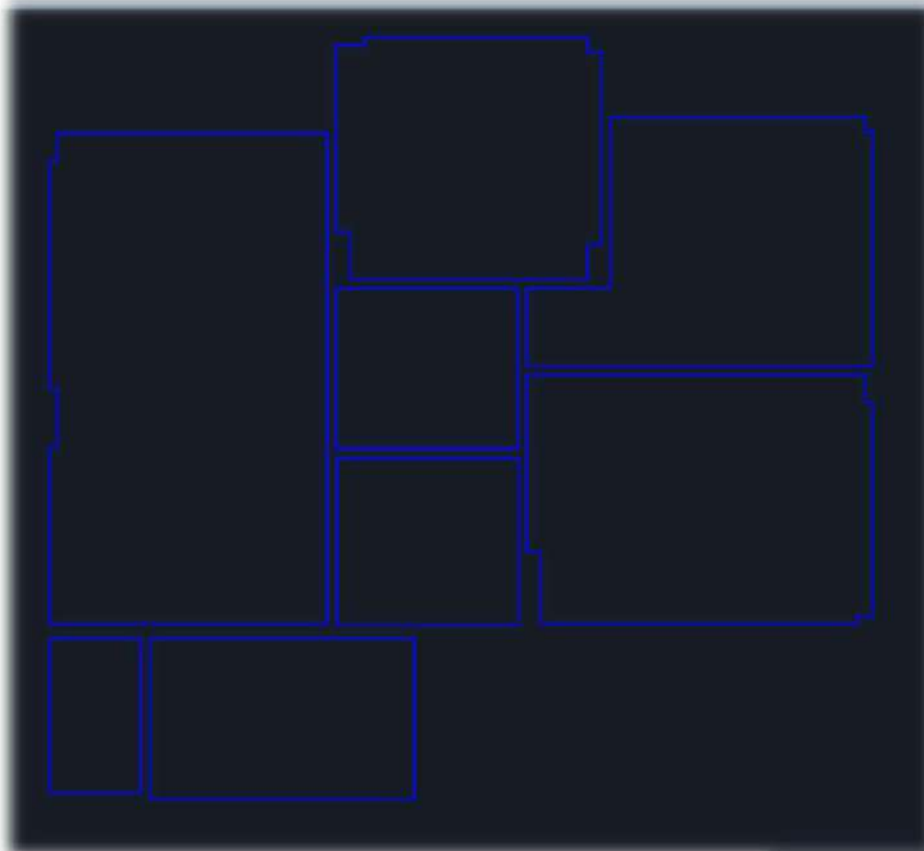

Notes:

1. THE COPYRIGHT OF THIS DRAWING IS VESTED IN YOURSPREADSHEETS AND IF ANY NOT BE REPRODUCED IN WHOLE OR IN PART OR USED FOR THE MANUFACTURE OF ANY ARTICLE WITHOUT THE EXPRESS PERMISSION OF THE COPYRIGHT HOLDERS.

2. WORK TO REQUIRED DIMENSIONS ONLY.

Key plane

Before

Instructor :

YourSpreadsheets

Address line 1
Address line 2
Telephone line 1
Fax line 1
www.YourSpreadsheets.co.uk

CLIENT: BAH + CLIENT
3 Mossadeh, Ad Dami, Dokki,
Giza Governorate, Giza,
Egypt

ARCHITECT: Amr Mamdouh
40 Mossadeh, Ad Dami, Dokki,
Giza Governorate, Giza,
Egypt

SITE: 31 ROVER ROAD
BLOCK A AND B

TITLE: RC DETAILS AND SECTIONS
OF GROUND BEAMS

SCALE AT A2: 1:50, 1:100	DATE: 05/09/13	DRAWN: DJ	CHECKED: DJ
PROJECT NO: 24567	DRAWING NO: A2/248	REVISION: C	

الحصر الهندسي للحوائط الخرسانية؟؟

رقم البند	نوع الأعمال و التوريدات	وحدة القياس	عدد	مقاسات			الإضافه	التنزيلات	إجمالي بعد التنزيلات	ملاحظات
				الطول	العرض	الارتفاع				
البند: بالمتر المكعب حصر الحوائط الخرسانية على ملف Car Shed										
	محور A - A	م ^٢		٥٧٠٠,٠٠٠	٠,٢٥٠	٤,٦٠٠	٦٥٥٥,٠٠٠	٠,٠٠٠	٦٥٥٥,٠٠٠	
	محور B - B	م ^٢		١٢٧٠٠,٠٠٠	٠,٢٥٠	٤,٦٠٠	١٤٦٠٥,٠٠٠	٠,٠٠٠	١٤٦٠٥,٠٠٠	
	محور C - C	م ^٢		١٨٤٠٠,٠٠٠	٠,٢٥٠	٤,٦٠٠	٢١١٦٠,٠٠٠	٠,٠٠٠	٢١١٦٠,٠٠٠	
	محور ١ - ١	م ^٢		٦٩٥٠,٠٠٠	٠,٢٥٠	٥,٤٥٠	٩٤٦٩,٣٧٥	٠,٠٠٠	٩٤٦٩,٣٧٥	
	محور ٢ - ٢	م ^٢		٦٩٥٠,٠٠٠	٠,٢٥٠	٤,٥٣٠	٧٨٧٠,٨٧٥	٠,٠٠٠	٧٨٧٠,٨٧٥	
	محور ٣ - ٣	م ^٢		٤٥٥٠,٠٠٠	٠,٢٥٠	٤,٥٣٠	٥١٥٢,٨٧٥	٠,٠٠٠	٥١٥٢,٨٧٥	
	محور ٤ - ٤	م ^٢		٤٥٥٠,٠٠٠	٠,٢٥٠	٤,٥٣٠	٥١٥٢,٨٧٥	٠,٠٠٠	٥١٥٢,٨٧٥	
	محور ٥ - ٥	م ^٢		٤٥٥٠,٠٠٠	٠,٢٥٠	٤,٥٣٠	٥١٥٢,٨٧٥	٠,٠٠٠	٥١٥٢,٨٧٥	
	٢١١٦٠,٠٠٠									
إجمالي البند: بالمتر المكعب حصر الحوائط الخرسانية على ملف Car Shed فقط واحد وعشرون ألف ومائة وستون و (١٠٠٠/٠) لاغير										
إجمالي حصر الحوائط الخرسانية على ملف Car Shed م ^٢										
٢١١٦٠,٠٠٠										



Notes:

1. THE COPYRIGHT OF THIS DRAWING IS VESTED IN YOURSPREADSHEETS AND IF ANY NOT BE REPRODUCED IN WHOLE OR IN PART OR USED FOR THE MANUFACTURE OF ANY ARTICLE WITHOUT THE EXPRESS PERMISSION OF THE COPYRIGHT HOLDERS.
2. WORK TO REQUIRED DIMENSIONS ONLY.

Key plane

Before

Instructor :

YourSpreadsheets

Address line 1
Address line 2
Telephone line 1
Fax line 1
www.YourSpreadsheets.co.uk

CLIENT: BAHİ CLIENT
3 Mossadeh, Ad Dami, Dokki,
Giza Governorate, Giza,
Egypt


ARCHITECT: Amr Mamdoh
40 Mossadeh, Ad Dami, Dokki,
Giza Governorate, Giza,
Egypt

SITE: 31 ROVER ROAD
BLOCK A AND B

TITLE: RC DETAILS AND SECTIONS
OF GROUND BEAMS

SCALE AT A2: 1:50, 1:100	DATE: 05/09/13	DRAWN: DJ	CHECKED: DJ
PROJECT NO: 24567	DRAWING NO: A2/248	REVISION: C	

اللوحة الهندسية للحوائط الخرسانية؟؟؟

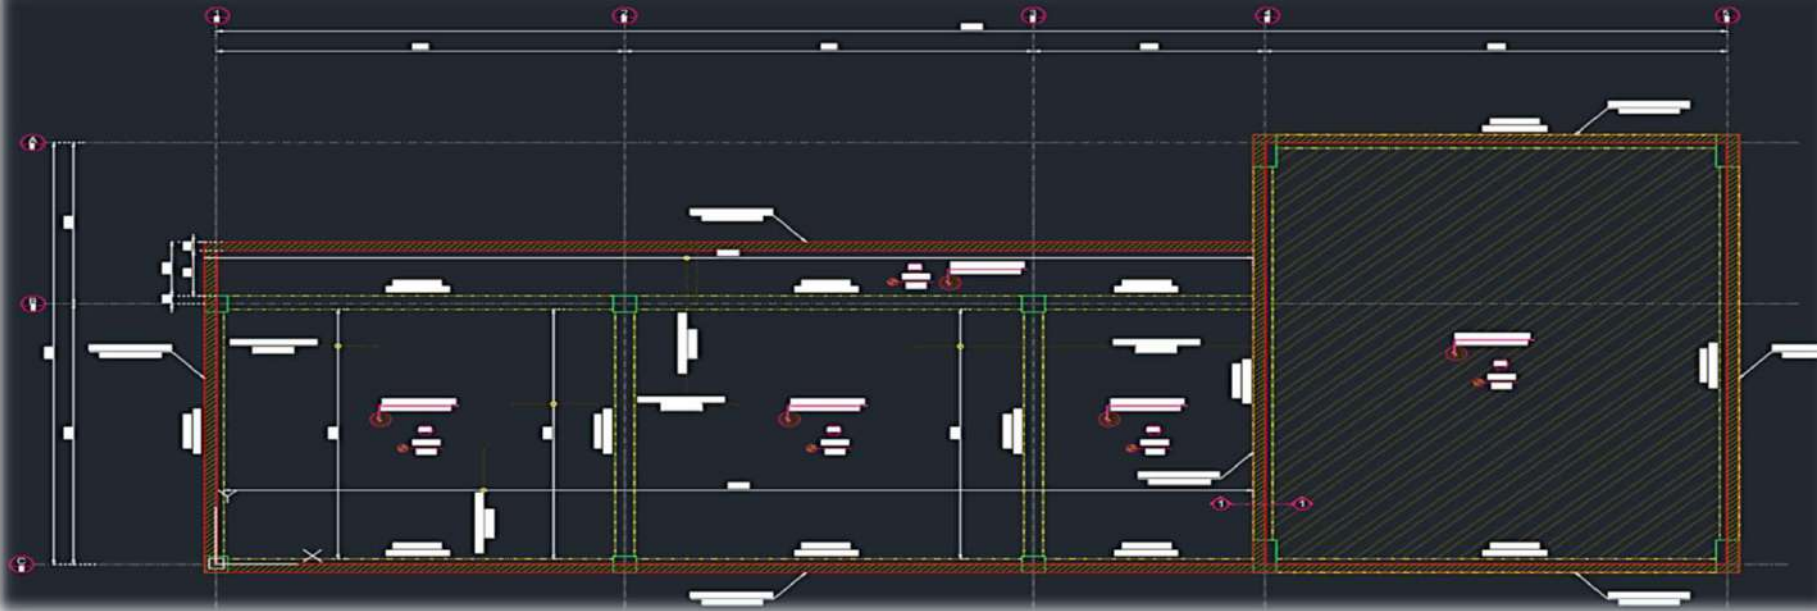

Notes:

1. THE COPYRIGHT OF THIS DRAWING IS VESTED IN YOURSPREADSHEETS AND IF ANY NOT BE REPRODUCED IN WHOLE OR IN PART OR USED FOR THE MANUFACTURE OF ANY ARTICLE WITHOUT THE EXPRESS PERMISSION OF THE COPYRIGHT HOLDERS.

2. WORK TO FIGURED DIMENSIONS ONLY.

Key plane

Before

Instructor :

YourSpreadsheets

Address line 1
Address line 2
Telephone line 1
Fax line 1
www.YourSpreadsheets.co.uk


CLIENT: BAHi CLIENT
3 Mossadeh, Ad Doui, Dokki,
Giza Governorate, Giza,
Egypt

ARCHITECT: Amr Mamdouh
40 Mossadeh, Ad Doui, Dokki,
Giza Governorate, Giza,
Egypt

SITE: 31 ROVER ROAD
BLOCK A AND B

TITLE: RC DETAILS AND SECTIONS
OF GROUND BEAMS

SCALE AT A2: 1:50: 1:100	DATE: 05/09/13	DRAWN: DJ	CHECKED: DJ
PROJECT NO: 24567	DRAWING NO: A2/248	REVISION: C	

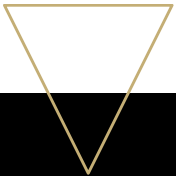

Thank You




Email

em3875050@email.com



Phone

+201012162395

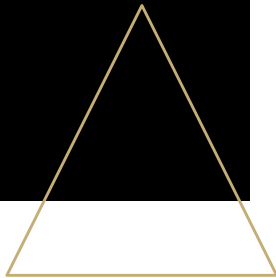

COURSE: TECHNICAL OFFICE G46

Name: Ibrahim Mohamed Read

Eng: Amr Mamdouh

Lecture: 9

Task: 7

الحصر الهندسي لبند المباني؟؟؟



Notes:

1. THE COPYRIGHT OF THIS DRAWING IS VESTED IN YOURSPREADSHEETS AND IT MAY NOT BE REPRODUCED IN WHOLE OR PART OR USED FOR THE MANUFACTURE OF ANY ARTICLE WITHOUT THE EXPRESS PERMISSION OF THE COPYRIGHT HOLDERS.
2. WORK TO DIMENSIONS ONLY.

Key plane

Before

Instructor :

YourSpreadsheets

Address line 1
Address line 2
Telephone line 1
Fax line 1
www.YourSpreadsheets.co.uk

CLIENT: BAH i CLIENT
3 Mossadak, Ad Doqi, Dokki,
Giza Governorate, Giza,
Egypt

ARCHITECT: Amr Mamdoh
40 Mossadak, Ad Doqi, Dokki,
Giza Governorate, Giza,
Egypt

SITE: 31 ROVER ROAD
BLOCK A AND B

TITLE: RC DETAILS AND SECTIONS
OF GROUND BEAMS

SCALE AT A2: 1:50, 1:100
DATE: 05/09/13
DRAWN: DJ
CHECKED: DJ
PROJECT NO: 24567
DRAWING NO: A2/248
REVISION: C

حصر أعمال المباني سمك ٢٥ سم على محاور X

ملاحظات	الإجمالي	التنزيل	الإضافة	مقاسات			العدد	وحدة القياس	بيان الأعمال و التوريدات
				ارتفاع	السمك	الطول			
الإضافة علي محور أ - أ	١,٧٥٢		١,٧٥٢	٢,٤	٠,٢٥	٢,٩٢		٣م	بالمتر المكعب توريد وبناء مباني من الطوب الأحمر المفرغ مقاس (6×12×25 سم)
التنزيل علي محور أ - أ شبك نموذج ش ١	٠,٣٦٠	٠,٣٦٠		١,٢	٠,٢٥	١,٢		٣م	
الإضافة علي محور ب - ب	١,٦٠٣		١,٦٠٣	٢,٤	٠,٢	٣,٣٤		٣م	
التنزيل علي محور ب - ب شبك نموذج ش ١	٠,٢٨٨	٠,٢٨٨		١,٢	٠,٢	١,٢		٣م	
الإضافة علي محور ز - ز	٢,٥٤٩		٢,٥٤٩	٢,٤	٠,٢	٥,٣١		٣م	
التنزيل علي محور ز - ز شبك نموذج ش ٢	٠,٠٩٨	٠,٠٩٨		٠,٧	٠,٢	٠,٧		٣م	

٥,١٥٨

اجمالي الحوائط سمك ٢٥ سم على محاور X

حصر أعمال المباني سمك ١٢ سم على محاور X

ملاحظات	الإجمالي	التنزيل	الإضافة	مقاسات		العدد	وحدة القياس	بيان الأعمال و التوريدات
				ارتفاع	الطول			
الإضافة علي محور ج - ج	٦,٠٩٦		٦,٠٩٦	٢,٤	٢,٥٤		٢م	بالمتر المسطح توريد وبناء مباني من الطوب الأحمر المفرغ مقاس (6×12×25 سم)
التنزيل علي محور ج - ج	٣,٣٠٠	٣,٣٠٠		٢,٢	١,٥		٣م	
الإضافة علي محور د - د	٧,٤٨٨		٧,٤٨٨	٢,٤	٣,١٢		٤م	
التنزيل علي محور د - د	١,٩٨٠	١,٩٨٠		٢,٢	٠,٩		٥م	
الإضافة علي محور هـ - هـ	١٠,٦٥٦		١٠,٦٥٦	٢,٤	٤,٤٤٠		٦م	
الإضافة بين محوري و - و ، ز - ز	٥,٧١٢		٥,٧١٢	٢,٤	٢,٣٨٠		٧م	
التنزيل بين محوري و - و ، ز - ز	١,٨٧٠	١,٨٧٠		٢,٢	٠,٨٥٠		٨م	
الإضافة علي محور ز - ز	١٢,٧٤٤		١٢,٧٤٤	٢,٤	٥,٣١٠		٩م	
الإضافة علي محور ح - ح	٠,٤٩٠		٠,٤٩٠	٠,٧	٠,٧٠٠		١٠م	

٣٦,٠٣٦

اجمالي الحوائط سمك ١٢ سم على محاور X

الحصر الهندسي لبند المباني؟؟؟



Notes:

1. THE COPYRIGHT OF THIS DRAWING IS VESTED IN YOURSPREADSHEETS AND IT MAY NOT BE REPRODUCED IN WHOLE OR PART OR USED FOR THE MANUFACTURE OF ANY ARTICLE WITHOUT THE EXPRESS PERMISSION OF THE COPYRIGHT HOLDERS.
2. WORK TO DIMENSIONS ONLY.

Key plane

Before

Instructor :

YourSpreadsheets

Address line 1
Address line 2
Telephone line 1
Fax line 1
www.YourSpreadsheets.co.uk

CLIENT: BAH i CLIENT
3 Mossadak, Ad Doqi, Dokki,
Giza Governorate, Giza,
Egypt

ARCHITECT: Amr Mamdoh
40 Mossadak, Ad Doqi, Dokki,
Giza Governorate, Giza,
Egypt

SITE: 31 ROVER ROAD
BLOCK A AND B

TITLE: RC DETAILS AND SECTIONS
OF GROUND BEAMS

SCALE AT A2: 1:50, 1:100 DATE: 05/09/13 DRAWN: DJ CHECKED: DJ
PROJECT NO: 24567 DRAWING NO: A2/248 REVISION: C

حصر أعمال المباني سمك ٢٥ سم على محاور y

ملاحظات	الإجمالي	التنزيل	الإضافة	مقاسات			العدد	وحدة القياس	بيان الأعمال و التوريدات
				ارتفاع	السمك	الطول			
الإضافة علي محور ١ - ١	٢,٩٧٦		٢,٩٧٦	٢,٤	٠,٢	٦,٢		٣م	بالمتر المكعب توريد وبناء مباني من الطوب الأحمر المفرغ مقاس (6x12x25 سم)
التنزيل علي محور ١ - ١ شباك نموذج ش ١	٠,٢٨٨-	٠,٢٨٨		١,٢	٠,٢	١,٢		٣م	
الإضافة علي محور ٤ - ٤	١,١١٤		١,١١٤	٢,٤	٠,٢	٢,٣٢		٣م	
الإضافة علي محور ٦ - ٦	٣,٧٦٨		٣,٧٦٨	٢,٤	٠,٢	٧,٨٥		٣م	
التنزيل علي محور ٦ - ٦ باب نموذج ب ١	٠,٤٤٠-	٠,٤٤٠		٢,٢	٠,٢	١		٣م	

٧,١٣٠

اجمالي الحوائط سمك ٢٥ سم على محاور X

حصر أعمال المباني سمك ١٢ سم على محاور X

ملاحظات	الإجمالي	التنزيل	الإضافة	مقاسات		العدد	وحدة القياس	بيان الأعمال و التوريدات
				ارتفاع	الطول			
الإضافة علي محور ٢ - ٢	٦,٣٨٤		٦,٣٨٤	٢,٤	٢,٦٦		٢م	بالمتر المسطح توريد وبناء مباني من الطوب الأحمر المفرغ مقاس (6x12x25 سم)
الإضافة علي محور ٣ - ٣	٨,٢٠٨		٨,٢٠٨	٢,٤	٣,٤٢		٣م	
التنزيل علي محور ٣ - ٣ باب نموذج ب ٢	٣,٩٦٠-	٣,٩٦٠		٢,٢	٠,٩	٢	٤م	
الإضافة علي محور ٥ - ٥	١٧,٠٤٠		١٧,٠٤٠	٢,٤	٧,١٠٠		٥م	
التنزيل علي محور ٥ - ٥	٢,٤٠٠-	٢,٤٠٠		٢,٤	١		٦م	

٢٥,٢٧٢

اجمالي الحوائط سمك ١٢ سم على محاور X

12.288

اجمالي الحوائط سمك ٢٥ سم على جميع المحاور

61.308

اجمالي الحوائط سمك ٢٥ سم على جميع المحاور

الحصر الهندسي لبند المباني؟؟؟



Notes:

1. THE COPYRIGHT OF THIS DRAWING IS VESTED IN YOURSPREADSHEETS AND IT MAY NOT BE REPRODUCED IN WHOLE OR PART OR USED FOR THE MANUFACTURE OF ANY ARTICLE WITHOUT THE EXPRESS PERMISSION OF THE COPYRIGHT HOLDERS.
2. WORK TO DIMENSIONS ONLY.

Key plane

Before

Instructor :

YourSpreadsheets

Address line 1
Address line 2
Telephone line 1
Fax line 1
www.YourSpreadsheets.co.uk

CLIENT: BAHi CLIENT
3 Mossadak, Ad Doqi, Dokki,
Giza Governorate, Giza,
Egypt

ARCHITECT: Amr Mamdoh
40 Mossadak, Ad Doqi, Dokki,
Giza Governorate, Giza,
Egypt

SITE: 31 ROVER ROAD
BLOCK A AND B

TITLE: RC DETAILS AND SECTIONS
OF GROUND BEAMS

SCALE AT A2: 1:50, 1:100	DATE: 05/09/13	DRAWN: DJ	CHECKED: DJ
PROJECT NO: 24567	DRAWING NO: A2/248	REVISION: C	

نسبة الهالك*	مسطح الحائط / مسطح الطوبه	٢م1	مسطح الحائط / مسطح الطوبه	نسبة الهالك*	٢م1
1.05*	1/(0.26*0.13*0.06)	٣م1	1/(0.26*0.06)	1.1*	٢م1
517.7514793	493.0966469	٣م1	64.1025641	67.3076923	٢م1

حساب كميات المون بالمتر المكعب

حساب كمية الماء	حساب كمية الرمل	حساب كمية الأسمنت	أبعاد الطوبه
1000	75	1000	3
12.288	?	12.288	?
0.92157	0.0061438	0.0368628	٦ * ١٢ * ٢٥

حساب كميات المون بالمتر المسطح

حساب كمية الماء	حساب كمية الرمل	حساب كمية الأسمنت	أبعاد الطوبه
1000	75	1000	3
61.308	?	61.308	?
4.5981	0.030654	0.183924	٦ * ١٢ * ٢٥

كل ١٠٠٠ طوبه ٣ شكاير أسمنت

كل ١٠٠٠ طوبه ٠,٥ م٣ رمل

كل ١٠٠٠ طوبه ٧٥ لتر ماء

كل ١ م³ رمل ٢٤ شكايرة اسمنت

اللوحة الهندسية التي تم عليها الحصر ؟؟؟



Notes:
1. THE COPYRIGHT OF THIS DRAWING IS VESTED IN YOURSPREADSHEETS AND IT MAY NOT BE REPRODUCED IN WHOLE OR PART OR USED FOR THE MANUFACTURE OF ANY ARTICLE WITHOUT THE EXPRESS PERMISSION OF THE COPYRIGHT HOLDERS.
2. WORK TO FIGURED DIMENSIONS ONLY.

Key plane

Before

Instructor :

YourSpreadsheets

Address line 1
Address line 2
Telephone line 1
Fax line 1
www.YourSpreadsheets.co.uk


CLIENT: BAHi CUENT
3 Mossadak, Ad Doqi, Dokki,
Giza Governorate, Giza,
Egypt

ARCHITECT: Amr Mamdoh
40 Mossadak, Ad Doqi, Dokki,
Giza Governorate, Giza,
Egypt

SITE: 31 ROVER ROAD
BLOCK A AND B

TITLE: RC DETAILS AND SECTIONS
OF GROUND BEAMS

SCALE AT A2: 1:50, 1:100	DATE: 05/09/13	DRAWN: DJ	CHECKED: DJ
PROJECT NO: 24567	DRAWING NO: A2/248	REVISION: C	

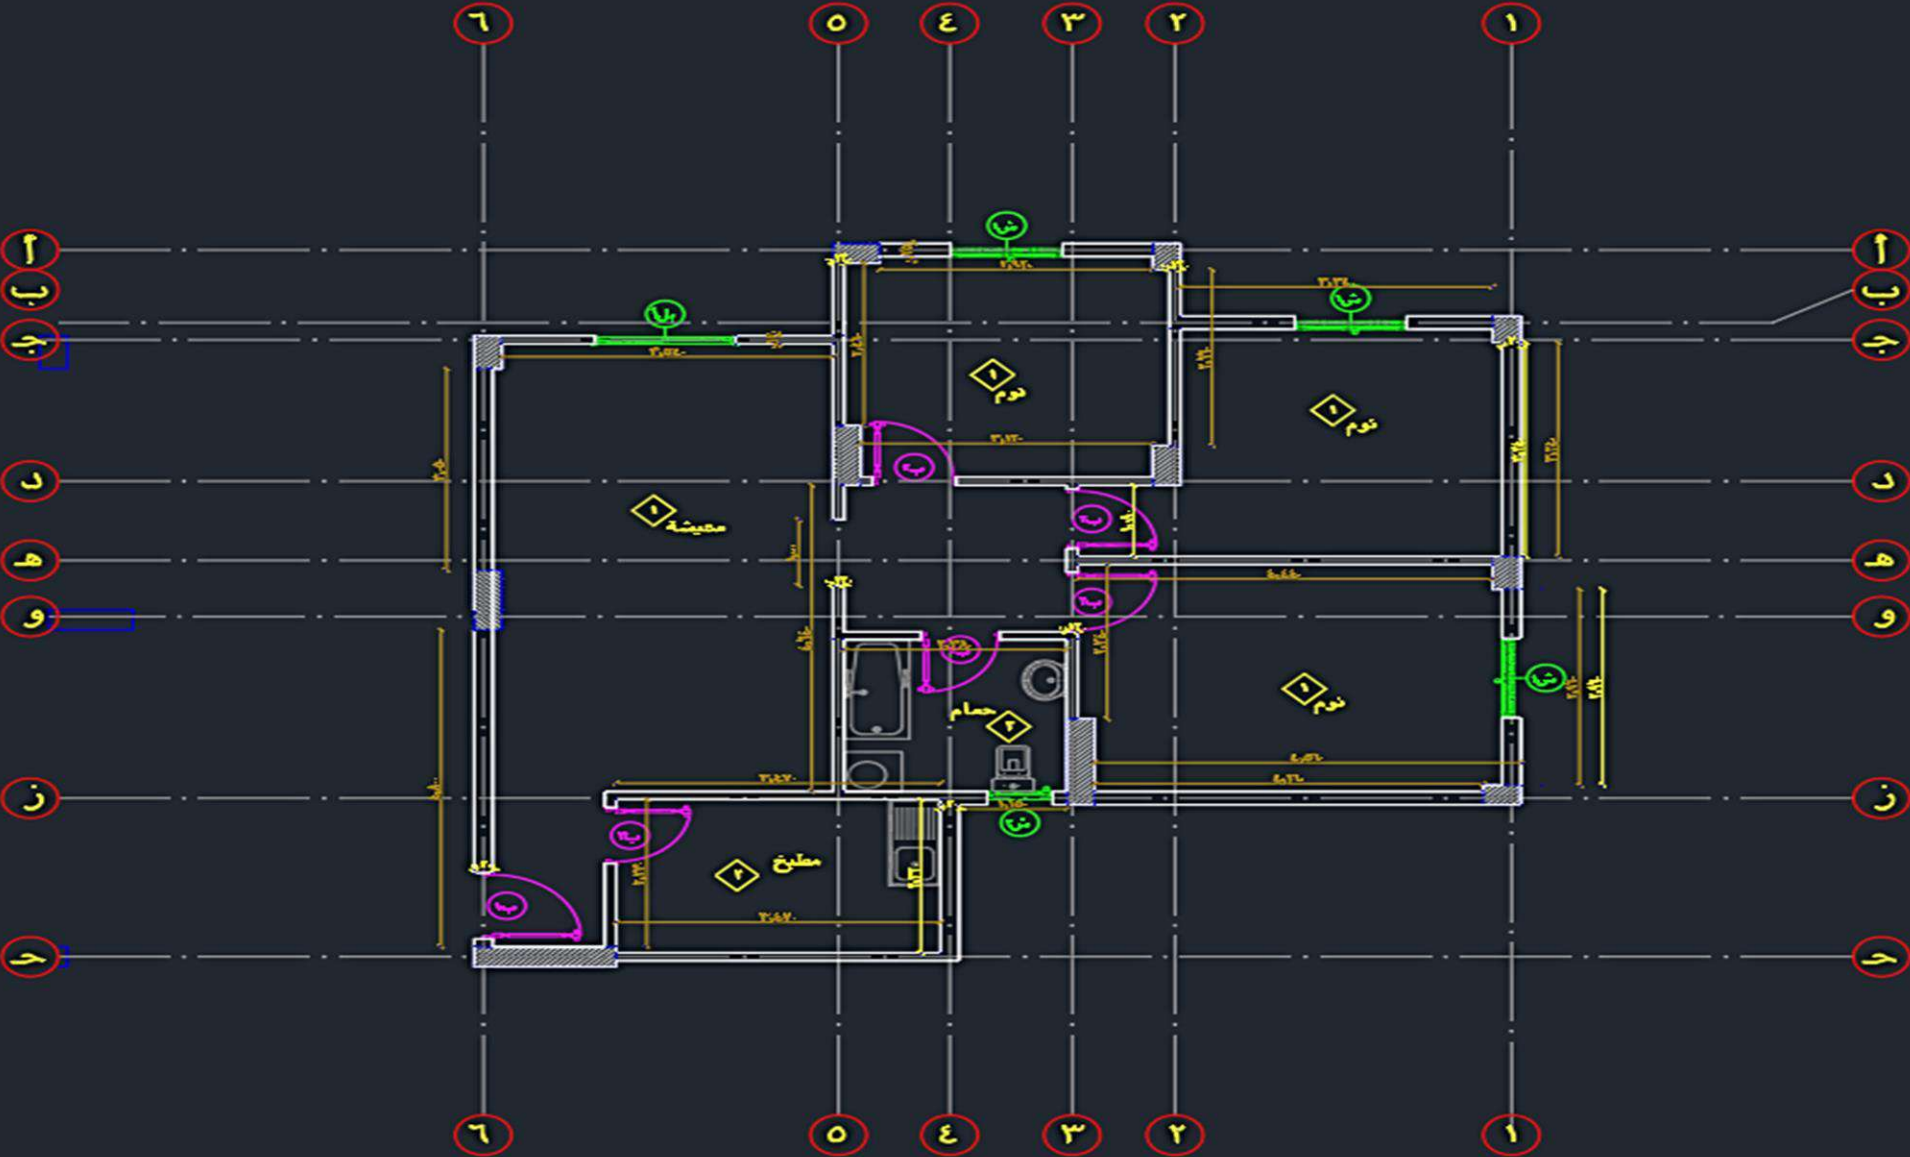

THE END

COURSE: TECHNICAL OFFICE G46

Name: Ibrahim Mohamed Read

Eng: Amr Mamdouh

Lecture: 10

Task: 8

الحصر الهندسي لبند أعمال البياض (الداخلي) ؟؟؟



Notes:

1. THE COPYRIGHT OF THIS DRAWING IS VESTED IN YOURSPREADSHEETS AND IT MAY NOT BE REPRODUCED IN WHOLE OR PART OR USED FOR THE MANUFACTURE OF ANY ARTICLE WITHOUT THE EXPRESS PERMISSION OF THE COPYRIGHT HOLDERS.
2. WORK TO FOUR DECIMALS ONLY.

Key plane

Before

Instructor :

YourSpreadsheets

Address line 1
Address line 2
Telephone line 1
Fax line 1
www.YourSpreadsheets.co.uk

CLIENT: BAH i CLIENT
3 Mossadak, Ad Doqi, Dokki,
Giza Governorate, Giza,
Egypt

ARCHITECT: Amr Mamdoh
40 Mossadak, Ad Doqi, Dokki,
Giza Governorate, Giza,
Egypt

SITE: 31 ROVER ROAD
BLOCK A AND B

TITLE: RC DETAILS AND SECTIONS
OF GROUND BEAMS

SCALE AT AS: 1:50, 1:100	DATE: 05/09/13	DRAWN: DJ	CHECKED: DJ
PROJECT NO: 24567	DRAWING NO: A2/248	REVISION: C	

حصر اعمال البياض الداخلي بسمك ٢ سم على محاور X

ملاحظات	الإجمالي	التنزيل	الإضافة	مقاسات		العدد	وحدة القياس	بيان الأعمال و التوريدات
				ارتفاع	الطول			
الإضافة علي محور أ - أ	١٠,٠٢٣		١٠,٠٢٣	٢,٦٨	٣,٧٤	١	٢م	بالمتر المسطح توريد وعمل بياض تخشين لزوم الحوائط الداخلية والأسقف بسمك ٢ سم علي محاور X على مشروع (معماري + إنشائي) والسعر يشمل كل مايلزم لنهوا الأعمال على الوجه الأمثل مما جميعه بالمتر المسطح
التنزيل علي محور أ - أ شبك نموذج ش ١	١,٤٤٠-	١,٤٤٠		١,٢	١,٢	١	٢م	
الإضافة علي محور ب - ب	٩,٦٤٨		٩,٦٤٨	٢,٦٨	٣,٦	١	٢م	
التنزيل علي محور ب - ب شبك نموذج ش ١	١,٤٤٠-	١,٤٤٠		١,٢	١,٢	١	٢م	
الإضافة علي محور ج - ج	١٠,٦٦٦		١٠,٦٦٦	٢,٦٨	٣,٩٨	١	٢م	
التنزيل علي محور ج - ج باب نموذج بل ١	٣,٣٠٠-	٣,٣٠٠		٢,٢	١,٥	١	٢م	
الإضافة علي محور د - د	١٨,٥٩٩		١٨,٥٩٩	٢,٦٨	٦,٩٤	١	٢م	
التنزيل علي محور د - د باب نموذج ب ٢	٣,٩٦٠-	٣,٩٦٠		٢,٢	٠,٩	٢	٢م	
الإضافة علي محور هـ - هـ	٢٥,١٣٨		٢٥,١٣٨	٢,٦٨	٩,٣٨	١	٢م	
الإضافة علي محور ز - ز	١٥,٢٧٦		١٥,٢٧٦	٢,٦٨	٥,٧	١	٢م	
التنزيل علي محور ز - ز	٠,٤١٠-	٠,٤١٠		٠,٠٩	٤,٥٦	١	٢م	
بياض الأسقف	٥٣,٢١٠		٥٣,٢١٠	٥٣,٢١		١	٢م	

١٣٢,٠١١

الإجمالي على محاور X

الحصر الهندسي لبند أعمال البياض (الداخلي) ؟؟؟



Notes:

1. THE COPYRIGHT OF THIS DRAWING IS VESTED IN YOURSIGNED AND IT MAY NOT BE REPRODUCED IN WHOLE OR PART OR USED FOR THE MANUFACTURE OF ANY ARTICLE WITHOUT THE EXPRESS PERMISSION OF THE COPYRIGHT HOLDER.
2. WORK TO DIMENSIONS ONLY.

Key plane

Before

Instructor :

YourSpreadsheets

Address line 1
Address line 2
Telephone line 1
Fax line 1
www.YourSpreadsheets.co.uk

CLIENT: BAH i CLIENT
3 Mossadak, Ad Doqi, Dokki,
Giza Governorate, Giza,
Egypt

ARCHITECT: Amr Mamdoh
40 Mossadak, Ad Doqi, Dokki,
Giza Governorate, Giza,
Egypt

SITE: 31 ROVER ROAD
BLOCK A AND B

TITLE: RC DETAILS AND SECTIONS
OF GROUND BEAMS

SCALE AT A2: 1:50, 1:100 DATE: 05/09/13 DRAWN: DJ CHECKED: DJ
PROJECT NO: 24567 DRAWING NO: A2/248 REVISION: C

حصر أعمال البياض الداخلي بسمك ٢ سم على محاور y

ملاحظات	الإجمالي	التنزيل	الإضافة	مقاسات		العدد	وحدة القياس	بيان الأعمال و التوريدات
				ارتفاع	الطول			
الإضافة علي محور ١ - ١	١٦,٤٠٢		١٦,٤٠٢	٢,٦٨	٦,١٢	١	٢م	بالمتر المسطح توريد وعمل بياض تخشين لزوم الحوائط الداخلية والأسقف بسمك ٢ سم علي محاور y على مشروع (معماري + إنشائي) والسعر يشمل كل مايلزم لنهوا الأعمال على الوجه الأمثل مما جميعه بالمتر المسطح
التنزيل علي محور ١ - ١ شبك نموذج ش ١	١,٤٤٠-	١,٤٤٠		١,٢	١,٢	١	٢م	
الإضافة علي محور ٢ - ٢	١٣,٣٤٦		١٣,٣٤٦	٢,٦٨	٤,٩٨	١	٢م	
الإضافة علي محور ٣ - ٣	١٤,٦٣٣		١٤,٦٣٣	٢,٦٨	٥,٤٦	١	٢م	
التنزيل علي محور ٣ - ٣ باب نموذج ب ١	٢,٤٠٠-	٢,٤٠٠		١,٢	١	٢	٢م	
الإضافة علي محور ٥ - ٥	٢٨,٦٧٦		٢٨,٦٧٦	٢,٦٨	١٠,٧	١	٢م	
الإضافة علي محور ٦ - ٦	٢٤,٩٥١		٢٤,٩٥١	٢,٦٨	٩,٣١	١	٢م	
التنزيل علي محور ٦ - ٦ باب نموذج ب ١	١,٢٠٠-	١,٢٠٠		١,٢	١	١	٢م	

٩٢,٩٦٨

الإجمالي على محاور y

224.978

اجمالي البياض الداخلي علي جميع المحاور بسمك ٢ سم على مشروح (معماري + إنشائي)

Arvil Group
CONSTRUCTION & TRAINING COMPANY

1. THE COPYRIGHT OF THIS DRAWING IS VESTED IN TOWERSPENCER AND IT MAY NOT BE REPRODUCED IN WHOLE OR PART OR USED FOR THE MANUFACTURE OF ANY ARTICLE WITHOUT THE EXPRESS PERMISSION OF THE COPYRIGHT HOLDERS.

2. WORK TO FIGURED DIMENSIONS ONLY.

Before

Address line 1
Address line 2
Telephone line 1
Fax line 1
www.YourSpreadsheets.co.uk

ARCHITECT: Amr Mamdoh
40 Mossadak, Ad Doqi, Dokki,
Giza Governorate, Giza,
Egypt

SCALE AT A2: 1:50, 1:100	DATE: 05/09/13	DRAWN: DJ	CHECKED: DJ
PROJECT NO: 24567	DRAWING NO: A2/248	REVISION: C	

ملاحظات	الإجمالي	التنزيل	الإضافة	مقاسات		العدد	وحدة القياس	بيان الأعمال و التوريدات
				ارتفاع	الطول			
الإضافة علي محور أ - أ	١١,٢٨٠		١١,٢٨٠	٣	٣,٧٦	١	٢م	بالمتر المسطح توريد وعمل بياض تخشين لزوم الحوائط الخارجية والأسقف بسمك ٢ سم علي محاور X على مشروع (معماري + إنشائي) والسعر يشمل كل مايلزم لنهؤ الأعمال على الوجه الأمثل مما جميعه بالمتر المسطح
التنزيل علي محور أ - أ شبك نموذج ش ١	١,٤٤٠-	١,٤٤٠		١,٢	١,٢	١	٢م	
الإضافة علي محور ب - ب	١٠,٩٢٠		١٠,٩٢٠	٣	٣,٦٤	١	٢م	
التنزيل علي محور ب - ب شبك نموذج ش ١	١,٤٤٠-	١,٤٤٠		١,٢	١,٢	١	٢م	
الإضافة علي محور ج - ج	١١,٥٢٠		١١,٥٢٠	٣	٣,٨٤	١	٢م	
التنزيل علي محور ج - ج باب نموذج بل ١	٣,٣٠٠-	٣,٣٠٠		٢,٢	١,٥	١	٢م	
الإضافة علي محور ز - ز	١٨,٠٣٠		١٨,٠٣٠	٣	٦,٠١	١	٢م	
التنزيل علي محور ز - ز	٠,٤١٠-	٠,٤١٠		٠,٠٩	٤,٥٦	١	٢م	
الإضافة علي محور ح - ح	٥,٣٢٠		٥,٣٢٠	٣	٥,٣٢	١	٢م	
٥٠,٤٨٠		الإجمالي على محاور X						

Notes:

1. THE COPYRIGHT OF THIS DRAWING IS VESTED IN YOURSPREADSHEETS AND IT MAY NOT BE REPRODUCED IN WHOLE OR PART OR USED FOR THE MANUFACTURE OF ANY ARTICLE WITHOUT THE EXPRESS PERMISSION OF THE COPYRIGHT HOLDERS.
2. WORK TO FOURED DIMENSIONS ONLY.

Key plane

Before

Instructor :

YourSpreadsheets

Address line 1
Address line 2
Telephone line 1
Fax line 1
www.YourSpreadsheets.co.uk

CLIENT: BAH E CLIENT
3 Mossadak, Ad Doqi, Dokki,
Giza Governorate, Giza,
Egypt

ARCHITECT: Amr Mamdoh
40 Mossadak, Ad Doqi, Dokki,
Giza Governorate, Giza,
Egypt

SITE: 31 ROVER ROAD
BLOCK A AND B

TITLE: RC DETAILS AND SECTIONS
OF GROUND BEAMS

SCALE AT A2: 1:50, 1:100	DATE: 05/09/13	DRAWN: DJ	CHECKED: DJ
PROJECT NO: 24567	DRAWING NO: A2/248	REVISION: C	

الحصر الهندسي لبند أعمال البياض (الخارجي) ؟؟؟

حصر أعمال البياض الخارجي بسمك ٢ سم على محاور y

ملاحظات	الإجمالي	التنزيل	الإضافة	مقاسات		العدد	وحدة القياس	بيان الأعمال و التوريدات
				ارتفاع	الطول			
الإضافة علي محور ١ - ١	٢٢,٣٢٠		٢٢,٣٢٠	٣	٧,٤٤	١	٢م	بالمتر المسطح توريد وعمل بياض تخشين لزوم الحوائط الخارجية والأسقف بسمك ٢ سم علي محاور y على مشروع (معماري + إنشائي) والسعر يشمل كل مايلزم لنهوا الأعمال على الوجه الأمثل مما جميعه بالمتر المسطح
التنزيل علي محور ١ - ١ شبك نموذج ش ١	١,٤٤٠-	١,٤٤٠		١,٢	١,٢	١	٢م	
الإضافة علي محور ٢ - ٢	٣,٣٠٠		٣,٣٠٠	٣	١,١	١	٢م	
الإضافة علي محور ٤ - ٤	٧,٠٨٠		٧,٠٨٠	٣	٢,٣٦	١	٢م	
الإضافة علي محور ٥ - ٥	٤,٢٠٠		٤,٢٠٠	٣	١,٤	١	٢م	
الإضافة علي محور ٦ - ٦	٢٨,٧٧٠		٢٨,٧٧٠	٣	٩,٥٩	١	٢م	
التنزيل علي محور ٦ - ٦ باب نموذج ب ١	١,٢٠٠-	١,٢٠٠		١,٢	١	١	٢م	
٦٣,٠٣٠		الإجمالي على محاور y						

113.510

اجمالي البياض الخارجي علي جميع المحاور بسمك ٢ سم على مشروح (معماري + إنشائي)

حساب كميات المون في بند البياض

مرحلة الطرطشه	مرحلة الملو أو الياسه
أسمنت ٩ شكاير رمل ١ م ٣ مياه ٢٢٥ لتر مياه	أسمنت ٦ شكاير رمل ٣ م ١ مياه ١٥٠ لتر مياه
200م طرطشه للحائط بسمك طرطشه ٠,٥	40م طبقة ملو بسمك ٢ سم

الحصر الهندسي لبند أعمال الدهانات (الداخلية)؟؟؟



Notes:

1. THE COPYRIGHT OF THIS DRAWING IS VESTED IN YOURSPREADSHEETS AND IT MAY NOT BE REPRODUCED IN WHOLE OR PART OR USED FOR THE MANUFACTURE OF ANY ARTICLE WITHOUT THE EXPRESS PERMISSION OF THE COPYRIGHT HOLDERS.
2. WORK TO DIMENSIONS ONLY.

Key plane

Before

Instructor :

YourSpreadsheets

Address line 1
Address line 2
Telephone line 1
Fax line 1
www.YourSpreadsheets.co.uk

CLIENT: BAH i CLIENT
3 Mossadak, Ad Doqi, Dokki,
Giza Governorate, Giza,
Egypt

ARCHITECT: Amr Mamdoh
40 Mossadak, Ad Doqi, Dokki,
Giza Governorate, Giza,
Egypt

SITE: 31 ROVER ROAD
BLOCK A AND B

TITLE: RC DETAILS AND SECTIONS
OF GROUND BEAMS

SCALE AT A2: 1:50, 1:100	DATE: 05/09/13	DRAWN: DJ	CHECKED: DJ
PROJECT NO: 24567	DRAWING NO: A2/248	REVISION: C	

حصر أعمال الدهانات الداخلية بسمك ٢ سم على محاور X

ملاحظات	الإجمالي	التنزيل	الإضافة	مقاسات		العدد	وحدة القياس	بيان الأعمال و التوريدات
				ارتفاع	الطول			
الإضافة علي محور أ - أ	١٠,٠٢٣		١٠,٠٢٣	٢,٦٨	٣,٧٤	١	٢م	بالمتر المسطح توريد وعمل دهانات لزوم الحوائط الداخلية والأسقف بسمك ٢ سم علي محاور X على مشروع (معماري + إنشائي) والسعر يشمل كل مايلزم لنهوا الأعمال على الوجه الأمثل مما جميعه بالمتر المسطح
التنزيل علي محور أ - أ شبك نموذج ش ١	١,٤٤٠-	١,٤٤٠		١,٢	١,٢	١	٢م	
الإضافة علي محور ب - ب	٩,٦٤٨		٩,٦٤٨	٢,٦٨	٣,٦	١	٢م	
التنزيل علي محور ب - ب شبك نموذج ش ١	١,٤٤٠-	١,٤٤٠		١,٢	١,٢	١	٢م	
الإضافة علي محور ج - ج	١٠,٦٦٦		١٠,٦٦٦	٢,٦٨	٣,٩٨	١	٢م	
التنزيل علي محور ج - ج باب نموذج بل ١	٣,٣٠٠-	٣,٣٠٠		٢,٢	١,٥	١	٢م	
الإضافة علي محور د - د	١٨,٥٩٩		١٨,٥٩٩	٢,٦٨	٦,٩٤	١	٢م	
التنزيل علي محور د - د باب نموذج ب ٢	٣,٩٦٠-	٣,٩٦٠		٢,٢	٠,٩	٢	٢م	
الإضافة علي محور هـ - هـ	٢٥,١٣٨		٢٥,١٣٨	٢,٦٨	٩,٣٨	١	٢م	
الإضافة علي محور ز - ز	١٥,٢٧٦		١٥,٢٧٦	٢,٦٨	٥,٧	١	٢م	
التنزيل علي محور ز - ز	٠,٤١٠-	٠,٤١٠		٠,٠٩	٤,٥٦	١	٢م	
دهان الأسقف	٦٧,٩٧٠		٦٧,٩٧٠	٦٧,٩٧٠٤		١	٢م	
١٤٦,٧٧١		الإجمالي على محاور X						

الحصر الهندسي لبند أعمال الدهانات (الداخلية)؟؟؟



Notes:

1. THE COPYRIGHT OF THIS DRAWING IS VESTED IN YOURSPREADSHEETS AND IT MAY NOT BE REPRODUCED IN WHOLE OR PART OR USED FOR THE MANUFACTURE OF ANY ARTICLE WITHOUT THE EXPRESS PERMISSION OF THE COPYRIGHT HOLDERS.
2. WORK TO DIMENSIONS ONLY.

Key plane

Before

Instructor :

YourSpreadsheets

Address line 1
Address line 2
Telephone line 1
Fax line 1
www.YourSpreadsheets.co.uk

CLIENT: BAH i CLIENT
3 Mossadak, Ad Doqi, Dokki,
Giza Governorate, Giza,
Egypt

ARCHITECT: Amr Mamdoh
40 Mossadak, Ad Doqi, Dokki,
Giza Governorate, Giza,
Egypt

SITE: 31 ROVER ROAD
BLOCK A AND B

TITLE: RC DETAILS AND SECTIONS
OF GROUND BEAMS

SCALE AT A2: 1:50, 1:100
DATE: 05/09/13
DRAWN: DJ
CHECKED: DJ
PROJECT NO: 24567
DRAWING NO: A2/248
REVISION: C

حصر أعمال الدهانات الداخلية بسمك ٢ سم على محاور y

ملاحظات	الإجمالي	التنزيل	الإضافة	مقاسات		العدد	وحدة القياس	بيان الأعمال و التوريدات
				ارتفاع	الطول			
الإضافة علي محور ١ - ١	١٦,٤٠٢		١٦,٤٠٢	٢,٦٨	٦,١٢	١	٢م	بالمتر المسطح توريد وعمل دهانات لزوم الحوائط الداخلية والأسقف بسمك ٢ سم علي محاور y على مشروع (معماري + إنشائي) والسعر يشمل كل مايلزم لنهوا الأعمال على الوجه الأمثل مما جميعه بالمتر المسطح
التنزيل علي محور ١ - ١ شبك نموذج ش ١	١,٤٤٠	١,٤٤٠		١,٢	١,٢	١	٢م	
الإضافة علي محور ٢ - ٢	١٣,٣٤٦		١٣,٣٤٦	٢,٦٨	٤,٩٨	١	٢م	
الإضافة علي محور ٣ - ٣	١٤,٦٣٣		١٤,٦٣٣	٢,٦٨	٥,٤٦	١	٢م	
التنزيل علي محور ٣ - ٣ باب نموذج ب ١	٢,٤٠٠	٢,٤٠٠		١,٢	١	٢	٢م	
الإضافة علي محور ٥ - ٥	٢٨,٦٧٦		٢٨,٦٧٦	٢,٦٨	١٠,٧	١	٢م	
الإضافة علي محور ٦ - ٦	٢٤,٩٥١		٢٤,٩٥١	٢,٦٨	٩,٣١	١	٢م	
التنزيل علي محور ٦ - ٦ باب نموذج ب ١	١,٢٠٠	١,٢٠٠		١,٢	١	١	٢م	
٩٢,٩٦٨		الإجمالي على محاور y						

239.739

اجمالي الدهانات الداخلية علي جميع المحاور بسمك ٢ سم على مشروع (معماري + إنشائي)

الحصر الهندسي لبند أعمال الدهانات (الخارجية) ٩٩٩



Notes:

1. THE COPYRIGHT OF THIS DRAWING IS VESTED IN TOWERSPENCER AND IT MAY NOT BE REPRODUCED IN WHOLE OR PART OR USED FOR THE MANUFACTURE OF ANY ARTICLE WITHOUT THE EXPRESS PERMISSION OF THE COPYRIGHT HOLDERS.

2. WORK TO FIGURED DIMENSIONS ONLY.

Key plane

Before

Instructor:

YourSpreadsheets

Address line 1
Address line 2
Telephone line 1
Fax line 1
www.YourSpreadsheets.co.uk

CLIENT: **BAH i CLIENT**
3 Mossadak, Ad Doqi, Dokki,
Giza Governorate, Giza,
Egypt

ARCHITECT: Amr Mamdoh
40 Mossadak, Ad Doqi, Dokki,
Giza Governorate, Giza,
Egypt

SITE: 31 ROVER ROAD
BLOCK A AND B

TITLE: RC DETAILS AND SECTIONS
OF GROUND BEAMS

SCALE AT A2: 1:50, 1:100	DATE: 05/09/13	DRAWN: DJ	CHECKED: DJ
PROJECT NO: 24567	DRAWING NO: A2/248	REVISION: C	

حصر أعمال الدهانات الخارجية بسمك ٢ سم على محاور X

ملاحظات	الإجمالي	النتزيل	الإضافة	مقاسات		العدد	وحدة القياس	بيان الأعمال و التوريدات
				الطول	ارتفاع			
الإضافة علي محور أ - أ	١١,٢٨٠		١١,٢٨٠	٣,٧٦	٣	١	٢م	بالمتر المسطح توريد وعمل دهانات لزوم الحوائط الخارجية والأسقف بسمك ٢ سم علي محاور X علي شروع (معماري + إنشائي) والسعر يشمل كل مايلزم لنهيو الأعمال على الوجه الأمثل مما جميعه بالمتر المسطح
النتزيل علي محور أ - أ شبك نموذج ش ١	١,٤٤٠-	١,٤٤٠		١,٢	١,٢	١	٢م	
الإضافة علي محور ب - ب	١٠,٩٢٠		١٠,٩٢٠	٣,٦٤	٣	١	٢م	
النتزيل علي محور ب - ب شبك نموذج ش ١	١,٤٤٠-	١,٤٤٠		١,٢	١,٢	١	٢م	
الإضافة علي محور ج - ج	١١,٥٢٠		١١,٥٢٠	٣,٨٤	٣	١	٢م	
النتزيل علي محور ج - ج باب نموذج بل ١	٣,٣٠٠-	٣,٣٠٠		١,٥	٢,٢	١	٢م	
الإضافة علي محور ز - ز	١٨,٠٣٠		١٨,٠٣٠	٦,٠١	٣	١	٢م	
النتزيل علي محور ز - ز	٠,٤١٠-	٠,٤١٠		٤,٥٦	٠,٠٩	١	٢م	
الإضافة علي محور ح - ح	٥,٣٢٠		٥,٣٢٠	٥,٣٢	٣	١	٢م	
٥٠,٤٨٠		الإجمالي علي محاور X						

الحصر الهندسي لبند أعمال الدهانات (الخارجية)؟؟؟



Notes:

1. THE COPYRIGHT OF THIS DRAWING IS VESTED IN YOURSPREADSHEETS AND IT MAY NOT BE REPRODUCED IN WHOLE OR PART OR USED FOR THE MANUFACTURE OF ANY ARTICLE WITHOUT THE EXPRESS PERMISSION OF THE COPYRIGHT HOLDERS.
2. WORK TO DIMENSIONS ONLY.

Key plane

Before

Instructor :

YourSpreadsheets

Address line 1
Address line 2
Telephone line 1
Fax line 1
www.YourSpreadsheets.co.uk

CLIENT: BAH i CLIENT
3 Mossadak, Ad Doqi, Dokki,
Giza Governorate, Giza,
Egypt

ARCHITECT: Amr Mamdoh
40 Mossadak, Ad Doqi, Dokki,
Giza Governorate, Giza,
Egypt

SITE: 31 ROVER ROAD
BLOCK A AND B

TITLE: RC DETAILS AND SECTIONS
OF GROUND BEAMS

SCALE AT A2: 1:50, 1:100	DATE: 05/09/13	DRAWN: DJ	CHECKED: DJ
PROJECT NO: 24567	DRAWING NO: A2/248	REVISION: C	

حصر أعمال الدهانات الخارجية بسمك ٢ سم على محاور y

ملاحظات	الإجمالي	التنزيل	الاضافه	مقاسات		العدد	وحدة القياس	بيان الأعمال و التوريدات
				ارتفاع	الطول			
الإضافة علي محور ١ - ١	٢٢,٣٢٠		٢٢,٣٢٠	٣	٧,٤٤	١	٢م	بالمتر المسطح توريد وعمل دهانات لزوم الحوائط الخارجية والأسقف بسمك ٢ سم علي محاور y على مشروع (معماري + إنشائي) والسعر يشمل كل مايلزم لنهوا الأعمال على الوجه الأمثل مما جميعه بالمتر المسطح
التنزيل علي محور ١ - ١ شبك نموذج ش ١	١,٤٤٠-	١,٤٤٠		١,٢	١,٢	١	٢م	
الأضافة على محور ٢ - ٢	٣,٣٠٠		٣,٣٠٠	٣	١,١	١	٢م	
الإضافة علي محور ٤ - ٤	٧,٠٨٠		٧,٠٨٠	٣	٢,٣٦	١	٢م	
الإضافة علي محور ٥ - ٥	٤,٢٠٠		٤,٢٠٠	٣	١,٤	١	٢م	
الإضافة علي محور ٦ - ٦	٢٨,٧٧٠		٢٨,٧٧٠	٣	٩,٥٩	١	٢م	
التنزيل علي محور ٦ - ٦ باب نموذج ب ١	١,٢٠٠-	١,٢٠٠		١,٢	١	١	٢م	
٦٣,٠٣٠		الإجمالي على محاور y						

113.510

اجمالي الدهانات الخارجية علي جميع المحاور بسمك ٢ سم على مشروح (معماري + إنشائي)

حساب كميات المون في بند الدهانات

معدلات الفرد تختلف من شركة دهانات لشركة اخرى على حسب كل بستله خاصه بشركه معينه تقوم بفرد كام متر مسطح ويراعا عند حساب المون إضافة نسبة الهالك

اللوحة الهندسية التي تم عليها الحصر ؟؟؟



Notes:

1. THE COPYRIGHT OF THIS DRAWING IS VESTED IN YOURSPREADSHEETS AND IT MAY NOT BE REPRODUCED IN WHOLE OR PART OR USED FOR THE MANUFACTURE OF ANY ARTICLE WITHOUT THE EXPRESS PERMISSION OF THE COPYRIGHT HOLDERS.
2. WORK TO FIGURED DIMENSIONS ONLY.

Key plane

Before

Instructor :

YourSpreadsheets

Address line 1
Address line 2
Telephone line 1
Fax line 1
www.YourSpreadsheets.co.uk


CLIENT: BAHi CUENT
3 Mossadak, Ad Doqi, Dokki,
Giza Governorate, Giza,
Egypt

ARCHITECT: Amr Mamdoh
40 Mossadak, Ad Doqi, Dokki,
Giza Governorate, Giza,
Egypt



SITE: 31 ROVER ROAD
BLOCK A AND B

TITLE: RC DETAILS AND SECTIONS
OF GROUND BEAMS

SCALE AT A2: 1:50, 1:100	DATE: 05/09/13	DRAWN: DJ	CHECKED: DJ
PROJECT NO: 24567	DRAWING NO: A2/248	REVISION: C	

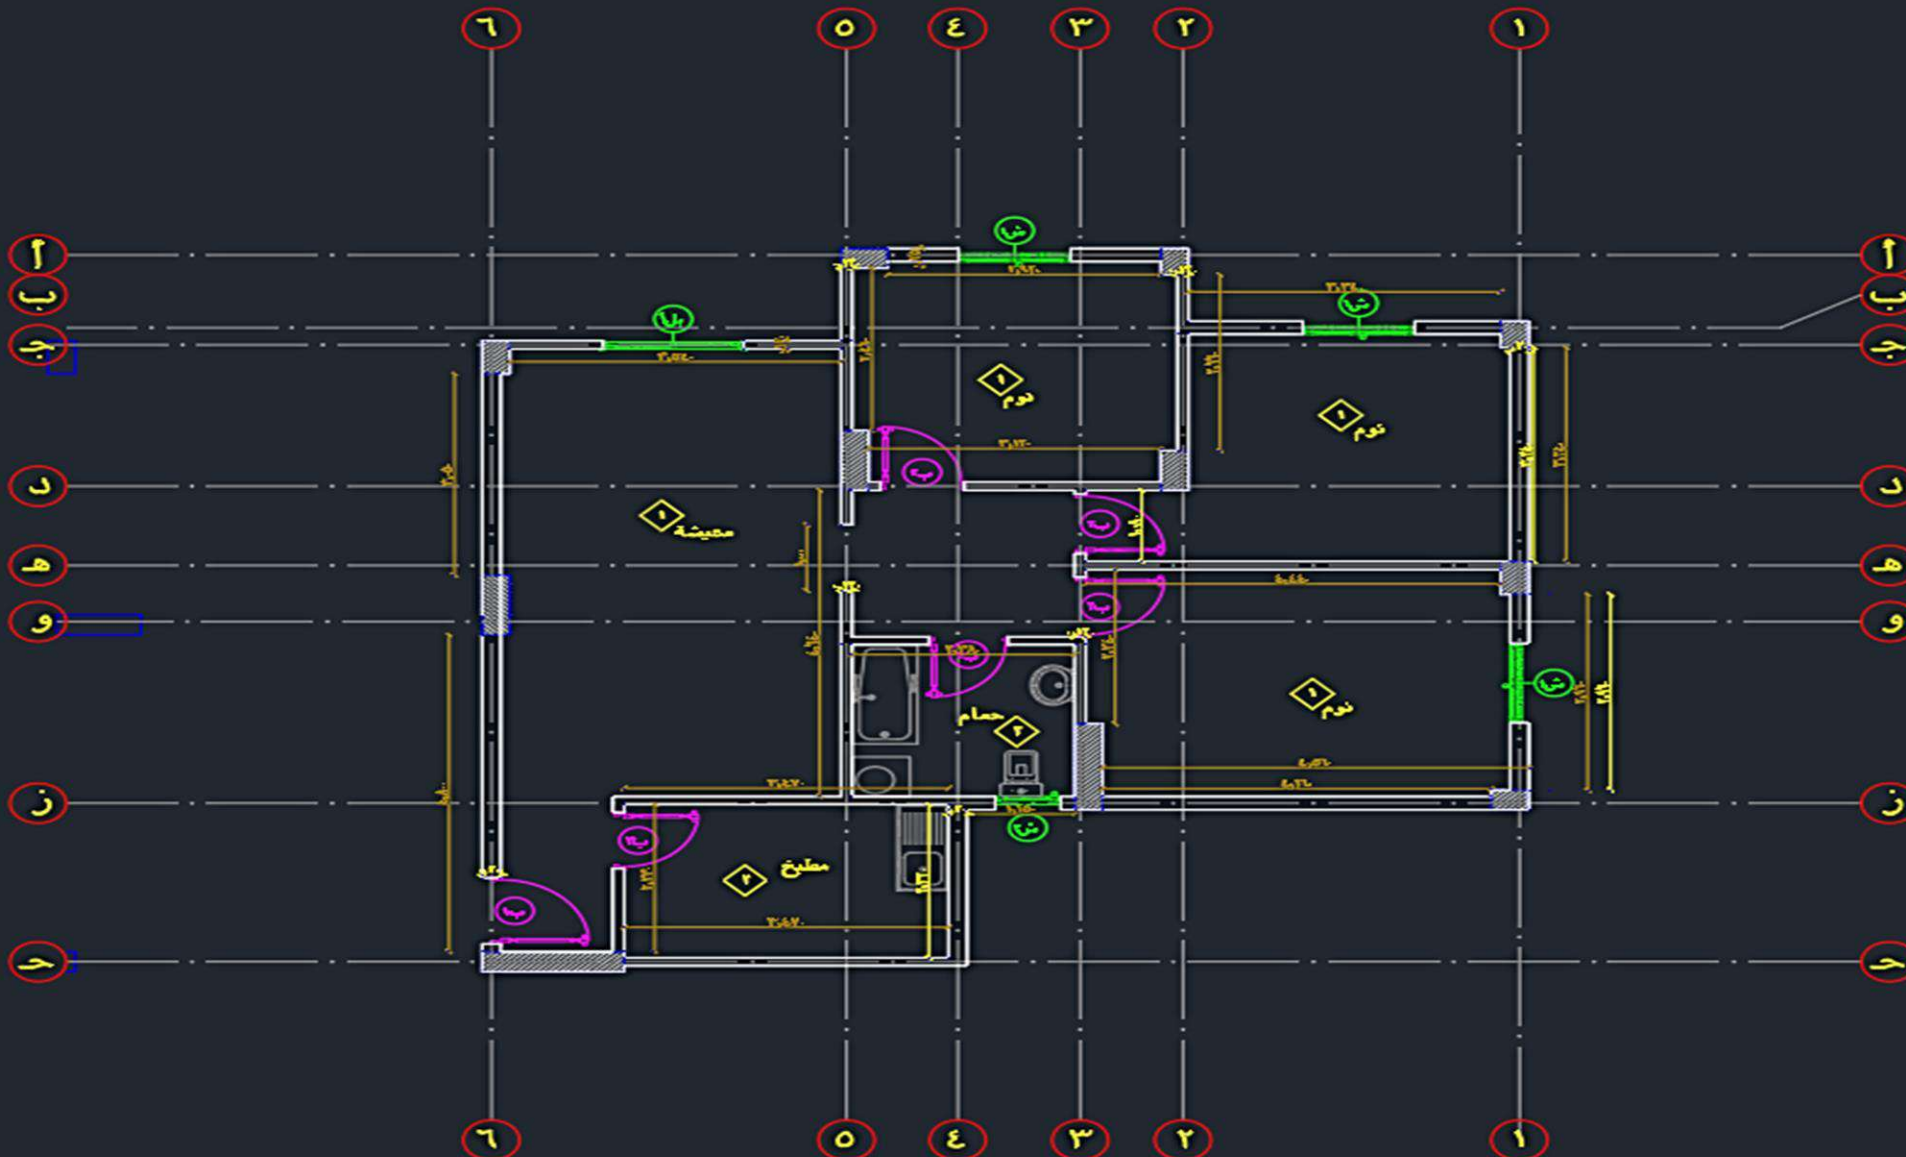

اللوحة الهندسية التي تم عليها حصر أعمال البياض؟؟؟

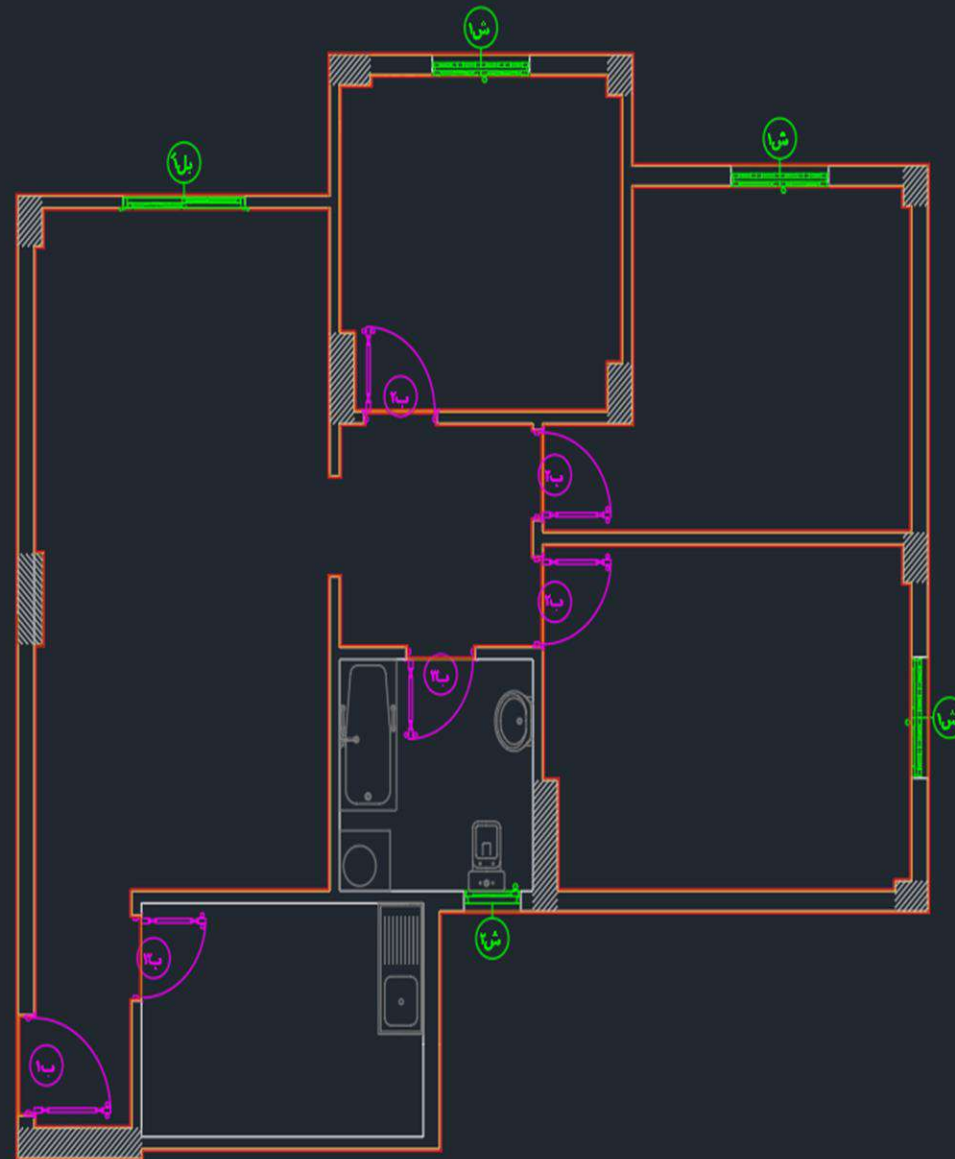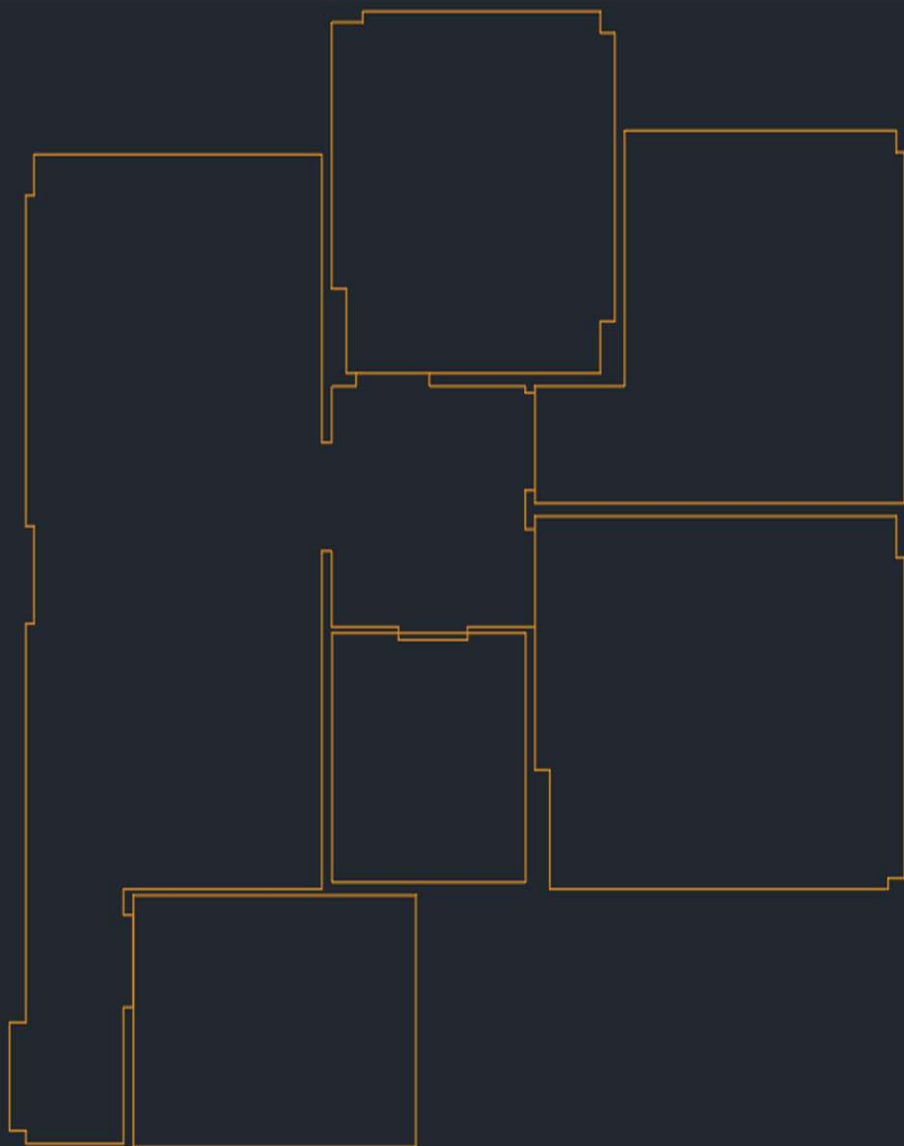

Notes:

1. THE COPYRIGHT OF THIS DRAWING IS VESTED IN YOURSPREADSHEETS AND IT MAY NOT BE REPRODUCED IN WHOLE OR PART OR USED FOR THE MANUFACTURE OF ANY ARTICLE WITHOUT THE EXPRESS PERMISSION OF THE COPYRIGHT HOLDERS.
2. WORK TO FIGURED DIMENSIONS ONLY.

Key plane

Before

Instructor :

YourSpreadsheets

Address line 1
Address line 2
Telephone line 1
Fax line 1
www.YourSpreadsheets.co.uk

CLIENT: **BAHI CLIENT**
3 Mossadak, Ad Doqi, Dokki,
Giza Governorate, Giza,
Egypt

ARCHITECT: **Amr Mamdoh**
40 Mossadak, Ad Doqi, Dokki,
Giza Governorate, Giza,
Egypt

SITE: **31 ROVER ROAD**
BLOCK A AND B

TITLE: **RC DETAILS AND SECTIONS**
OF GROUND BEAMS

SCALE AT A2: 1:50, 1:100	DATE: 05/09/13	DRAWN: DJ	CHECKED: DJ
PROJECT NO: 24567	DRAWING NO: A2/248	REVISION: C	

اللوحة الهندسية التي تم عليها حصر أعمال الدهانات؟؟؟



Notes:

1. THE COPYRIGHT OF THIS DRAWING IS VESTED IN YOURSPREADSHEETS AND IT MAY NOT BE REPRODUCED IN WHOLE OR PART OR USED FOR THE MANUFACTURE OF ANY ARTICLE WITHOUT THE EXPRESS PERMISSION OF THE COPYRIGHT HOLDERS.
2. WORK TO FIGURED DIMENSIONS ONLY.

Key plane

Before

Instructor :

YourSpreadsheets

Address line 1
Address line 2
Telephone line 1
Fax line 1
www.YourSpreadsheets.co.uk


CLIENT: **BAHI CUENT**
3 Mossadak, Ad Doqi, Dokki,
Giza Governorate, Giza,
Egypt

ARCHITECT: **Amr Mamdoh**
40 Mossadak, Ad Doqi, Dokki,
Giza Governorate, Giza,
Egypt

SITE: **31 ROVER ROAD
BLOCK A AND B**

TITLE: **RC DETAILS AND SECTIONS
OF GROUND BEAMS**

SCALE AT A2: 1:50, 1:100	DATE: 05/09/13	DRAWN: DJ	CHECKED: DJ
PROJECT NO: 24567	DRAWING NO: A2/248	REVISION: C	

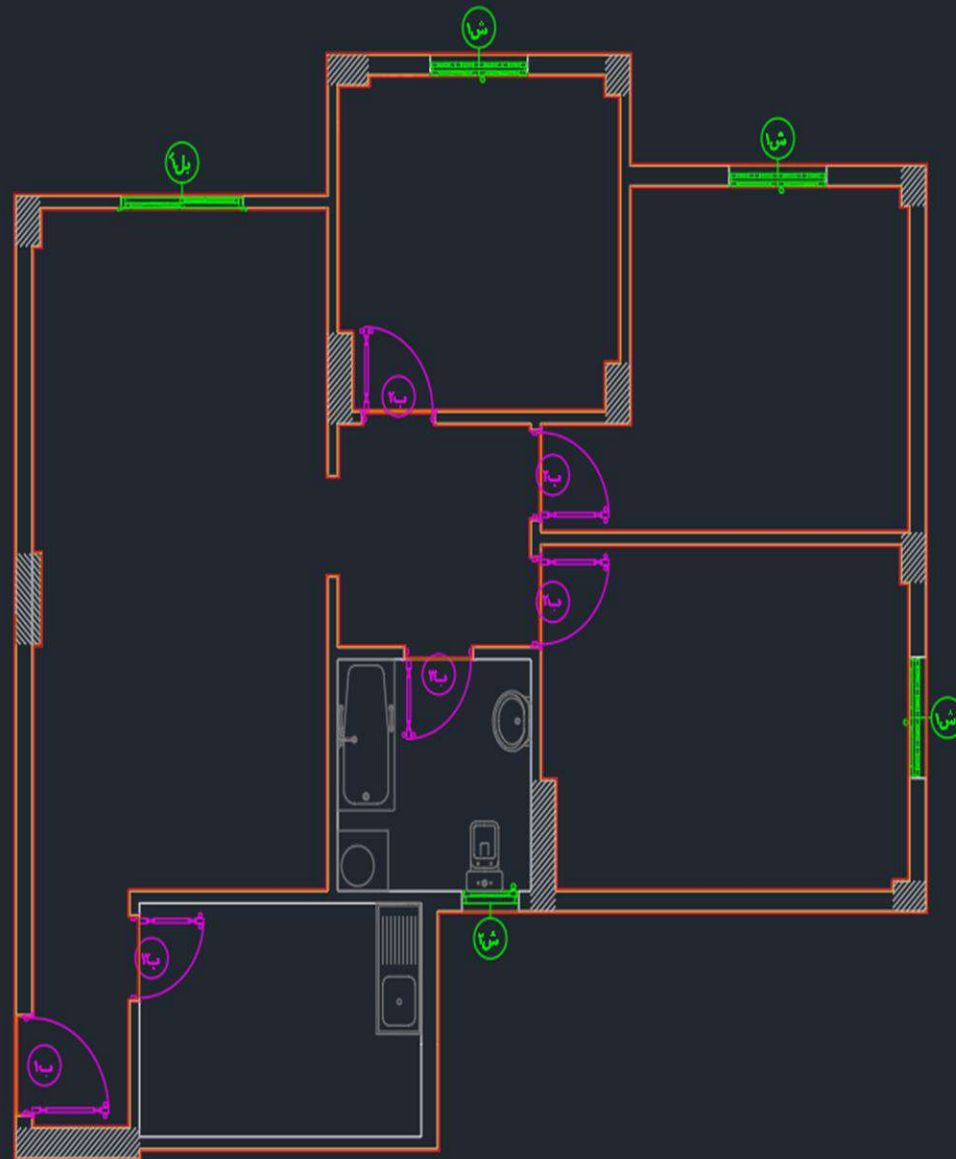

THE END

COURSE: TECHNICAL OFFICE G46

Name: Ibrahim Mohamed Read

Eng: Amr Mamdouh

Lecture: 11

Task: 9

الحصر الهندسي لبند أعمال السراميك (الأرضيات) ؟؟؟

حصر الأرضيات على لوحة (معماري + إنشائي)

Number	Area (m)	Add	Discount	Net
1	10.6504	10.6504		Room 1
2	12.2136	12.2136		Room 2
3	14.5736	14.5736		Room 3
4	31.6836796	31.6836796		Living
5	5.016	5.016		Toilet
5	-1.05		-1.05	Panio
6	7.4814	7.4814		Kitchen
Total	80.5686796			



Notes:

1. THE COPYRIGHT OF THIS DRAWING IS VESTED IN YOURSPREADSHEETS AND IT MAY NOT BE REPRODUCED IN WHOLE OR PART OR USED FOR THE MANUFACTURE OF ANY ARTICLE WITHOUT THE EXPRESS PERMISSION OF THE COPYRIGHT HOLDERS.
2. WORK TO DIMENSIONS ONLY.

Key plane

Before

Instructor :

YourSpreadsheets

Address line 1
Address line 2
Telephone line 1
Fax line 1
www.YourSpreadsheets.co.uk

CLIENT: BAH i CLIENT
3 Mossadak, Ad Doqi, Dokki,
Giza Governorate, Giza,
Egypt

ARCHITECT: Amr Mamdoh
40 Mossadak, Ad Doqi, Dokki,
Giza Governorate, Giza,
Egypt

SITE: 31 ROVER ROAD
BLOCK A AND B

TITLE: RC DETAILS AND SECTIONS
OF GROUND BEAMS

SCALE AT A2: 1:50, 1:100	DATE: 05/09/13	DRAWN: DJ	CHECKED: DJ
PROJECT NO: 24567	DRAWING NO: A2/248	REVISION: C	

الحصر الهندسي لبند أعمال السراميك (الأرضيات) ؟؟؟



Notes:

1. THE COPYRIGHT OF THIS DRAWING IS VESTED IN YOURSPREADSHEETS AND IT MAY NOT BE REPRODUCED IN WHOLE OR PART OR USED FOR THE MANUFACTURE OF ANY ARTICLE WITHOUT THE EXPRESS PERMISSION OF THE COPYRIGHT HOLDER.
2. WORK TO DIMENSIONS ONLY.

Key plane

Before

Instructor :

YourSpreadsheets

Address line 1
Address line 2
Telephone line 1
Fax line 1
www.YourSpreadsheets.co.uk

CLIENT: BAH i CLIENT
3 Mossadak, Ad Doqi, Dokki,
Giza Governorate, Giza,
Egypt

ARCHITECT: Amr Mamdoh
40 Mossadak, Ad Doqi, Dokki,
Giza Governorate, Giza,
Egypt

SITE: 31 ROVER ROAD
BLOCK A AND B

TITLE: RC DETAILS AND SECTIONS
OF GROUND BEAMS

SCALE AT A2: 1:50, 1:100	DATE: 05/09/13	DRAWN: DJ	CHECKED: DJ
PROJECT NO: 24567	DRAWING NO: A2/248	REVISION: C	

حصر حوائط الحمام والمطبخ لبند السراميك على لوحة (معماري + إنشائي)

Axe (x & y)	Area (m)		m2		Total	Net
	Length	Height	Add	Discount		
3 - 3 (y)	2.3	2.78	6.394		6.394	Toilet
5 - 5 (y)	2.3	2.78	6.394		6.394	Toilet
4 - 4 (y)	2.32	2.78	6.4496		6.4496	Kitchen
between axe 5 - 5 & axe 6 - 6 (y)	2.32	2.78	6.4496		6.4496	Kitchen
between axe 5 - 5 & axe 6 - 6 (y)	0.85	2.2		1.87	-1.87	door 3
between axe و - و & axe ز - ز (x)	2.38	2.78	6.6164		6.6164	Toilet
between axe و - و & axe ز - ز (x)	0.85	2.2		1.87	-1.87	door 3
ز - ز (x)	2.38	2.78	6.6164		6.6164	Toilet
ز - ز (x)	0.7	0.7		0.49	-0.49	window 2
ز - ز (x)	3.47	2.78	9.6466		9.6466	Kitchen
ح - ح (x)	3.47	2.78	9.6466		9.6466	Kitchen
Total	53.9832					

إجمالي كمية سراميك الأرضيات	80.5686796
إجمالي كمية سراميك الحوائط	53.9832

الحصر الهندسي لبند أعمال السراميك (الأرضيات) ؟؟؟



Notes:

1. THE COPYRIGHT OF THIS DRAWING IS VESTED IN YOURSPREADSHEETS AND IT MAY NOT BE REPRODUCED IN WHOLE OR PART OR USED FOR THE MANUFACTURE OF ANY ARTICLE WITHOUT THE EXPRESS PERMISSION OF THE COPYRIGHT HOLDERS.
2. WORK TO DIMENSIONS ONLY.

Key plane

Before

Instructor :

YourSpreadsheets

Address line 1
Address line 2
Telephone line 1
Fax line 1
www.YourSpreadsheets.co.uk

CLIENT: BAH i CLIENT
3 Mossadak, Ad Doqi, Dokki,
Giza Governorate, Giza,
Egypt

ARCHITECT: Amr Mamdoh
40 Mossadak, Ad Doqi, Dokki,
Giza Governorate, Giza,
Egypt

SITE: 31 ROVER ROAD
BLOCK A AND B

TITLE: RC DETAILS AND SECTIONS
OF GROUND BEAMS

SCALE AT A2: 1:50, 1:100	DATE: 05/09/13	DRAWN: DJ	CHECKED: DJ
PROJECT NO: 24567	DRAWING NO: A2/248	REVISION: C	

حساب الوز على لوحة (معماري + إنشائي)

Number	Area (m)	Add	Discount	Net
0	98.64024	98.64024		Perimeter
1	2.2		2.2	door 1
3	1.32		3.96	door 2
2	1.87		3.74	door 3
Total	108.54024			

ملحوظة: بالنسبة للوز يتم تحميلها على بند الأرضيات ولكن لحسابها نقوم بحساب محيط ال plan ونخصم منه فتحات الأبواب ونحصل على مجموع الوز بالمتري الطولي

Arvil Group
CONSTRUCTION & TRAINING COMPANY

1. THE COPYRIGHT OF THIS DRAWING IS VESTED IN TOWNSGROUNDS AND IT MAY NOT BE REPRODUCED IN WHOLE OR PART OR USED FOR THE MANUFACTURE OF ANY ARTICLE WITHOUT THE EXPRESS PERMISSION OF THE COPYRIGHT HOLDERS.

2. WORK TO FIGURED DIMENSIONS ONLY.

Before

Address line 1
Address line 2
Telephone line 1
Fax line 1
www.YourSpreadsheets.co.uk

ARCHITECT: Amr Mamdoh
40 Mossadak, Ad Doqi, Dokki,
Giza Governorate, Giza,
Egypt

SCALE AT A2: 1:50, 1:100	DATE: 05/09/13	DRAWN: DJ	CHECKED: DJ
PROJECT NO: 24567	DRAWING NO: A2/248		REVISION: C

حصر أعمال العزل لوش القواعد								
ملاحظات	الإجمالي	النتزيل	الإضافه	مقاسات		العدد	وحدة القياس	بيان الأعمال و التوريدات
				العرض	الطول			
	٣١,٨٧٥		٣١,٨٧٥	١,٢٥	١,٥	١٧	٢م	ق١
	١٨,٧٢٠		١٨,٧٢٠	١,٦	١,٩٥	٦	٢م	ق٢
	٢,١٢٥	٢,١٢٥		٠,٢٥	٠,٥	١٧	٢م	ع١
	٠,٩٠٠	٠,٩٠٠		٠,٢٥	٠,٦	٦	٢م	ع٢
٤٧,٥٧٠	الإجمالي							

الحصر الهندسي لبند أعمال العزل؟؟؟



Notes:

1. THE COPYRIGHT OF THIS DRAWING IS VESTED IN YOURSPREADSHEETS AND IT MAY NOT BE REPRODUCED IN WHOLE OR PART OR USED FOR THE MANUFACTURE OF ANY ARTICLE WITHOUT THE EXPRESS PERMISSION OF THE COPYRIGHT HOLDERS.
2. WORK TO DIMENSIONS ONLY.

Key plane

Before

Instructor :

YourSpreadsheets

Address line 1
Address line 2
Telephone line 1
Fax line 1
www.YourSpreadsheets.co.uk

CLIENT: BAH E CLIENT
3 Mossadak, Ad Doqi, Dokki,
Giza Governorate, Giza,
Egypt

ARCHITECT: Amr Mamdoh
40 Mossadak, Ad Doqi, Dokki,
Giza Governorate, Giza,
Egypt

SITE: 31 ROVER ROAD
BLOCK A AND B

TITLE: RC DETAILS AND SECTIONS
OF GROUND BEAMS

SCALE AT A2: 1:50, 1:100	DATE: 05/09/13	DRAWN: DJ	CHECKED: DJ
PROJECT NO: 24567	DRAWING NO: A2/248	REVISION: C	

حصر أعمال عزل الدكة الخرسانية

ملاحظات	الإجمالي	التنزيل	الإضافه	مقاسات	العدد	وحدة القياس	بيان الأعمال و التوريدات
				إجمالي مسطح الدكة الخرسانية			
	٨٩,٨٧٧		٨٩,٨٧٧	٨٩,٨٧٧٤٩١٦٤		٢م	حصر عزل الدكة الخرسانية
٨٩,٨٧٧		الإجمالي					

حصر أعمال عزل الحمام

ملاحظات	الإجمالي	التنزيل	الإضافه	مقاسات	العدد	وحدة القياس	بيان الأعمال و التوريدات
				إجمالي مسطح الحمام			
	٥,٤٧٤		٥,٤٧٤	٥,٤٧٤		٢م	حصر عزل الحمام
٥,٤٧٤		الإجمالي					

حصر أعمال عزل السطح

ملاحظات	الإجمالي	التنزيل	الإضافه	مقاسات	العدد	وحدة القياس	بيان الأعمال و التوريدات
				إجمالي مسطح السطح			
	١١٩,٧١٦		١١٩,٧١٦	١١٩,٧١٦		٢م	حصر عزل مباني قصية الردم
١١٩,٧١٦		الإجمالي					

Arvil Group
CONSTRUCTION & TRAINING COMPANY

1. THE COPYRIGHT OF THIS DRAWING IS VESTED IN TOWERSPENCER AND IT MAY NOT BE REPRODUCED IN WHOLE OR PART OR USED FOR THE MANUFACTURE OF ANY ARTICLE WITHOUT THE EXPRESS PERMISSION OF THE COPYRIGHT HOLDERS.

2. WORK TO FIGURED DIMENSIONS ONLY.

Before

Instructor:

Address line 1
Address line 2
Telephone line 1
Fax line 1
www.YourSpreadsheets.co.uk

ARCHITECT: Amr Mamdoh
40 Mossadak, Ad Doqi, Dokki,
Giza Governorate, Giza,
Egypt

SCALE AT A2: 1:50, 1:100	DATE: 05/09/13	DRAWN: DJ	CHECKED: DJ
PROJECT NO: 24567	DRAWING NO: A2/248	REVISION: C	

حصر أعمال عزل السمات								
ملاحظات	الإجمالي	التنزيل	الإضافة	مقاسات		العدد	وحدة القياس	بيان الأعمال و التوريدات
				السبك	إجمالي محيط السمات			
	١٠٢,٧٨٠		١٠٢,٧٨٠	٠,٥	٢٠٥,٥٦		٢م	حصر عزل السمات
١٠٢,٧٨٠		الإجمالي						

حصص أعمال عزل رقابي الأعمدة								
ملاحظات	الإجمالي	النتزير	الإضافة	مقاسات		العدد	وحدة القياس	بيان الأعمال و التوريدات
				الإرتفاع	إجمالي أطوال رقابي الأعمدة			
	٥٣,٥٣٩		٥٣,٥٣٩	١,٥	٣٥,٦٩٢٥		٢م	حصص عزل رقابي الأعمدة
٥٣,٥٣٩		الإجمالي						

حصار أعمال عزل مباني قصية الـردم								
ملاحظات	الإجمالي	النتزير	الإضافة	مقاسات		العدد	وحدة القياس	بيان الأعمال و التوريدات
				الإرتفاع	إجمالي أطوال مباني قصية الـردم			
	٤٨٩,١٥٩		٤٨٩,١٥٩	١,٦٥	٢٩٦,٤٦		٢م	حصار عزل مباني قصية الـردم
٤٨٩,١٥٩		الإجمالي						

اللوحة الهندسية التي تم عليها الحصر لبند الأرضيات وبند العزل؟؟؟



Notes:

1. THE COPYRIGHT OF THIS DRAWING IS VESTED IN YOURSIGNED AND IT MAY NOT BE REPRODUCED IN WHOLE OR PART OR USED FOR THE MANUFACTURE OF ANY ARTICLE WITHOUT THE EXPRESS PERMISSION OF THE COPYRIGHT HOLDER.
2. WORK TO FIGURED DIMENSIONS ONLY.

Key plane

Before

Instructor :

YourSpreadsheets

Address line 1
Address line 2
Telephone line 1
Fax line 1
www.YourSpreadsheets.co.uk


CLIENT: **BAHI CLIENT**
3 Mossadak, Ad Doqi, Dokki,
Giza Governorate, Giza,
Egypt

ARCHITECT: **Amr Mamdoh**
40 Mossadak, Ad Doqi, Dokki,
Giza Governorate, Giza,
Egypt

SITE: **31 ROVER ROAD
BLOCK A AND B**

TITLE: **RC DETAILS AND SECTIONS
OF GROUND BEAMS**


SCALE AT A2: 1:50, 1:100	DATE: 05/09/13	DRAWN: DJ	CHECKED: DJ
PROJECT NO: 24567	DRAWING NO: A2/248	REVISION: C	

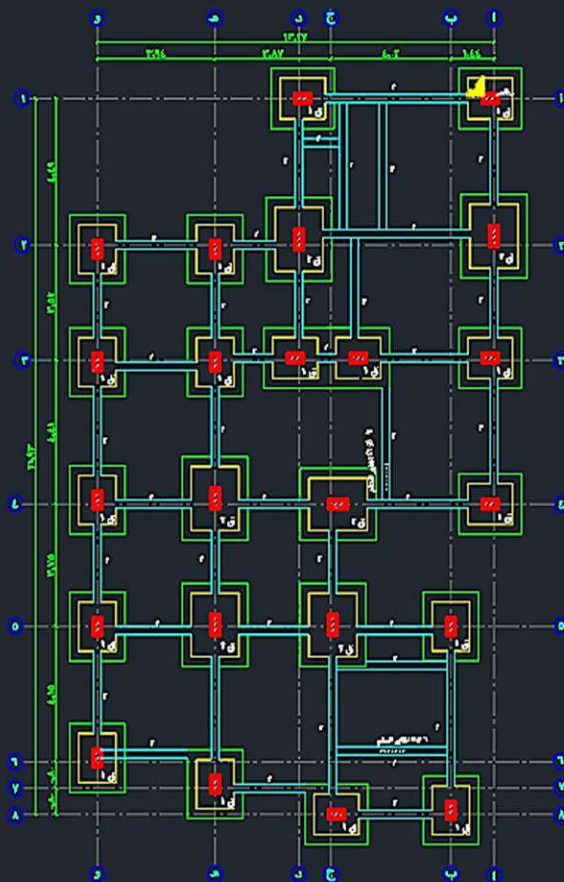

الاساسات



مخاور واعادة

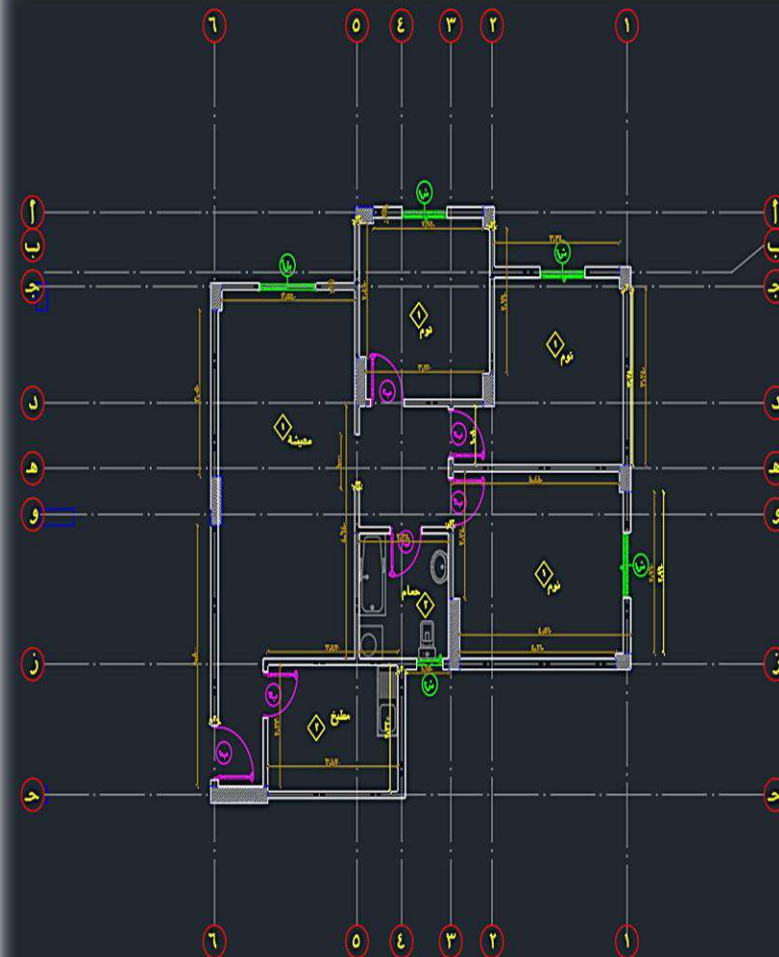

اللوحة الهندسية التي تم عليها حصر أعمال السراميك (الأرضيات) ؟؟؟



Notes:

1. THE COPYRIGHT OF THIS DRAWING IS VESTED IN YOURSPREADSHEETS AND IT MAY NOT BE REPRODUCED IN WHOLE OR PART OR USED FOR THE MANUFACTURE OF ANY ARTICLE WITHOUT THE EXPRESS PERMISSION OF THE COPYRIGHT HOLDERS.
2. WORK TO FIGURED DIMENSIONS ONLY.

Key plane

Before

Instructor :

YourSpreadsheets

Address line 1
Address line 2
Telephone line 1
Fax line 1
www.YourSpreadsheets.co.uk



CLIENT: **BAHI CLIENT**
3 Mossadak, Ad Doqi, Dokki,
Giza Governorate, Giza,
Egypt

ARCHITECT: **Amr Mamdoh**
40 Mossadak, Ad Doqi, Dokki,
Giza Governorate, Giza,
Egypt

SITE: **31 ROVER ROAD
BLOCK A AND B**

TITLE: **RC DETAILS AND SECTIONS
OF GROUND BEAMS**

SCALE AT A2: 1:50, 1:100	DATE: 05/09/13	DRAWN: DJ	CHECKED: DJ
PROJECT NO: 24567	DRAWING NO: A2/248	REVISION: C	

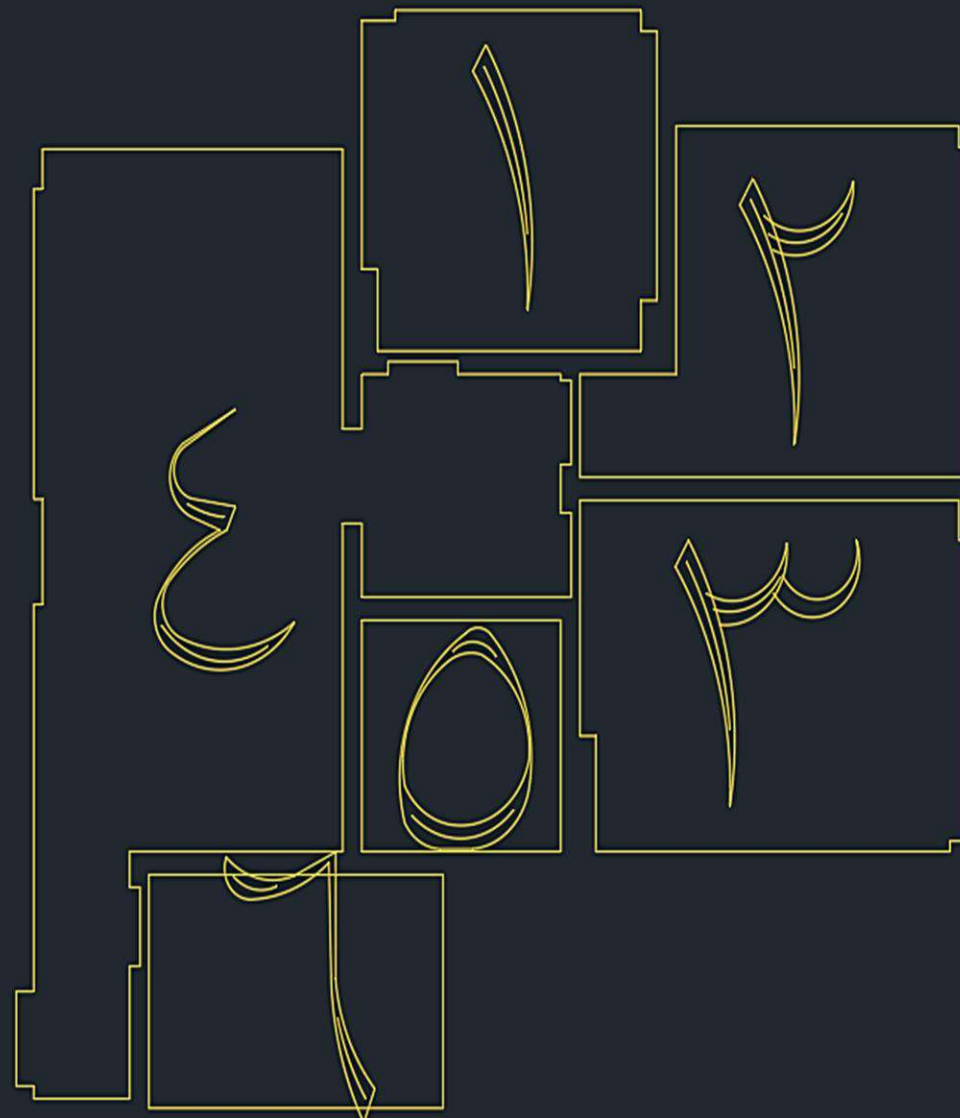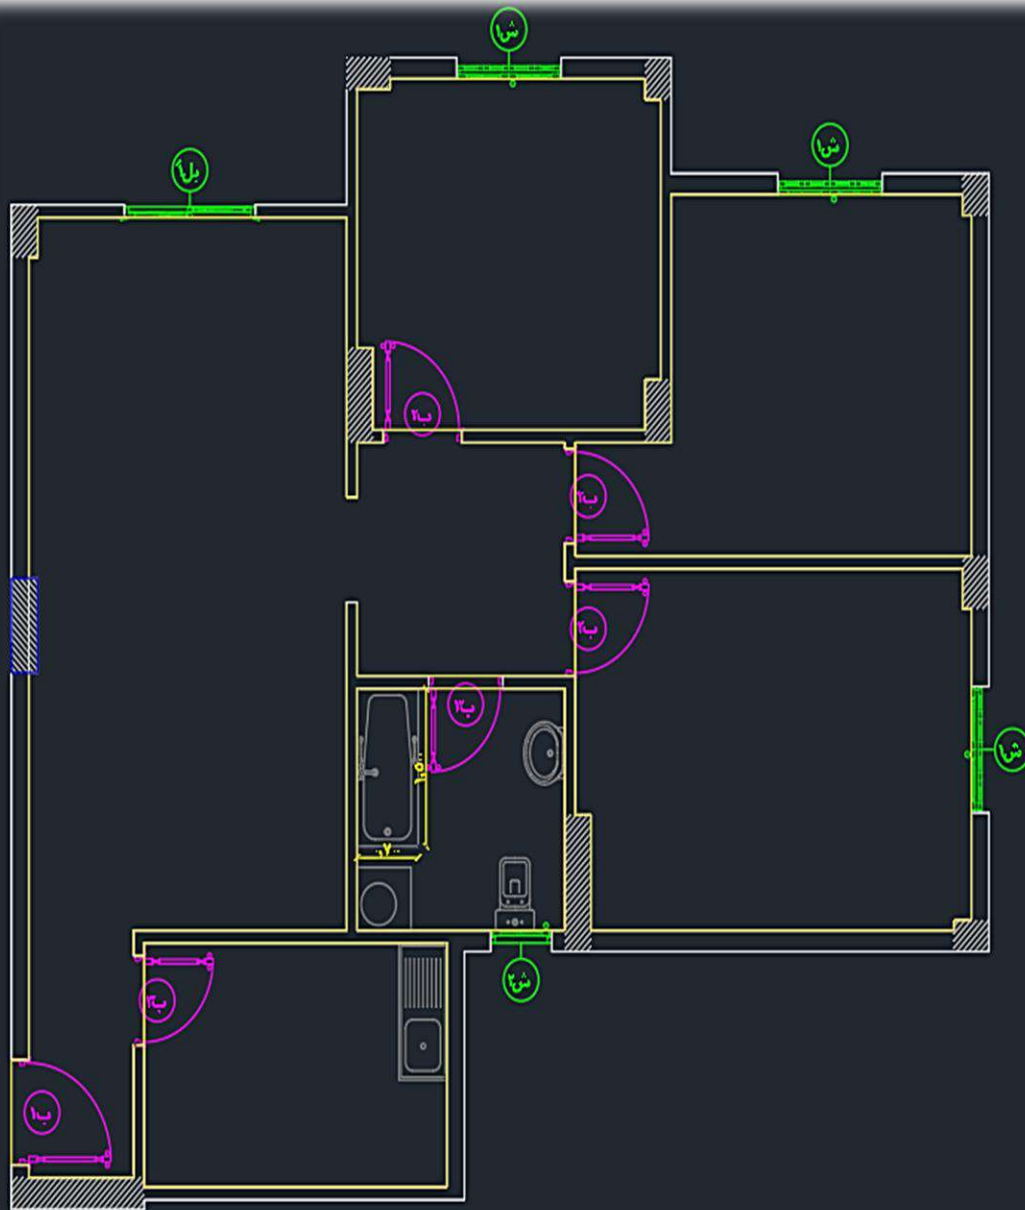

اللوحة الهندسية التي تم حصر أعمال العزل؟؟؟






Notes:

1. THE COPYRIGHT OF THIS DRAWING IS VESTED IN YOURSPREADSHEETS AND IT MAY NOT BE REPRODUCED IN WHOLE OR PART OR USED FOR THE MANUFACTURE OF ANY ARTICLE WITHOUT THE EXPRESS PERMISSION OF THE COPYRIGHT HOLDERS.
2. WORK TO DIMENSIONS ONLY.

Key plane

Before

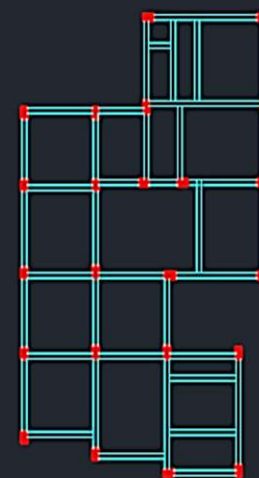
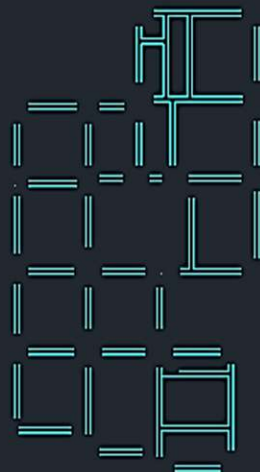
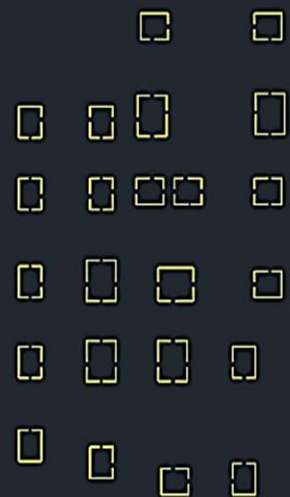


حصر عزل جوانب القواعد

حصر عزل السطحات

حصر عزل رقابي الأعمدة

حصر عزل مباني قصية الردم

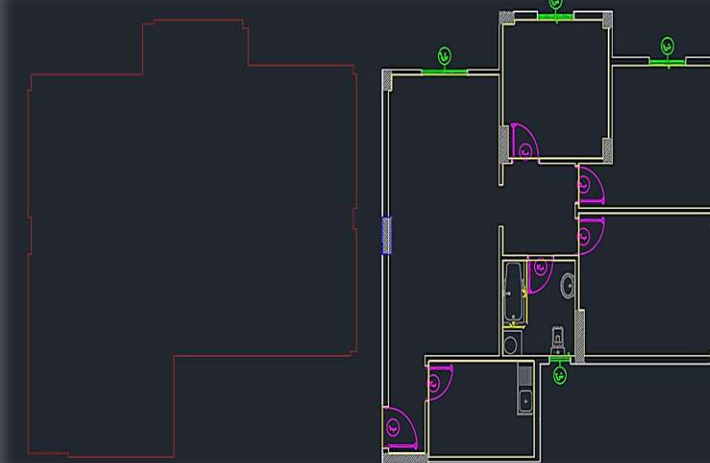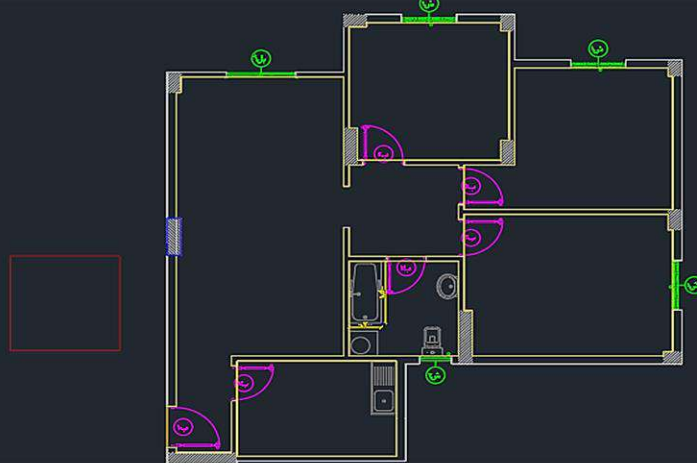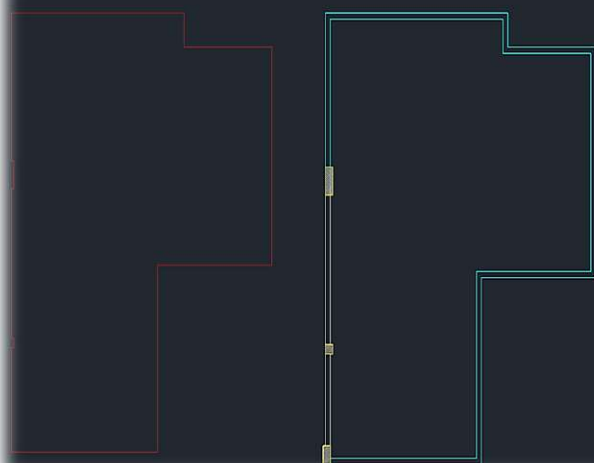

حصر عزل السطحات

حصر عزل الحمام

حصر عزل الدكة الخرسانية

Instructor :

YourSpreadsheets

Address line 1
Address line 2
Telephone line 1
Fax line 1
www.YourSpreadsheets.co.uk

CLIENT: BAH i CLIENT
3 Mossadak, Ad Doqi, Dokki,
Giza Governorate, Giza,
Egypt

ARCHITECT: Amr Mamdoh
40 Mossadak, Ad Doqi, Dokki,
Giza Governorate, Giza,
Egypt

SITE: 31 ROVER ROAD
BLOCK A AND B

TITLE: RC DETAILS AND SECTIONS
OF GROUND BEAMS

SCALE AT A2: 1:50, 1:100	DATE: 05/09/13	DRAWN: DJ	CHECKED: DJ
PROJECT NO: 24567	DRAWING NO: A2/248	REVISION: C	

THE END

COURSE: TECHNICAL OFFICE G46

Name: Ibrahim Mohamed Read

Eng: Amr Mamdouh

Lecture: 12

Task: 10

مقايست الأعمال المطلوبة + بعض الملاحظات

سلسل	البند	الوحدة	الكمية	الفئة	إجمالي
1	أعمال الحفر	م3	500	120	60000
2	أعمال الردم	م3	400	150	60000
3	خرسانة القواعد العادية	م3	30	3500	105000
4	خرسانة القواعد المسلحة والسملات	م3	40	8000	320000
5	الخرسانة المسلحة لأعمدة الدور الأرضي + الأول	م3	15	8900	133500
6	الخرسانة المسلحة لسقف الدور الأرضي + الأول	م3	100	8800	880000
7	خرسانة دكة الأرضية للدور الأرضي	م2	200	180	36000
8	مباني قصة الردم	م3	30	2000	60000
9	مباني الدور الأرضي	م2	20	900	18000
10	مباني الدور الأول + السطح	م2	280	800	224000
11	بياض المحارة الخارجى للواجهات	م2	450	250	112500
12	بياض المحارة الداخلى للدور الأرضي + الدور الأول	م2	600	200	120000
13	أعمال عزل القواعد المسلحة والسملات	مقط	1	10000	10000
14	أعمال عزل مباني قصة الردم	مقط	1	5000	5000
15	أعمال تأسيس الكهرباء	مقط	1	20000	20000
16	أعمال تأسيس السبابة	مقط	1	15000	15000
إجمالي قيمة الأعمال					2179000

ملاحظات :

- ✓ كمية خرسانة الاعمدة 9 م3 للدور الارضى و 5 م3 للدور الاول .
- ✓ فى شهر فبراير تبين أثناء مراجعة الحصر من خلال الاستشارى وجود خطأ فى حصر خرسانة القواعد العادية و حصر خرسانة القواعد المسلحة وبعد التصحيح أصبحت الكميات كالاتى خرسانة القواعد العادية = 32 م3 ، خرسانة القواعد المسلحة والسملات = 38 م3
- ✓ فى شهر ابريل حدثت زيادة فى أسعار حديد التسليح .. ما الاجراء المتبع بتلك الحالة ؟



Notes:

1. THE COPYRIGHT OF THIS DRAWING IS VESTED IN YOURSPREADSHEETS AND IT MAY NOT BE REPRODUCED IN WHOLE OR PART OR USED FOR THE MANUFACTURE OF ANY ARTICLE WITHOUT THE EXPRESS PERMISSION OF THE COPYRIGHT HOLDERS.
2. WORK TO DIMENSIONED DIMENSIONS ONLY.

Key plane

Before

Instructor :

YourSpreadsheets

Address line 1
Address line 2
Telephone line 1
Fax line 1
www.YourSpreadsheets.co.uk

CLIENT: BAH i CLIENT
3 Mossadak, Ad Doqi, Dokki,
Giza Governorate, Giza,
Egypt

ARCHITECT: Amr Mamdoh
40 Mossadak, Ad Doqi, Dokki,
Giza Governorate, Giza,
Egypt

SITE: 31 ROVER ROAD
BLOCK A AND B

TITLE: RC DETAILS AND SECTIONS
OF GROUND BEAMS

SCALE AT A2: 1:50, 1:100	DATE: 05/09/13	DRAWN: DJ	CHECKED: DJ
PROJECT NO: 24567	DRAWING NO: A2/248	REVISION: C	

مستخلص جاري رقم (١)

عن المدة من بداية الأعمال حتى تاريخ ٣٠ / يناير / ٢٠٢٤

مستخلص أعمال : جاري رقم ١

[illegible]

Notes:

1. THE COPYRIGHT OF THIS DRAWING IS VESTED IN TOWERSPENCER AND IT MAY NOT BE REPRODUCED IN WHOLE OR PART OR USED FOR THE MANUFACTURE OF ANY ARTICLE WITHOUT THE EXPRESS PERMISSION OF THE COPYRIGHT HOLDERS.

2. WORK TO FIGURED DIMENSIONS ONLY.

Key plane

Before

Instructor:

YourSpreadsheets

Address line 1
Address line 2
Telephone line 1
Fax line 1
www.YourSpreadsheets.co.uk

CLIENT: **BAH i CLIENT**
3 Mossadak, Ad Doqi, Dokki,
Giza Governorate, Giza,
Egypt

ARCHITECT: Amr Mamdoh
40 Mossadak, Ad Doqi, Dokki
Giza Governorate, Giza,
Egypt

SITE: 31 ROVER ROAD
BLOCK A AND B

TITLE: RC DETAILS AND SECTIONS
OF GROUND BEAMS

SCALE AT A2:
1:50, 1:100

DATE:
05/09/13

DRAWN: DJ	CHECKED:
--------------	----------

PROJECT NO:
24567

DRAWING NO:
A2/248

REVISED

مستخلص جاري رقم (١)



Notes:

1. THE COPYRIGHT OF THIS DRAWING IS VESTED IN YOURSPREADSHEETS AND IT MAY NOT BE REPRODUCED IN WHOLE OR PART OR USED FOR THE MANUFACTURE OF ANY ARTICLE WITHOUT THE EXPRESS PERMISSION OF THE COPYRIGHT HOLDERS.
2. WORK TO FIGURED DIMENSIONS ONLY.

Key plane

Before

Instructor :

YourSpreadsheets

Address line 1
Address line 2
Telephone line 1
Fax line 1
www.YourSpreadsheets.co.uk

CLIENT: BAH i CLIENT
3 Mossadak, Ad Doqi, Dokki,
Giza Governorate, Giza,
Egypt

ARCHITECT: Amr Mamdoh
40 Mossadak, Ad Doqi, Dokki,
Giza Governorate, Giza,
Egypt

SITE: 31 ROVER ROAD
BLOCK A AND B

TITLE: RC DETAILS AND SECTIONS
OF GROUND BEAMS

SCALE AT AS: 1:50, 1:100	DATE: 05/09/13	DRAWN: DJ	CHECKED: DJ
PROJECT NO: 24567	DRAWING NO: A2/248	REVISION: C	

الإستقطاعات

المبلغ المستقطع	النسبة - القيمة	بيان الأعمال
510000	510000	إجمالي الأعمال
25500	0.05	تأمين الأعمال
51000	0.1	دفعة مقدمة
76500	0.15	ضرائب وتأمينات
0	0	خصومات
0	0	السابق صرفة
357,000	الصافي المستحق بعد الإستقطاع	

مدير المشروع

مهندس الإستشاري

المدير المسنول

مهندس المشروع

مستخلص جاري رقم (٢)



Notes:

1. THE COPYRIGHT OF THIS DRAWING IS VESTED IN YOURSPREADSHEETS AND IT MAY NOT BE REPRODUCED IN WHOLE OR PART OR USED FOR THE MANUFACTURE OF ANY ARTICLE WITHOUT THE EXPRESS PERMISSION OF THE COPYRIGHT HOLDERS.
2. WORK TO DIMENSIONS ONLY.

Key plane

Before

Instructor :

YourSpreadsheets

Address line 1
Address line 2
Telephone line 1
Fax line 1
www.YourSpreadsheets.co.uk

CLIENT: BAHİ CLIENT
3 Mossadak, Ad Doqi, Dokki,
Giza Governorate, Giza,
Egypt

ARCHITECT: Amr Mamdoh
40 Mossadak, Ad Doqi, Dokki,
Giza Governorate, Giza,
Egypt

SITE: 31 ROVER ROAD
BLOCK A AND B

TITLE: RC DETAILS AND SECTIONS
OF GROUND BEAMS

SCALE AT A2: 1:50, 1:100
DATE: 05/09/13
PROJECT NO: 24567
DRAWN: DJ
CHECKED: DJ
REVISION: C

عن المدة من بداية الأعمال حتى تاريخ ٣٠ / فبراير / ٢٠٢٤

مستخلص أعمال : جاري رقم ٢

رقم البند	بيان الأعمال	الوحدة	الكمية	الفئة	قيمة الأعمال	مقدار كمية الأعمال			إجمالي قيمة الأعمال المنفذة حتى الآن	نسبة الصرف الحالية	المستحق صرفة	ملاحظات
						كمية المستخلص المسابق	كمية المستخلص الحالي	إجمالي مقدار كمية الأعمال المنفذة حتى الآن				
1	أعمال الحفر	م³	500	120	60000	500	0	500	60000	100%	60000	
2	أعمال الردم	م³	400	150	60000	400	0	400	60000	100%	60000	
3	خرسانة القواعد العادية	م³	30	3500	105000	30	2	32	112000	100%	112000	
4	خرسانة القواعد المسلحة والسملات	م³	40	8000	320000	40	-2	38	304000	100%	304000	
5	الخرسانة المسلحة لأعمدة الدور الأرضي + الدور الأول	م³	14	8900	124600	14	14	14	124600	60%	74760	
6	الخرسانة المسلحة لسقف الدور الأرضي + الدور الأول	م³	100	8800	880000	100	100	100	880000	30%	264000	
7	خرسانة الدكة الأرضية للدور الأرضي	م²	200	180	36000	200	200	200	36000	100%	36000	
8	مباني قصة الردم	م³	30	2000	60000	30	30	30	60000	100%	60000	
9	مباني الدور الأرضي	م²	20	900	18000	20	20	20	18000	0%	0	
10	مباني الدور الأول + السطح	م²	280	800	224000	280	280	280	224000	0%	0	
11	بياض المحارة الخارجي للوجهات	م²	450	250	112500	450	450	450	112500	0%	0	
12	بياض المحارة الداخلي للدور الأرضي + الدور الأول	م²	600	200	120000	600	600	600	120000	0%	0	
13	أعمال عزل القواعد المسلحة والسملات	مقط	1	10000	10000	1	0	1	10000	100%	10000	
14	أعمال عزل مباني قصة الردم	مقط	1	5000	5000	1	1	1	5000	100%	5000	
15	أعمال تأسيس الكهرباء	مقط	1	20000	20000	1	1	1	20000	0%	0	
16	أعمال تأسيس السباكة	مقط	1	15000	15000	1	1	1	15000	0%	0	
	إجمالي قيمة الأعمال حتى تاريخه					# تسعمائة وخمسة وثمانون ألفا وسبعمائة وستون جنية مصري فقط لا غير #					985760	

مستخلص جاري رقم (٢)

الإستقطاعات

المبلغ المستقطع	النسبة - القيمة	بيان الأعمال
985760	985760	إجمالي الأعمال
49288	0.05	تأمين الأعمال
98576	0.1	دفعة مقدمة
147864	0.15	ضرائب وتأمينات
0	0	خصومات
357.000	357.000	السابق صرفة
689,675	الصافي المستحق بعد الإستقطاع	



Notes:

1. THE COPYRIGHT OF THIS DRAWING IS VESTED IN YOURSPREADSHEETS AND IT MAY NOT BE REPRODUCED IN WHOLE OR PART OR USED FOR THE MANUFACTURE OF ANY ARTICLE WITHOUT THE EXPRESS PERMISSION OF THE COPYRIGHT HOLDERS.
2. WORK TO DIMENSIONS ONLY.

Key plane

Before

Instructor :

YourSpreadsheets

Address line 1
Address line 2
Telephone line 1
Fax line 1
www.YourSpreadsheets.co.uk

CUSTOMER: BAH i CLIENT
3 Mossadak, Ad Doqi, Dokki,
Giza Governorate, Giza,
Egypt

ARCHITECT: Amr Mamdoh
40 Mossadak, Ad Doqi, Dokki,
Giza Governorate, Giza,
Egypt

SITE: 31 ROVER ROAD
BLOCK A AND B

TITLE: RC DETAILS AND SECTIONS
OF GROUND BEAMS

SCALE AT A2: 1:50, 1:100	DATE: 05/09/13	DRAWN: DJ	CHECKED: DJ
PROJECT NO: 24567	DRAWING NO: A2/248	REVISION: C	

مدير المشروع

مهندس الإستشاري

المدير المسنول

مهندس المشروع

Arvil Group
CONSTRUCTION & TRAINING COMPANY

1. THE COPYRIGHT OF THIS DRAWING IS VESTED IN TOWNSEND & GREENE AND IT MAY NOT BE REPRODUCED IN WHOLE OR PART OR USED FOR THE MANUFACTURE OF ANY ARTICLE WITHOUT THE EXPRESS PERMISSION OF THE COPYRIGHT HOLDERS.

2. WORK TO FIGURED DIMENSIONS ONLY.

Before

Address line 1
Address line 2
Telephone line 1
Fax line 1
www.YourSpreadsheets.co.uk

SCALE AT A2: 1:50, 1:100	DATE: 05/09/13	DRAWN: DJ	CHECKED: DJ
PROJECT NO: 24567	DRAWING NO: A2/248	REVISION: C	

عن المدة من بداية الأعمال حتى تاريخ ٣٠ / مارس / ٢٠٢٤

[illegible]

مستخلص جاري رقم (٣)

الإستقطاعات

المبلغ المستقطع	النسبة - القيمة	بيان الأعمال
1167990	1167990	إجمالي الأعمال
58399.5	0.05	تأمين الأعمال
116799	0.1	دفعة مقدمة
175198.5	0.15	ضرائب وتأمينات
0	0	خصومات
689.675	689.675	السابق صرفة
816,903	الصافي المستحق بعد الإستقطاع	

مهندس المشروع	المدير المسئول	مهندس الإستشاري	مدير المشروع
---------------	----------------	-----------------	--------------



Notes:

1. THE COPYRIGHT OF THIS DRAWING IS VESTED IN YOURSPREADSHEETS AND IT MAY NOT BE REPRODUCED IN WHOLE OR PART OR USED FOR THE MANUFACTURE OF ANY ARTICLE WITHOUT THE EXPRESS PERMISSION OF THE COPYRIGHT HOLDERS.
2. WORK TO DIMENSIONS ONLY.

Key plane

Before

Instructor :

YourSpreadsheets

Address line 1
Address line 2
Telephone line 1
Fax line 1
www.YourSpreadsheets.co.uk

CLIENT: BAH i CLIENT
3 Mossadak, Ad Doqi, Dokki,
Giza Governorate, Giza,
Egypt

ARCHITECT: Amr Mamdoh
40 Mossadak, Ad Doqi, Dokki,
Giza Governorate, Giza,
Egypt

SITE: 31 ROVER ROAD
BLOCK A AND B

TITLE: RC DETAILS AND SECTIONS
OF GROUND BEAMS

SCALE AT A2: 1:50, 1:100	DATE: 05/09/13	DRAWN: DJ	CHECKED: DJ
PROJECT NO: 24567	DRAWING NO: A2/248	REVISION: C	

مستخلص جاري رقم (٤)

عن المدة من بداية الأعمال حتى تاريخ ٣٠ / ابريل / ٢٠٢٤

مستخلص أعمال : جاري رقم ٤

رقم البند	بيان الأعمال	الوحدة	الكمية	الفئة	قيمة الأعمال	مقدار كمية الأعمال			إجمالي قيمة الأعمال المنفذة حتى الآن	نسبة الصرف الحالية	المستحق صرافة	ملاحظات
						كمية المستخلص الحالي	كمية المستخلص المسبق	إجمالي مقدار كمية الأعمال المنفذة حتى الآن				
1	أعمال الحفر	م³	500	120	60000	500	0	500	60000	100%	60000	
2	أعمال الردم	م³	400	150	60000	400	0	400	60000	100%	60000	
3	خرسانة القواعد العادية	م³	30	3500	105000	30	2	32	112000	100%	112000	
4	خرسانة القواعد المسلحة والسملات	م³	40	8000	320000	40	-2	38	304000	100%	304000	
5	الخرسانة المسلحة لأعمدة الدور الأرضي + الدور الأول	م³	14	8900	124600	14	0	14	124600	100%	124600	
6	الخرسانة المسلحة لسقف الدور الأرضي + الدور الأول	م³	100	8800	880000	100	0	100	880000	100%	880000	
7	خرسانة الدكة الأرضية للدور الأرضي	م²	200	180	36000	200	0	200	36000	100%	36000	
8	مباني قصة الردم	م³	30	2000	60000	30	0	30	60000	100%	60000	
9	مباني الدور الأرضي	م²	20	900	18000	20	20	0	18000	80%	14400	
10	مباني الدور الأول + السطح	م²	280	800	224000	280	280		224000	0%	0	
11	بياض المحارة الخارجي للوجهات	م²	450	250	112500	450	450		112500	0%	0	
12	بياض المحارة الداخلي للدور الأرضي + الدور الأول	م²	600	200	120000	600	600		120000	0%	0	
13	أعمال عزل القواعد المسلحة والسملات	مقطن	1	10000	10000	1	0	1	10000	100%	10000	
14	أعمال عزل مباني قصة الردم	مقطن	1	5000	5000	1	0	1	5000	100%	5000	
15	أعمال تأسيس الكهرباء	مقطن	1	20000	20000	1	1	1	20000	0%	0	
16	أعمال تأسيس السباكة	مقطن	1	15000	15000	1	1	1	15000	0%	0	
	# مليون وستة وستون ألفاً جنية مصري فقط لاغير #											1666000
	إجمالي قيمة الأعمال حتى تاريخه											

Notes:

1. THE COPYRIGHT OF THIS DRAWING IS VESTED IN YOURSPREADSHEETS AND IT MAY NOT BE REPRODUCED IN WHOLE OR PART OR USED FOR THE MANUFACTURE OF ANY ARTICLE WITHOUT THE EXPRESS PERMISSION OF THE COPYRIGHT HOLDERS.
2. WORK TO DIMENSIONS ONLY.

Key plane

Before

Instructor :

YourSpreadsheets

Address line 1
Address line 2
Telephone line 1
Fax line 1
www.YourSpreadsheets.co.uk

CLIENT: BAHİ CLIENT
3 Mossadak, Ad Doqi, Dokki,
Giza Governorate, Giza,
Egypt

ARCHITECT: Amr Mamdoh
40 Mossadak, Ad Doqi, Dokki,
Giza Governorate, Giza,
Egypt

SITE: 31 ROVER ROAD
BLOCK A AND B

TITLE: RC DETAILS AND SECTIONS
OF GROUND BEAMS

SCALE AT A2: 1:50, 1:100	DATE: 05/09/13	DRAWN: DJ	CHECKED: DJ
PROJECT NO: 24567	DRAWING NO: A2/248	REVISION: C	

مستخلص جاري رقم (٤)



Notes:

1. THE COPYRIGHT OF THIS DRAWING IS VESTED IN YOURSPREADSHEETS AND IT MAY NOT BE REPRODUCED IN WHOLE OR PART OR USED FOR THE MANUFACTURE OF ANY ARTICLE WITHOUT THE EXPRESS PERMISSION OF THE COPYRIGHT HOLDERS.
2. WORK TO DIMENSIONS ONLY.

Key plane

Before

Instructor :

YourSpreadsheets

Address line 1
Address line 2
Telephone line 1
Fax line 1
www.YourSpreadsheets.co.uk

CLIENT: BAH I CLIENT
3 Mossadak, Ad Doqi, Dokki,
Giza Governorate, Giza,
Egypt

ARCHITECT: Amr Mamdoh
40 Mossadak, Ad Doqi, Dokki,
Giza Governorate, Giza,
Egypt

SITE: 31 ROVER ROAD
BLOCK A AND B

TITLE: RC DETAILS AND SECTIONS
OF GROUND BEAMS

SCALE AT A2: 1:50, 1:100	DATE: 05/09/13	DRAWN: DJ	CHECKED: DJ
PROJECT NO: 24567	DRAWING NO: A2/248	REVISION: C	

الإستقطاعات

بيان الأعمال	النسبة - القيمة	المبلغ المستقطع
إجمالي الأعمال	1666000	1666000
تأمين الأعمال	0.05	83300
دفعة مقدمة	0.1	166600
ضرائب وتأمينات	0.15	249900
خصومات	0	0
السابق صرفة	816.903	816.903
الصافي المستحق بعد الإستقطاع		1,165,383

الإجراءات المتبعة في حدوث زيادة في أسعار حديد التسليح:

المعامل = قيمة الوحدة في البند * الفئة

نسبة الزيادة = (السعر الحالي - السعر المتعاقد عليه) / السعر المتعاقد عليه

القيمة التعويضية عن نسبة الزيادة = المعامل * نسبة الزيادة * الفئة المسعرة * الكمية المنفذة في البند التي يتم التعويض عنها

• يتم التعويض مع الجهات الحكومية طبقا لقانون ١٨٢

• أما الجهات الخاصة يتم ذلك حسب الاتفاق في العقد

مهندس المشروع

المدير المسئول

مهندس الإستشاري

مدير المشروع

مستخلص جاري رقم (٥)



Notes:

1. THE COPYRIGHT OF THIS DRAWING IS VESTED IN TOWNSEND & GREENE AND IT MAY NOT BE REPRODUCED IN WHOLE OR PART OR USED FOR THE MANUFACTURE OF ANY ARTICLE WITHOUT THE EXPRESS PERMISSION OF THE COPYRIGHT HOLDERS.

2. WORK TO FIGURED DIMENSIONS ONLY.

2. WORK TO FIGURED DIMENSIONS ONLY.

Key plane

Before

Instructor :

YourSpreadsheets

Address line 1
Address line 2
Telephone line 1
Fax line 1
www.YourSpreadsheets.co.uk

CLIENT: **BAH i CLIENT**
3 Mossadak, Ad Doqi, Dokki,
Giza Governorate, Giza,
Egypt

ARCHITECT: Amr Mamdoh
40 Mossadak, Ad Doqi, Dokki,
Giza Governorate, Giza,
Egypt

SITE: 31 ROVER ROAD
BLOCK A AND B

TITLE:	RC DETAILS AND SECTIONS OF GROUND BEAMS
--------	--

SCALE AT A2: 1:50, 1:100	DATE: 05/09/13	DRAWN: DJ	CHECKED: DJ
PROJECT NO: 24567	DRAWING NO: A2/248	REVISION: C	

مستخلص أعمال : جاري رقم ٥

عن المدة من بداية الأعمال حتى تاريخ ٣٠ / مايو / ٢٠٢٤

[illegible]

مستخلص جاري رقم (٥)



Notes:

1. THE COPYRIGHT OF THIS DRAWING IS VESTED IN YOURSPREADSHEETS AND IT MAY NOT BE REPRODUCED IN WHOLE OR PART OR USED FOR THE MANUFACTURE OF ANY ARTICLE WITHOUT THE EXPRESS PERMISSION OF THE COPYRIGHT HOLDERS.
2. WORK TO DIMENSIONS ONLY.

Key plane

Before

Instructor :

YourSpreadsheets

Address line 1
Address line 2
Telephone line 1
Fax line 1
www.YourSpreadsheets.co.uk

CLIENT: BAH i CLIENT
3 Mossadak, Ad Doqi, Dokki,
Giza Governorate, Giza,
Egypt

ARCHITECT: Amr Mamdoh
40 Mossadak, Ad Doqi, Dokki,
Giza Governorate, Giza,
Egypt

SITE: 31 ROVER ROAD
BLOCK A AND B

TITLE: RC DETAILS AND SECTIONS
OF GROUND BEAMS

SCALE AT A2: 1:50, 1:100	DATE: 05/09/13	DRAWN: DJ	CHECKED: DJ
PROJECT NO: 24567	DRAWING NO: A2/248	REVISION: C	

الإستقطاعات

المبلغ المستقطع	النسبة - القيمة	بيان الأعمال
2078600	2078600	إجمالي الأعمال
103930	0.05	تأمين الأعمال
207860	0.1	دفعة مقدمة
311790	0.15	ضرائب وتأمينات
0	0	خصومات
1.165.383	1.165.383	السابق صرفة
1,455,020	الصافي المستحق بعد الإستقطاع	

مدير المشروع

مهندس الإستشاري

المدير المسنول

مهندس المشروع

مستخلص ختامي



Notes:

1. THE COPYRIGHT OF THIS DRAWING IS VESTED IN TOWERSPENCER AND IT MAY NOT BE REPRODUCED IN WHOLE OR PART OR USED FOR THE MANUFACTURE OF ANY ARTICLE WITHOUT THE EXPRESS PERMISSION OF THE COPYRIGHT HOLDERS.

2. WORK TO FIGURED DIMENSIONS ONLY.

2. WORK TO FIGURED DIMENSIONS ONLY.

Key plane

Before

Instructor:

YourSpreadsheets

Address line 1
Address line 2
Telephone line 1
Fax line 1
www.YourSpreadsheets.co.uk

CLIENT: **BAH i CLIENT**
3 Mossadak, Ad Doqi, Dokki,
Giza Governorate, Giza,
Egypt

ARCHITECT: Amr Mamdoh
40 Mossadak, Ad Doqi, Dokki
Giza Governorate, Giza,
Egypt

SITE: 31 ROVER ROAD
BLOCK A AND B

TITLE: RC DETAILS AND SECTIONS
OF GROUND BEAMS

SCALE AT A2: 1:50, 1:100	DATE: 05/09/13	DRAWN: DJ	CHECKED: DJ
PROJECT NO: 24567	DRAWING NO: A2/248	REVISION: C	

مستخلص أعمال : ختمامی

عن المدة من بداية الأعمال حتى تاريخ ٣٠ / يونيو / ٢٠٢٤

[illegible]

مستخلص ختامي

الإستقطاعات

المبلغ المستقطع	النسبة - القيمة	بيان الأعمال
2161100	2161100	إجمالي الأعمال
108055	0.05	تأمين الأعمال
216110	0.1	دفعة مقدمة
324165	0.15	ضرائب وتأمينات
0	0	خصومات
1.455.020	1.455.020	السابق صرفة
1,512,770	الصافي المستحق بعد الإستقطاع	



Notes:

1. THE COPYRIGHT OF THIS DRAWING IS VESTED IN YOURSPREADSHEETS AND IT MAY NOT BE REPRODUCED IN WHOLE OR PART OR USED FOR THE MANUFACTURE OF ANY ARTICLE WITHOUT THE EXPRESS PERMISSION OF THE COPYRIGHT HOLDERS.
2. WORK TO DIMENSIONS ONLY.

Key plane

Before

Instructor :

YourSpreadsheets

Address line 1
Address line 2
Telephone line 1
Fax line 1
www.YourSpreadsheets.co.uk

CLIENT: BAH i CLIENT
3 Mossadak, Ad Doqi, Dokki,
Giza Governorate, Giza,
Egypt

ARCHITECT: Amr Mamdoh
40 Mossadak, Ad Doqi, Dokki,
Giza Governorate, Giza,
Egypt

SITE: 31 ROVER ROAD
BLOCK A AND B

TITLE: RC DETAILS AND SECTIONS
OF GROUND BEAMS

SCALE AT A2: 1:50, 1:100	DATE: 05/09/13	DRAWN: DJ	CHECKED: DJ
PROJECT NO: 24567	DRAWING NO: A2/248	REVISION: C	

مدير المشروع

مهندس الإستشاري

المدير المسنول

مهندس المشروع

THE END

COURSE: TECHNICAL OFFICE G46

Name: Ibrahim Mohamed Read


Eng: Amr Mamdouh

Lecture: 15


Task: 11

Template على برنامج الـ AS


أولاً: الدخول على قائمة settings

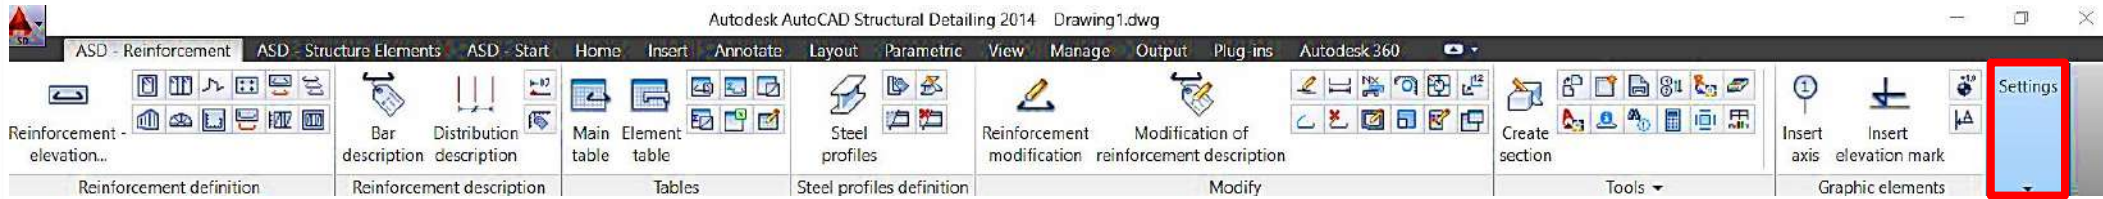

ثم اختيار قائمة Job Preferences

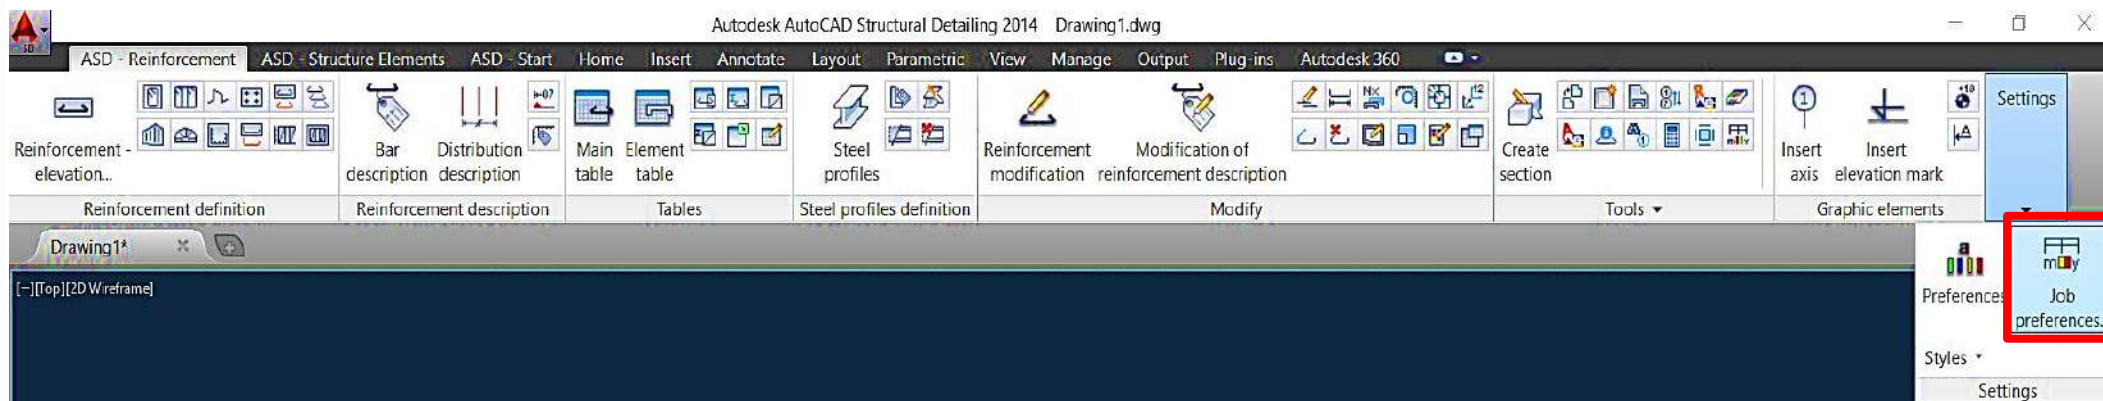

ثم اختيار قائمة Units والتعديل

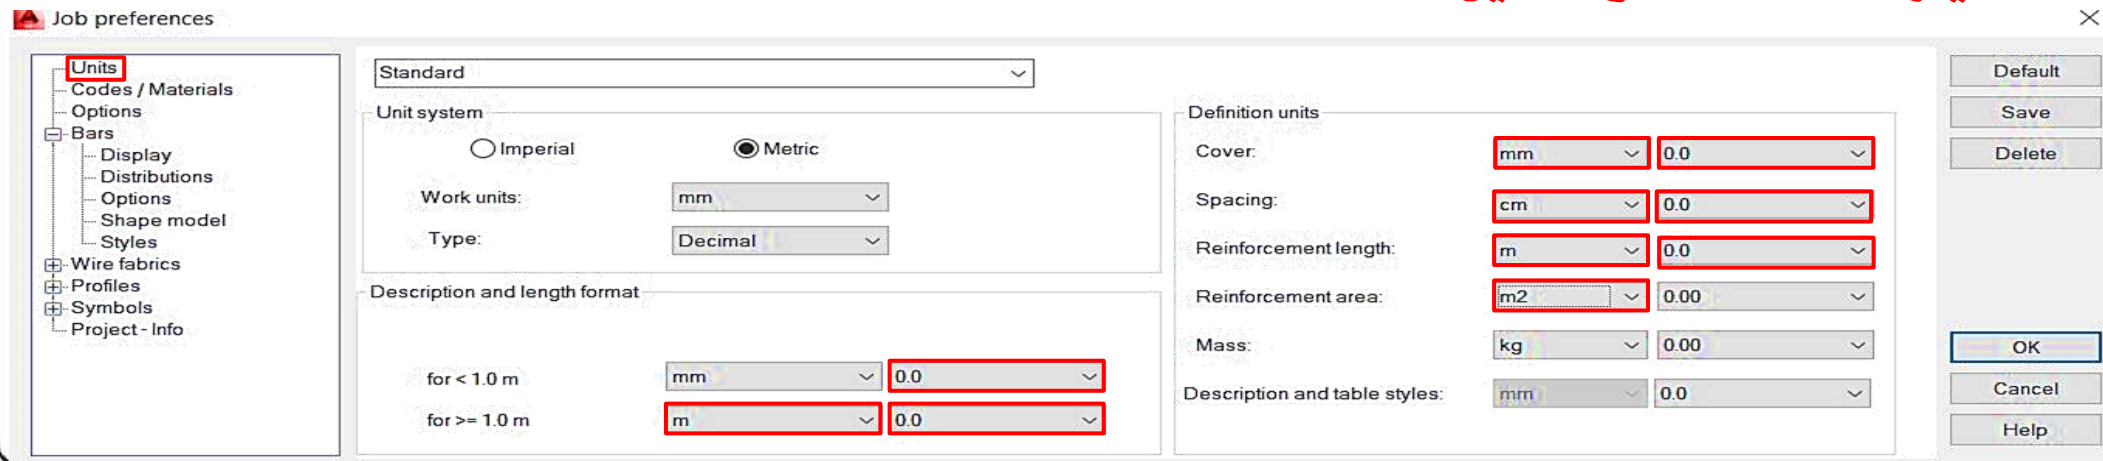

Notes:

1. THE COPYRIGHT OF THIS DRAWING IS VESTED IN YOURSPREADSHEETS AND IT MAY NOT BE REPRODUCED IN WHOLE OR PART OR USED FOR THE MANUFACTURE OF ANY ARTICLE WITHOUT THE EXPRESS PERMISSION OF THE COPYRIGHT HOLDERS.
2. WORK TO DIMENSIONED DIMENSIONS ONLY.

Key plane

Before

Instructor :

YourSpreadsheets

Address line 1
Address line 2
Telephone line 1
Fax line 1
www.YourSpreadsheets.co.uk

CLIENT: BAH I CLIENT
3 Mossadak, Ad Doqi, Dokki,
Giza Governorate, Giza,
Egypt

ARCHITECT: Amr Mamdoh
40 Mossadak, Ad Doqi, Dokki,
Giza Governorate, Giza,
Egypt

SITE: 31 ROVER ROAD
BLOCK A AND B

TITLE: RC DETAILS AND SECTIONS
OF GROUND BEAMS

SCALE AT A2: 1:50, 1:100
DATE: 05/09/13
DRAWN: DJ
PROJECT NO: 24567
DRAWING NO: A2/248
CHECKED: DJ
REVISION: C

Template على برنامج الـ AS

شخصية اختيار قائمة Codes Materials والتعديل



Job preferences

Units

Codes / Materials

Options

Bars

Display

Distributions

Options

Shape model

Styles

Wire fabrics

Profiles

Symbols

Project - Info

Codes

RC design: BS 8110 ☐ Seismic dispositions

Reinforcement (drawings): BS 8666:2005

Cover - long reinforcement: 25 [mm]

Cover - transversal reinforcement: 25 [mm]

Reinforcing bars

Database: bar_BS 8666_2000 - Copy

Lap splice:

Longitudinal:	Transversal:	Distributed:
60 x ∅	60 x ∅	60 x ∅

Steel grade	Symbol
R	∅
T	∅

Wire fabrics

Database: fabric_BS

Steel: B500A

Steel profiles

Database: RCAT

Material: STEEL 43-245

Default

Save

Delete

OK

Cancel

Help

Notes:

1. THE COPYRIGHT OF THIS DRAWING IS VESTED IN YOURSPREADSHEETS AND IT MAY NOT BE REPRODUCED IN WHOLE OR PART OR USED FOR THE MANUFACTURE OF ANY ARTICLE WITHOUT THE EXPRESS PERMISSION OF THE COPYRIGHT HOLDERS.

Key plane

Before

من قائمة Bars والدخول على خيار Display والتعديل

Job preferences

Units

Codes / Materials

Options

Bars

Display

Distributions

Options

Shape model

Styles

Wire fabrics

Profiles

Symbols

Project - Info

Bar shape

Color: Red ☒ Filled

Presentation: ☐ ☐ ☐

Line thickness: ByLayer

End of straight bars (without hooks) ☒ ☐ ☐

Bar symbol

Color: Magenta

Display: ☐ ☐ ☐

☐ Filled

Line thickness: ByLayer

Size: user-defined x 1.00

Added elements:

☐ detailed table

☒ chamfer dimensions/arc radius

☒ description of segment length

☐ bent diameter

☐ Angle (bent)

Bar - point

Symbol: ☐

Color: Red

Default

Save

Delete

OK

Cancel

Help

Instructor :

YourSpreadsheets

Address line 1
Address line 2
Telephone line 1
Fax line 1
www.YourSpreadsheets.co.uk

CLIENT: BAH i CLIENT
3 Mossadak, Ad Doqi, Dokki,
Giza Governorate, Giza,
Egypt

ARCHITECT: Amr Mamdoh
40 Mossadak, Ad Doqi, Dokki,
Giza Governorate, Giza,
Egypt

SITE: 31 ROVER ROAD
BLOCK A AND B

TITLE: RC DETAILS AND SECTIONS
OF GROUND BEAMS

SCALE AT AS:	DATE:	DRAWN:	CHECKED:
1:50, 1:100	05/09/13	DJ	DJ

PROJECT NO:	DRAWING NO:	REVISION:
24567	A2/248	C

Template على برنامج الـ AS

من قائمة Bars والدخول على خيار Distributions والتعديل

Job preferences

Units

Codes / Materials

Options

Bars

Display

Distributions

Options

Shape model

Styles

Wire fabrics

Profiles

Symbols

Project - Info

Surface distribution

Top reinforcement: ACAD_ISO03W

Bottom: ByLayer

Color: Red

Line thickness: ByLayer

Presentation: 

Linear distribution

Color: Red

Line thickness: 0.25 mm

Line style: ByBlock



☐ Filled

☐ Mark bar ends

Default

Save

Delete

OK

Cancel

Help

Notes:

1. THE COPYRIGHT OF THIS DRAWING IS VESTED IN YOURSIGNED AND IT MAY NOT BE REPRODUCED IN WHOLE OR PART OR USED FOR THE MANUFACTURE OF ANY ARTICLE WITHOUT THE EXPRESS PERMISSION OF THE COPYRIGHT HOLDERS.

2. WORK TO FIGURED DIMENSIONS ONLY.

Key plane

Before

من قائمة Bars والدخول على خيار Shape model والتعديل ثم الضغط Save ثم الضغط Ok

Job preferences

Units

Codes / Materials

Options

Bars

Display

Distributions

Options

Shape model

Styles

Wire fabrics

Profiles

Symbols

Project - Info

Reinforcement shape model display

According to :


☐ Reinforcement shape code

☒ Reinforcement shape

☐ Reinforcement shape type

Description :

Each shape model will comply with the reinforcement shape defined in the drawing regardless of the reinforcement definition method. All reinforcement shapes will have the shape model corresponding to reinforcement shape

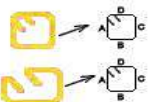

Hook length description

☒ All

☐ Standard

☐ Non-standard hooks



Reinforcement shape model behavior

In the description :

☐ Rotate shape symbol according to the model

☒ Automatically

Default

Save

Delete

OK

Cancel

Help

Instructor :

YourSpreadsheets

Address line 1

Address line 2

Telephone line 1

Fax line 1

www.YourSpreadsheets.co.uk

CLIENT: BAH i CLIENT

3 Mossadak, Ad Doqi, Dokki, Giza Governorate, Giza, Egypt

ARCHITECT: Amr Mamdoh

40 Mossadak, Ad Doqi, Dokki, Giza Governorate, Giza, Egypt

SITE: 31 ROVER ROAD BLOCK A AND B

TITLE: RC DETAILS AND SECTIONS OF GROUND BEAMS

SCALE AT A2: 1:50, 1:100

DATE: 05/09/13

DRAWN: DJ

CHECKED: DJ

PROJECT NO: 24567

DRAWING NO: A2/248

REVISION: C

Template على برنامج ال AS

الدخول على قائمة settings






Notes:

1. THE COPYRIGHT OF THIS DRAWING IS VESTED IN YOURSPREADSHEETS AND IT MAY NOT BE REPRODUCED IN WHOLE OR PART OR USED FOR THE MANUFACTURE OF ANY ARTICLE WITHOUT THE EXPRESS PERMISSION OF THE COPYRIGHT HOLDERS.
2. WORK TO DIMENSIONS ONLY.

Key plane

Before

ثم اختيار قائمة Styles ونختار منها Reinforcement description styles

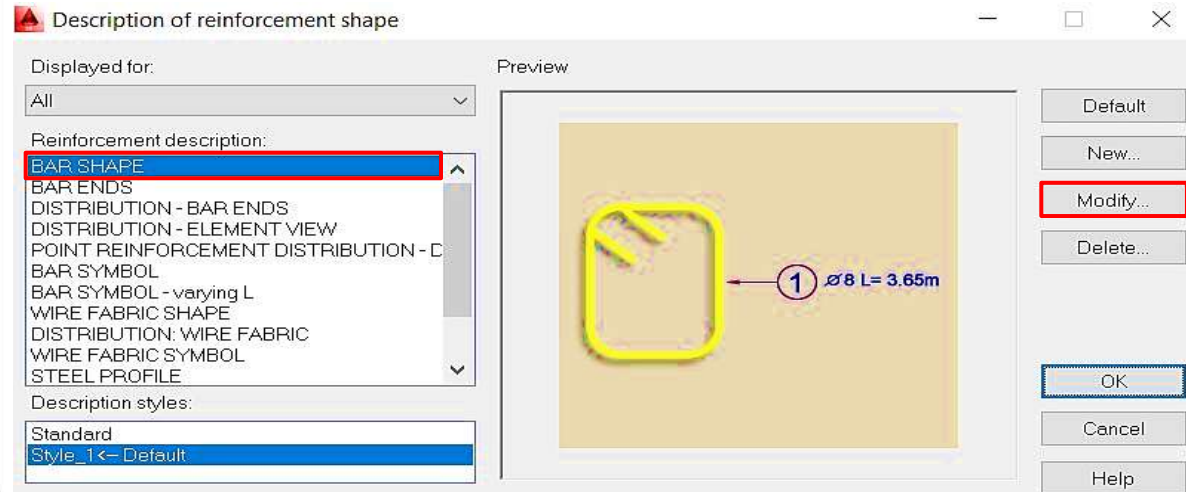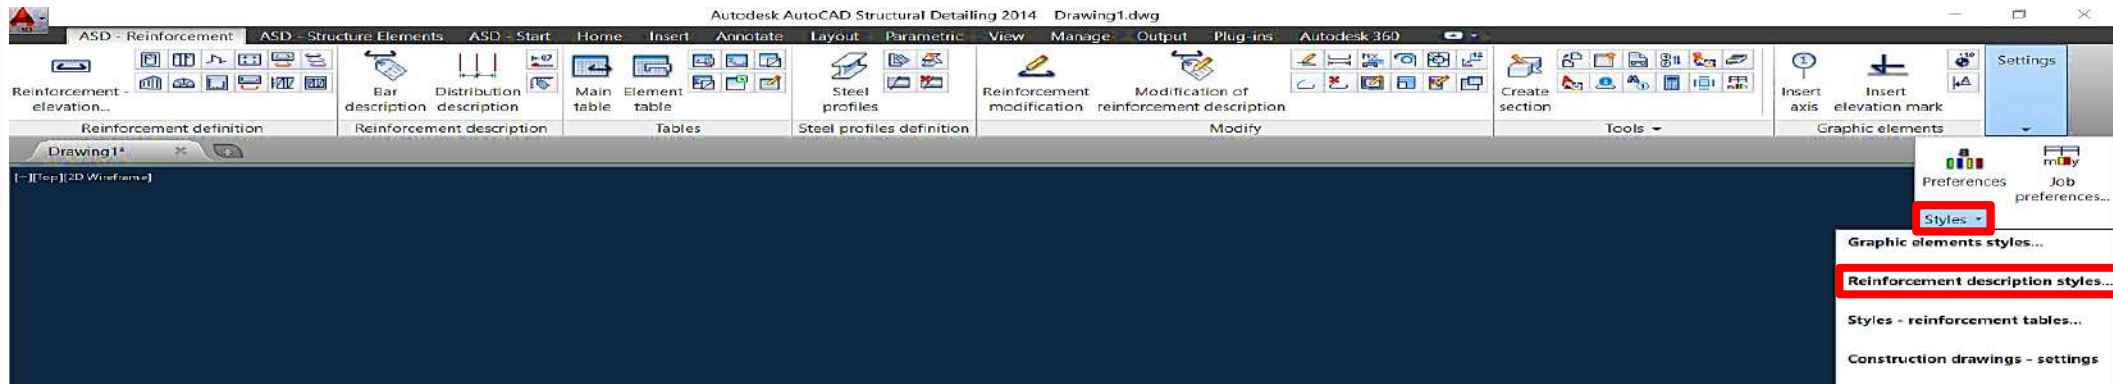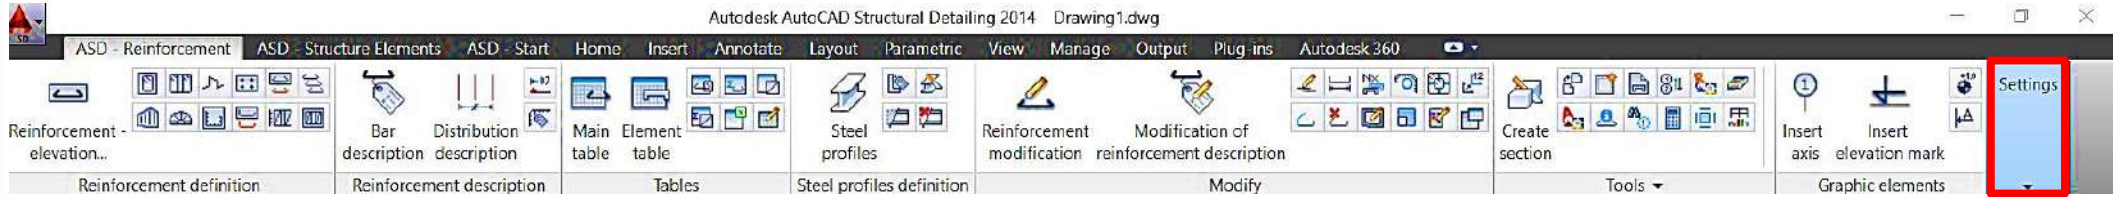

ثم اختيار قائمة BAR SHAPE
ثم الضغط على Modify

Instructor :

YourSpreadsheets

Address line 1
Address line 2
Telephone line 1
Fax line 1
www.YourSpreadsheets.co.uk

CLIENT: BAH i CLIENT
3 Mossadak, Ad Doqi, Dokki,
Giza Governorate, Giza,
Egypt

ARCHITECT: Amr Mamdoh
40 Mossadak, Ad Doqi, Dokki,
Giza Governorate, Giza,
Egypt

SITE: 31 ROVER ROAD
BLOCK A AND B

TITLE: RC DETAILS AND SECTIONS
OF GROUND BEAMS

SCALE AT AS: 1:50, 1:100	DATE: 05/09/13	DRAWN: DJ	CHECKED: DJ
PROJECT NO: 24567	DRAWING NO: A2/248	REVISION: C	

Template على برنامج الـ AS

شرح اختيار قائمة Description syntax والتعديل



Reinforcement description

Description elements Description syntax

Syntax elements

- | | |
|---|---|
| ☒ %num - number of reinforcing bars | ☒ %len - reinforcement length |
| ☒ %sym - diameter symbol | ☐ %lmin - min. reinforcement length |
| ☒ %dia - diameter | ☐ %lmax - max. reinforcement length |
| ☐ %pos - reinforcement position | ☐ %lmid - average reinforcement length |
| ☐ %spa - spacing | ☐ %dl - increment of reinf. length |
| ☐ %stl - reinforcing steel grade | ☐ %sch - reinforcement symbol |
| ☐ %des - User description | |
| ☐ %code - reinforcement code | |



Description:

☒ {%num}{%sym}{%dia} . L = {%len} ms

☐

Preview:

23#12.0000 . L = 3,7

Units and precision

Diameter:		0.1
Length:	m	0.1
Spacing:	cm	0.1

Style name:

Style_1

Add

Cancel

Help

Notes:

1. THE COPYRIGHT OF THIS DRAWING IS VESTED IN YOURSPREADSHEETS AND IT MAY NOT BE REPRODUCED IN WHOLE OR PART OR USED FOR THE MANUFACTURE OF ANY ARTICLE WITHOUT THE EXPRESS PERMISSION OF THE COPYRIGHT HOLDERS.
2. WORK TO FIGURED DIMENSIONS ONLY.

Key plane

Before

Instructor :

YourSpreadsheets

Address line 1
Address line 2
Telephone line 1
Fax line 1
www.YourSpreadsheets.co.uk

CLIENT: BAH i CLIENT
3 Mossadak, Ad Doqi, Dokki,
Giza Governorate, Giza,
Egypt

ARCHITECT: Amr Mamdoh
40 Mossadak, Ad Doqi, Dokki,
Giza Governorate, Giza,
Egypt

SITE: 31 ROVER ROAD
BLOCK A AND B

TITLE: RC DETAILS AND SECTIONS
OF GROUND BEAMS

SCALE AT A2: 1:50, 1:100	DATE: 05/09/13	DRAWN: DJ	CHECKED: DJ
PROJECT NO: 24567	DRAWING NO: A2/248	REVISION: C	

Template على برنامج الـ AS

تم اختيار قائمة Description elements والتعديل ثم الضغط على Add



Notes:

1. THE COPYRIGHT OF THIS DRAWING IS VESTED IN YOURSPREADSHEETS AND IT MAY NOT BE REPRODUCED IN WHOLE OR PART OR USED FOR THE MANUFACTURE OF ANY ARTICLE WITHOUT THE EXPRESS PERMISSION OF THE COPYRIGHT HOLDERS.
2. WORK TO FIGURED DIMENSIONS ONLY.

Key plane

Before

Instructor :

YourSpreadsheets

Address line 1
Address line 2
Telephone line 1
Fax line 1
www.YourSpreadsheets.co.uk

CLIENT: BAH i CLIENT
3 Mossadak, Ad Doqi, Dokki,
Giza Governorate, Giza,
Egypt

ARCHITECT: Amr Mamdoh
40 Mossadak, Ad Doqi, Dokki,
Giza Governorate, Giza,
Egypt

SITE: 31 ROVER ROAD
BLOCK A AND B

TITLE: RC DETAILS AND SECTIONS
OF GROUND BEAMS

SCALE AT AS: 1:50, 1:100	DATE: 05/09/13	DRAWN: DJ	CHECKED: DJ
PROJECT NO: 24567	DRAWING NO: A2/248	REVISION: C	

Reinforcement description

Description elements

Description syntax

Position

LABEL

Active: Red

Not active: Red

Line thickness: 0.00 mm

Shape: ① 1 1

Size: 5.0 [mm]

POSITION NO.

Position: Magenta

Not active: Magenta

Style: style1

Size: 3 [mm]

Description text appearance

Style: style1

Color: Yellow

Size: 2.5 [mm]

Position:

Distance: 1.0 [mm]

Auxiliary line

Color: Green

Thickness: 0.00 mm

Arrowhead: Oblique

Arrow size: 1.5 [mm]

Reinforcement shape model

Color: ByBlock

Thickness: 0.00 mm

Size: 10.0 [mm]

Distance: 5.0 [mm]

☒ Add dimensions for bar symbol

Size: 0.8 [mm]

Style name: Style_1

Add

Cancel

Help

Template على برنامج الـ AS

ثم اختيار قائمة DISTRIBUTION - ELEMENTVIEW ثم الضغط على Modify



Notes:

1. THE COPYRIGHT OF THIS DRAWING IS VESTED IN YOURSPREADSHEETS AND IT MAY NOT BE REPRODUCED IN WHOLE OR PART OR USED FOR THE MANUFACTURE OF ANY ARTICLE WITHOUT THE EXPRESS PERMISSION OF THE COPYRIGHT HOLDERS.
2. WORK TO DIMENSIONED DIMENSIONS ONLY.

Key plane

Before

Instructor :

YourSpreadsheets

Address line 1
Address line 2
Telephone line 1
Fax line 1
www.YourSpreadsheets.co.uk

CLIENT: BAH i CLIENT
3 Mossadak, Ad Doqi, Dokki,
Giza Governorate, Giza,
Egypt

ARCHITECT: Amr Mamdoh
40 Mossadak, Ad Doqi, Dokki,
Giza Governorate, Giza,
Egypt

SITE: 31 ROVER ROAD
BLOCK A AND B

TITLE: RC DETAILS AND SECTIONS
OF GROUND BEAMS

SCALE AT AS:	DATE:	DRAWN:	CHECKED:
1:50, 1:100	05/09/13	DJ	DJ
PROJECT NO:	DRAWING NO:	REVISION:	
24567	A2/248	C	

Description of reinforcement shape

Displayed for:
All

Reinforcement description:
BAR SHAPE
BAR ENDS
DISTRIBUTION - BAR ENDS
DISTRIBUTION - ELEMENT VIEW
POINT REINFORCEMENT DISTRIBUTION - C
BAR SYMBOL
BAR SYMBOL - varying L
WIRE FABRIC SHAPE
DISTRIBUTION: WIRE FABRIC
WIRE FABRIC SYMBOL
STEEL PROFILE

Description styles:
Standard
Style_1 ← Default

Preview

Default

New...

Modify...

Delete...

OK

Cancel

Help

Template على برنامج الـ AS

شرح اختيار قائمة Description syntax والتعديل



Reinforcement description



Notes:

1. THE COPYRIGHT OF THIS DRAWING IS VESTED IN YOURSPREADSHEETS AND IT MAY NOT BE REPRODUCED IN WHOLE OR PART OR USED FOR THE MANUFACTURE OF ANY ARTICLE WITHOUT THE EXPRESS PERMISSION OF THE COPYRIGHT HOLDERS.
2. WORK TO FIGURED DIMENSIONS ONLY.

Key plane

Before

Instructor :

YourSpreadsheets

Address line 1
Address line 2
Telephone line 1
Fax line 1
www.YourSpreadsheets.co.uk

CLIENT: BAH i CLIENT
3 Mossadak, Ad Doqi, Dokki,
Giza Governorate, Giza,
Egypt

ARCHITECT: Amr Mamdoh
40 Mossadak, Ad Doqi, Dokki,
Giza Governorate, Giza,
Egypt

SITE: 31 ROVER ROAD
BLOCK A AND B

TITLE: RC DETAILS AND SECTIONS
OF GROUND BEAMS

SCALE AT A2: 1:50, 1:100	DATE: 05/09/13	DRAWN: DJ	CHECKED: DJ
PROJECT NO: 24567	DRAWING NO: A2/248	REVISION: C	

Description elements Description syntax

Syntax elements

- | | |
|---|---|
| ☒ %num - number of reinforcing bars | ☒ %len - reinforcement length |
| ☒ %sym - diameter symbol | ☐ %lmin - min. reinforcement length |
| ☒ %dia - diameter | ☐ %lmax - max. reinforcement length |
| ☐ %pos - reinforcement position | ☐ %lmid - average reinforcement length |
| ☐ %spa - spacing | ☐ %dl - increment of reinf. length |
| ☐ %stl - reinforcing steel grade | ☐ %sch - reinforcement symbol |
| ☐ %des - User description | |
| ☐ %code - reinforcement code | |



Description:

☒ {%num}{%sym}{%dia} . L = {%len} ms

☐

Preview:

23#12.0000 . L = 3,7

Units and precision

Diameter:		0.1
Length:	m	0.1
Spacing:	cm	0.1

Style name:

Style_1

Add

Cancel

Help

ثم اختيار قائمة Description elements والتعديل



1. THE COPYRIGHT OF THIS DRAWING IS VESTED IN TONSORGESCHWARTZ AND
IT MAY NOT BE REPRODUCED IN WHOLE OR PART OR USED FOR THE
MANUFACTURE OF ANY ARTICLE WITHOUT THE EXPRESS PERMISSION OF
THE COPYRIGHT HOLDERS.

2. WORK TO FIGURED DIMENSIONS ONLY.

Before

Reinforcement description

Description elements | Description syntax

Position

Active: ■ Red

Not active: ■ Red

Line thickness: ——— 0.00 mm

Shape: ① 1 1

Size: 5.0 [mm]

POSITION NO.

Active: ■ Magenta

Not active: ■ Magenta

Style: style1

Size: 3.0 [mm]

Description text appearance

Style: style1

Color: ■ Yellow

Size: 2.5 [mm]

Position:

Distance: 1.0 [mm]

☐ Design of reinforcement spacing

- ☐ Dimensions at both line sides
- ☐ Grouping of spacings
- ☐ Add extreme dimensions to formwork edges

Extension line

Color: ■ Green

Thickness: ——— 0.00 mm

Marker: ☒ Oblique Closed fil

Marker size: 1.5 [mm]

0.0 [mm]

2.0 [mm]

☐ For all positions: 15.0 [mm]

Reinforcement shape model

Color: ☐ ByBlock

Thickness: ——— 0.00 mm

Size: 0.0 [mm]

Distance: 0.0 [mm]

☐ Add dimensions for bar symbol

Size: 0.0 [mm]

Style name: Style_1

Add
Cancel
Help

Template على برنامج الـ AS

من اختيار قائمة Description elements والتعديل



Notes:

1. THE COPYRIGHT OF THIS DRAWING IS VESTED IN TOWNSEND & BROWN AND IT MAY NOT BE REPRODUCED IN WHOLE OR PART OR USED FOR THE MANUFACTURE OF ANY ARTICLE WITHOUT THE EXPRESS PERMISSION OF THE COPYRIGHT HOLDERS.

2. WORK TO FIGURED DIMENSIONS ONLY.

Key plane

Before

Instructor :

YourSpreadsheets

Address line 1
Address line 2
Telephone line 1
Fax line 1
www.YourSpreadsheets.co.uk

CLIENT: **BAH i CLIENT**
3 Mossadak, Ad Doqi, Dokki,
Giza Governorate, Giza,
Egypt

ARCHITECT: Amr Mamdoh
40 Mossadak, Ad Doqi, Dokki,
Giza Governorate, Giza,
Egypt

SITE: 31 ROVER ROAD
BLOCK A AND B

TITLE	RC DETAILS AND SECTIONS OF GROUND BEAMS
-------	--

SCALE AT A2: 1:50, 1:100	DATE: 05/09/13	DRAWN: DJ	CHECKED: DJ
PROJECT NO: 24567	DRAWING NO: A2/248		REVISION: C

Reinforcement description

Description elements | Description syntax

Position	LABEL	POSITION NO.
Active:	☐ Red	Position:
Not active:	☐ Red	Active:
Line thickness:	— 0.00 mm	Not active:
Shape:	☒ ① ☐ [1] ☐ 1	Style:
Size:	5.0 [mm]	Size:

Description text appearance	Extension line	Reinforcement shape model
Style:	Color:	Color:
Color:	Thickness:	Thickness:
Size:	Marker:	Size:
Position:	Marker size:	Distance:
Distance:	☐ Distance to reinforcement:	☐ Add dimensions for bar symbol
☒ Design of reinforcement spacing	☐ For all positions:	Size:
☐ Dimensions at both line sides		
☒ Grouping of spacings		
☒ Add extreme dimensions to formwork edges		

Style name: Style_1

Add Cancel Help

Template على برنامج الـ AS

من اختيار قائمة Description elements والتعديل ثم الضغط على Add



Notes:

1. THE COPYRIGHT OF THIS DRAWING IS VESTED IN YOURSPREADSHEETS AND IT MAY NOT BE REPRODUCED IN WHOLE OR PART OR USED FOR THE MANUFACTURE OF ANY ARTICLE WITHOUT THE EXPRESS PERMISSION OF THE COPYRIGHT HOLDERS.
2. WORK TO DIMENSIONS ONLY.

Key plane

Before

Instructor :

YourSpreadsheets

Address line 1
Address line 2
Telephone line 1
Fax line 1
www.YourSpreadsheets.co.uk

CLIENT: BAH I CLIENT
3 Mossadak, Ad Doqi, Dokki,
Giza Governorate, Giza,
Egypt

ARCHITECT: Amr Mamdoh
40 Mossadak, Ad Doqi, Dokki,
Giza Governorate, Giza,
Egypt

SITE: 31 ROVER ROAD
BLOCK A AND B

TITLE: RC DETAILS AND SECTIONS
OF GROUND BEAMS

SCALE AT AS: 1:50, 1:100	DATE: 05/09/13	DRAWN: DJ	CHECKED: DJ
PROJECT NO: 24567	DRAWING NO: A2/248	REVISION: C	

Reinforcement description

Description elements

Description syntax

Position

LABEL

Active:

Red

Not active:

Red

Line thickness:

0.00 mm

Shape:

1

1

1

Size:

5.0

[mm]

POSITION NO.

Active:

Magenta

Not active:

Magenta

Style:

style1

Size:

3.0

[mm]

Description text appearance

Style:

style1

Color:

Yellow

Size:

2.5

[mm]

Position:

Distance:

1.0

[mm]

☒ Design of reinforcement spacing

☐ Dimensions at both line sides
 ☒ Grouping of spacings
 ☐ Add extreme dimensions to formwork edges

Extension line

Color:

Green

Thickness:

0.00 mm

Marker:

None

Dot

Marker size:

3.0

[mm]

2.0

[mm]

☐ Distance to reinforcement:

2.0

[mm]

☐ For all positions:

15.0

[mm]

Reinforcement shape model

Color:

ByBlock

Thickness:

0.00 mm

Size:

0.0

[mm]

Distance:

0.0

[mm]

☐ Add dimensions for bar symbol

Size:

0.0

[mm]


Style name:

Style_1

Add

Cancel

Help

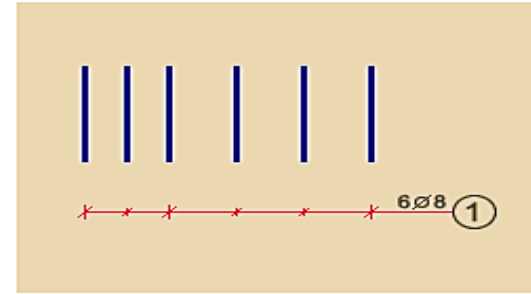

AS Template علی برنامه ال

ثم اختيار قائمة BAR SYMBOL ثم الضغط على Modify



Notes:

1. THE COPYRIGHT OF THIS DRAWING IS VESTED IN TOWNSPOONSHAW AND IT MAY NOT BE REPRODUCED IN WHOLE OR PART OR USED FOR THE MANUFACTURE OF ANY ARTICLE WITHOUT THE EXPRESS PERMISSION OF THE COPYRIGHT HOLDERS.

2. WORK TO FIGURED DIMENSIONS ONLY.

Key plane

Before

Default

New...

Modify...

Delete...

OK

Cancel

Help

Instructor :

YourSpreadsheets

Address line 1
Address line 2
Telephone line 1
Fax line 1
www.YourSpreadsheets.co.uk

CLIENT: **BAH i CLIENT**
3 Mossadak, Ad Doqi, Dokki,
Giza Governorate, Giza,
Egypt

ARCHITECT: Amr Mamdoh
40 Mossadak, Ad Doqi, Dokki,
Giza Governorate, Giza,
Egypt

SITE: 31 ROVER ROAD
BLOCK A AND B

TITLE:	RC DETAILS AND SECTIONS OF GROUND BEAMS
--------	--

SCALE AT A2: 1:50, 1:100	DATE: 05/09/13	DRAWN: DJ	CHECKED: DJ
PROJECT NO: 24567	DRAWING NO: A2/248		REVISION: C

Template على برنامج الـ AS

شرح اختيار قائمة Description syntax والتعديل



Notes:

1. THE COPYRIGHT OF THIS DRAWING IS VESTED IN YOURSPREADSHEETS AND IT MAY NOT BE REPRODUCED IN WHOLE OR PART OR USED FOR THE MANUFACTURE OF ANY ARTICLE WITHOUT THE EXPRESS PERMISSION OF THE COPYRIGHT HOLDERS.
2. WORK TO FIGURED DIMENSIONS ONLY.

Key plane

Before

Instructor :

YourSpreadsheets

Address line 1
Address line 2
Telephone line 1
Fax line 1
www.YourSpreadsheets.co.uk

CLIENT: BAH i CLIENT
3 Mossadak, Ad Doqi, Dokki,
Giza Governorate, Giza,
Egypt

ARCHITECT: Amr Mamdoh
40 Mossadak, Ad Doqi, Dokki,
Giza Governorate, Giza,
Egypt

SITE: 31 ROVER ROAD
BLOCK A AND B

TITLE: RC DETAILS AND SECTIONS
OF GROUND BEAMS

SCALE AT A2: 1:50, 1:100	DATE: 05/09/13	DRAWN: DJ	CHECKED: DJ
PROJECT NO: 24567	DRAWING NO: A2/248	REVISION: C	



Reinforcement description

Description elements Description syntax

Syntax elements

- | | |
|---|---|
| ☒ %num - number of reinforcing bars | ☒ %len - reinforcement length |
| ☒ %sym - diameter symbol | ☐ %lmin - min. reinforcement length |
| ☒ %dia - diameter | ☐ %lmax - max. reinforcement length |
| ☐ %pos - reinforcement position | ☐ %lmid - average reinforcement length |
| ☐ %spa - spacing | ☐ %dl - increment of reinf. length |
| ☐ %stl - reinforcing steel grade | ☐ %sch - reinforcement symbol |
| ☐ %des - User description | |
| ☐ %code - reinforcement code | |



Description:

☒ {%num}{%sym}{%dia} . L = {%len} ms

☐

Preview:

23#12.0000 . L = 3,7

Units and precision

Diameter:		0.1
Length:	m	0.1
Spacing:	cm	0.1

Style name:

Style_1

Add

Cancel

Help

Template على برنامج الـ AS

من اختيار قائمة Description elements والتعديل ثم الضغط على Add



Notes:

1. THE COPYRIGHT OF THIS DRAWING IS VESTED IN YOURSPREADSHEETS AND IT MAY NOT BE REPRODUCED IN WHOLE OR PART OR USED FOR THE MANUFACTURE OF ANY ARTICLE WITHOUT THE EXPRESS PERMISSION OF THE COPYRIGHT HOLDERS.
2. WORK TO DIMENSIONS ONLY.

Key plane

Before

Instructor :

YourSpreadsheets

Address line 1
Address line 2
Telephone line 1
Fax line 1
www.YourSpreadsheets.co.uk

CLIENT: BAH i CLIENT
3 Mossadak, Ad Doqi, Dokki,
Giza Governorate, Giza,
Egypt

ARCHITECT: Amr Mamdoh
40 Mossadak, Ad Doqi, Dokki,
Giza Governorate, Giza,
Egypt

SITE: 31 ROVER ROAD
BLOCK A AND B

TITLE: RC DETAILS AND SECTIONS
OF GROUND BEAMS

SCALE AT A2: 1:50, 1:100	DATE: 05/09/13	DRAWN: DJ	CHECKED: DJ
PROJECT NO: 24567	DRAWING NO: A2/248	REVISION: C	

Reinforcement description

Description elements

Description syntax

Position

Color:

Red

Line thickness:

0.00 mm

Shape:

①

1

1

Size:

5.0

 [mm]

Style:

Standard

Color:

Magenta

Size:

3

 [mm]

Description of leg length

Style:

style1

Color:

Yellow

Size:

2.0

 [mm]

Location:

1.0

 [mm]

Description text appearance

Style:

style1

Color:

Yellow

Size:

2.5

 [mm]

Location:

1.0

 [mm]

Style name:

Style_1


Add

Cancel



Help

Template على برنامج الـ AS

الدخول على قائمة settings

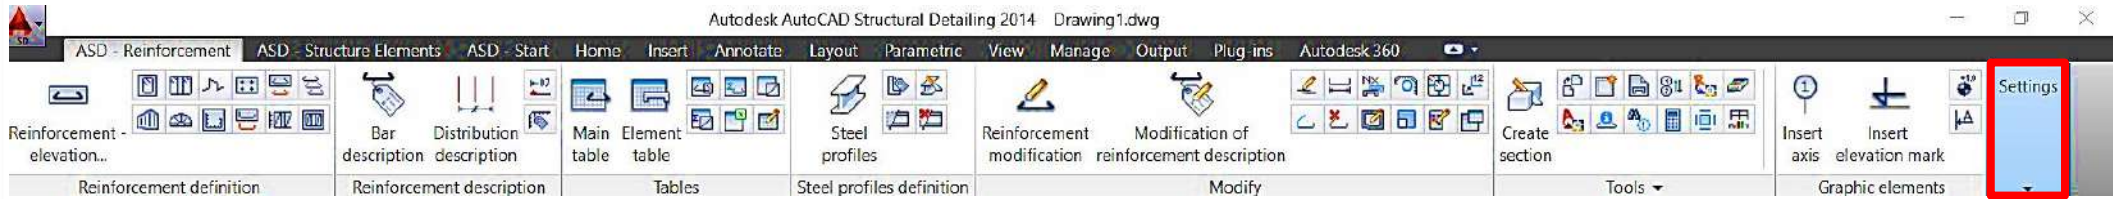

ثم اختيار قائمة Styles ونختار منها styles Reinforcement Tables

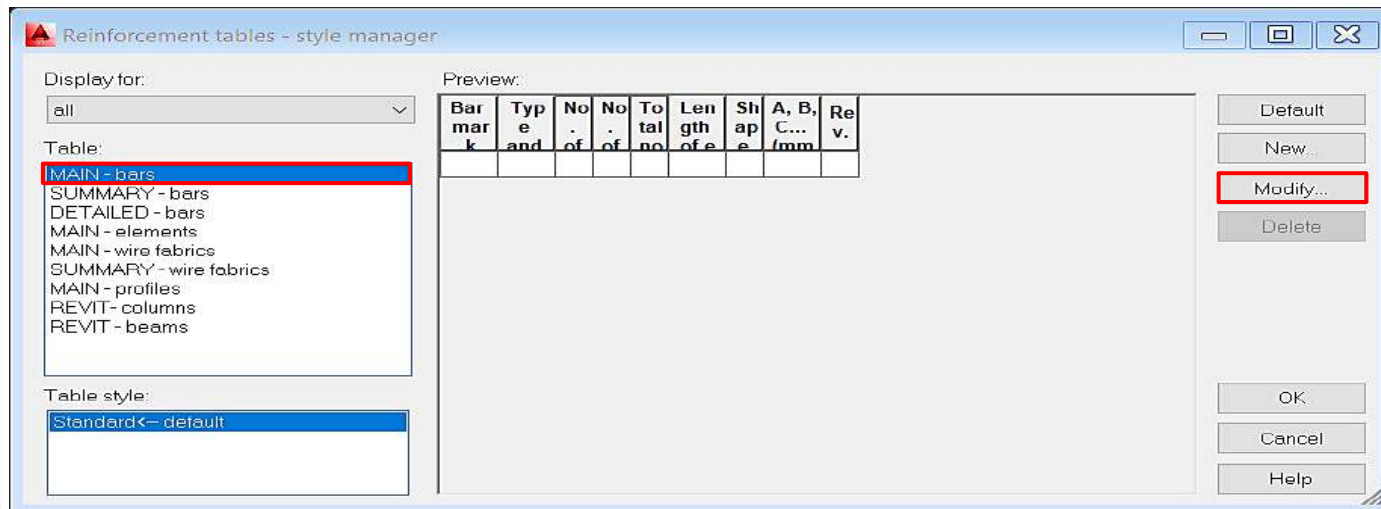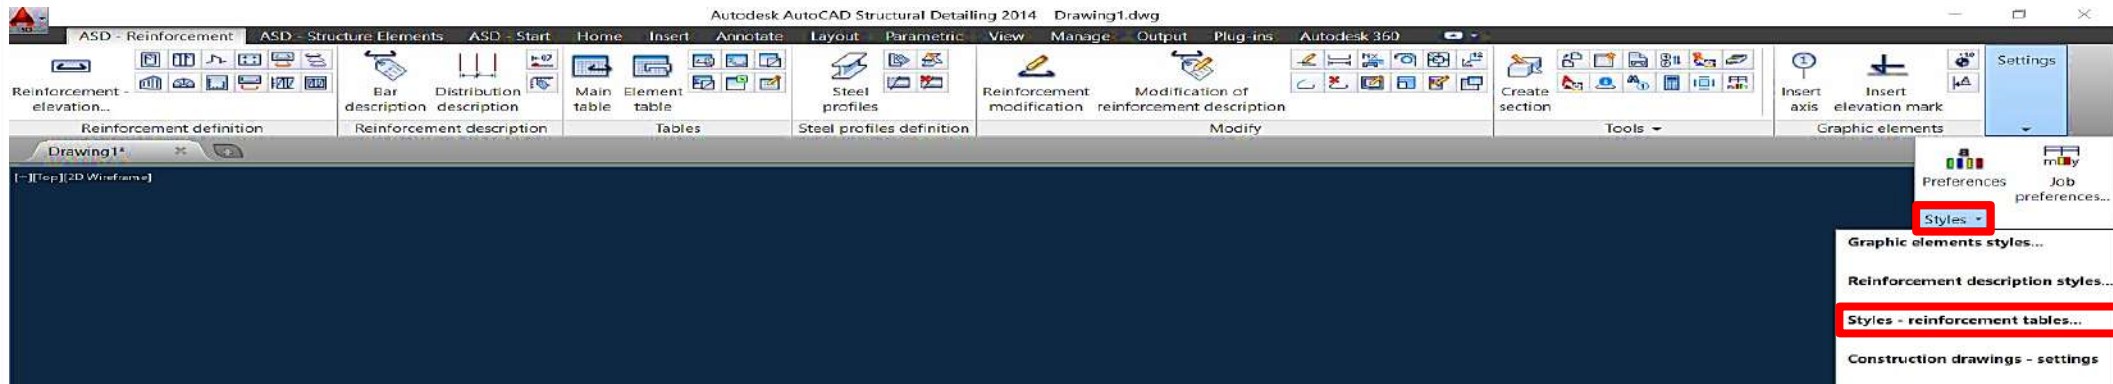

ثم اختيار قائمة MAIN – bars ونضغط علي Modify



Notes:

1. THE COPYRIGHT OF THIS DRAWING IS VESTED IN YOURSPREADSHEETS AND IT MAY NOT BE REPRODUCED IN WHOLE OR PART OR USED FOR THE MANUFACTURE OF ANY ARTICLE WITHOUT THE EXPRESS PERMISSION OF THE COPYRIGHT HOLDERS.
2. WORK TO DIMENSIONS ONLY.

Key plane

Before

Instructor :

YourSpreadsheets

Address line 1
Address line 2
Telephone line 1
Fax line 1
www.YourSpreadsheets.co.uk

CLIENT: BAH I CLIENT
3 Mossadak, Ad Doqi, Dokki,
Giza Governorate, Giza,
Egypt

ARCHITECT: Amr Mamdoh
40 Mossadak, Ad Doqi, Dokki,
Giza Governorate, Giza,
Egypt

SITE: 31 ROVER ROAD
BLOCK A AND B

TITLE: RC DETAILS AND SECTIONS
OF GROUND BEAMS

SCALE AT A2: 1:50, 1:100	DATE: 05/09/13	DRAWN: DJ	CHECKED: DJ
PROJECT NO: 24567	DRAWING NO: A2/248	REVISION: C	

Template على برنامج الـ AS

ثم اختيار قائمة Table: components and layout والتعديل



Notes:

1. THE COPYRIGHT OF THIS DRAWING IS VESTED IN YOURSPREADSHEETS AND IT MAY NOT BE REPRODUCED IN WHOLE OR PART OR USED FOR THE MANUFACTURE OF ANY ARTICLE WITHOUT THE EXPRESS PERMISSION OF THE COPYRIGHT HOLDERS.
2. WORK TO DIMENSIONS ONLY.

Key plane

Before

Modification of reinforcement table style

Table: components and layout | Font, color, line... | Sorting and detailed options | Options

MAIN
QUANTITIES
LENGTHS
SUMS

☒ Position no.
☐ Steel grade
☒ Diameter
☐ Diameter (according to steel g...
☐ Spacing
☒ Bar shape symbol
☐ Bar shape code
☐ Dimensions of bends
☐ Name - summary
☐ Bent diameters
☐ Bar mass
☐ Mass of a single bar
☐ Remarks
☐ Angle (bent)
☒ Total mass
☐ Revision
☐ Hooks
☐ Diameter symbol

Units: [mm] [0]

List of styles: Standard<-- default

Total table width: 155.0 [mm]

20.0	Posi tion	Dia meter	in the elem ents	of elem ents	Sym bol (mm)	Len gth (mm)	Total mass (kg)
20.0							
20.0		20.0	20.0	20.0	20.0	20.0	35.0

Modification of reinforcement table style

Table: components and layout | Font, color, line... | Sorting and detailed options | Options

MAIN
QUANTITIES
LENGTHS
SUMS

☒ Bars in the element
☒ of elements
☐ Total

Units: [mm] [0]

List of styles: Standard<-- default

Total table width: 155.0 [mm]

20.0	Posi tion	Dia meter	in the elem ents	of elem ents	Sym bol (mm)	Len gth (mm)	Total mass (kg)
20.0							
20.0		20.0	20.0	20.0	20.0	20.0	35.0

Modification of reinforcement table style

Table: components and layout | Font, color, line... | Sorting and detailed options | Options

MAIN
QUANTITIES
LENGTHS
SUMS

☐ Subtotal by steel grade
☐ Subtotal by diameter
☒ Bar
☐ Total (bar)

Units: mm [0]

List of styles: Standard<-- default

Total table width: 155.0 [mm]

20.0	Posi tion	Dia meter	in the elem ents	of elem ents	Sym bol (mm)	Len gth (mm)	Total mass (kg)
20.0							
20.0		20.0	20.0	20.0	20.0	20.0	35.0

Modification of reinforcement table style

Table: components and layout | Font, color, line... | Sorting and detailed options | Options

MAIN
QUANTITIES
LENGTHS
SUMS

☐ Length
☐ Unit mass of a bar
☐ Subtotal by diameter
☐ Subtotal by steel grade
☐ Total

Units: mm [0]

List of styles: Standard<-- default

Total table width: 155.0 [mm]

20.0	Posi tion	Dia meter	in the elem ents	of elem ents	Sym bol (mm)	Len gth (mm)	Total mass (kg)
20.0							
20.0		20.0	20.0	20.0	20.0	20.0	35.0

Instructor :

YourSpreadsheets

Address line 1
Address line 2
Telephone line 1
Fax line 1
www.YourSpreadsheets.co.uk

CLIENT: BAH I CLIENT
3 Mossadak, Ad Doqi, Dokki,
Giza Governorate, Giza,
Egypt

ARCHITECT: Amr Mamdoh
40 Mossadak, Ad Doqi, Dokki,
Giza Governorate, Giza,
Egypt

SITE: 31 ROVER ROAD
BLOCK A AND B

TITLE: RC DETAILS AND SECTIONS
OF GROUND BEAMS

SCALE AT A2: 1:50, 1:100
DATE: 05/09/13
DRAWN: DJ
PROJECT NO: 24567
DRAWING NO: A2/248
CHECKED: DJ
REVISION: C

Template على برنامج الـ AS

ثم اختيار قائمة Option والتعديل ثم الضغط على Ok



Notes:

1. THE COPYRIGHT OF THIS DRAWING IS VESTED IN YOURSPREADSHEETS AND IT MAY NOT BE REPRODUCED IN WHOLE OR PART OR USED FOR THE MANUFACTURE OF ANY ARTICLE WITHOUT THE EXPRESS PERMISSION OF THE COPYRIGHT HOLDERS.
2. WORK TO PROVIDED DIMENSIONS ONLY.

Key plane

Before

Instructor :

YourSpreadsheets

Address line 1
Address line 2
Telephone line 1
Fax line 1
www.YourSpreadsheets.co.uk

CLIENT: BAH i CLIENT
3 Mossadak, Ad Doqi, Dokki,
Giza Governorate, Giza,
Egypt

ARCHITECT: Amr Mamdoh
40 Mossadak, Ad Doqi, Dokki,
Giza Governorate, Giza,
Egypt

SITE: 31 ROVER ROAD
BLOCK A AND B

TITLE: RC DETAILS AND SECTIONS
OF GROUND BEAMS

SCALE AT A2: 1:50, 1:100	DATE: 05/09/13	DRAWN: DJ	CHECKED: DJ
PROJECT NO: 24567	DRAWING NO: A2/248	REVISION: C	



Modification of reinforcement table style

Table: components and layout Font color, line... Sorting and detailed options Options

Options

- ☐ Automatically adjust row height
- ☒ Autoadjust column width in the printout manager
- ☐ Table without heading
- ☐ Number of reinforcement position in label
- ☐ Hide horizontal table lines
- ☐ Hide vertical table lines
- ☒ Table with title

B.B.S

Zoom out

Zoom in

100 %

Fit

OK

Cancel

Help

List of styles:

Standard<- default

Total table width:

155.0

[mm]

Template على برنامج الـ AS

شماره اختيار قائمة bars - SUMMARY ونضغط على Modify



Notes:

1. THE COPYRIGHT OF THIS DRAWING IS VESTED IN YOURSPREADSHEETS AND IT MAY NOT BE REPRODUCED IN WHOLE OR PART OR USED FOR THE MANUFACTURE OF ANY ARTICLE WITHOUT THE EXPRESS PERMISSION OF THE COPYRIGHT HOLDERS.
2. WORK TO DIMENSIONS ONLY.

Key plane

Before

Instructor :

YourSpreadsheets

Address line 1
Address line 2
Telephone line 1
Fax line 1
www.YourSpreadsheets.co.uk

CLIENT: BAHIG CLIENT
3 Mossadak, Ad Doqi, Dokki,
Giza Governorate, Giza,
Egypt

ARCHITECT: Amr Mamdoh
40 Mossadak, Ad Doqi, Dokki,
Giza Governorate, Giza,
Egypt

SITE: 31 ROVER ROAD
BLOCK A AND B

TITLE: RC DETAILS AND SECTIONS
OF GROUND BEAMS

SCALE AT AS: 1:50, 1:100	DATE: 05/09/13	DRAWN: DJ	CHECKED: DJ
PROJECT NO: 24567	DRAWING NO: A2/248	REVISION: C	



Reinforcement tables - style manager

Display for:

all

Table:

MAIN - bars
SUMMARY - bars
DETAILED - bars
MAIN - elements
MAIN - wire fabrics
SUMMARY - wire fabrics
MAIN - profiles
REVIT - columns
REVIT - beams

Table style:

Standard<- default

Preview:

Steel grade 1	# 1	...	# n
Unit weight (kg)			
Total length (mm)			
Total weight (kg)			
.....	# 1	...	# n
Unit weight (kg)			
Total length (mm)			
Total weight (kg)			
Steel grade n	# 1	...	# n
Unit weight (kg)			
Total length (mm)			
Total weight (kg)			

Default

New...

Modify...

Delete

OK

Cancel

Help

Template على برنامج الـ AS

ثم اختيار قائمة Option والتعديل ثم الضغط على Ok



Notes:

1. THE COPYRIGHT OF THIS DRAWING IS VESTED IN YOURSPREADSHEETS AND IT MAY NOT BE REPRODUCED IN WHOLE OR PART OR USED FOR THE MANUFACTURE OF ANY ARTICLE WITHOUT THE EXPRESS PERMISSION OF THE COPYRIGHT HOLDERS.
2. WORK TO PROVIDED DIMENSIONS ONLY.

Key plane

Before

Instructor :

YourSpreadsheets

Address line 1
Address line 2
Telephone line 1
Fax line 1
www.YourSpreadsheets.co.uk

CLIENT: BAH i CLIENT
3 Mossadak, Ad Doqi, Dokki,
Giza Governorate, Giza,
Egypt

ARCHITECT: Amr Mamdoh
40 Mossadak, Ad Doqi, Dokki,
Giza Governorate, Giza,
Egypt

SITE: 31 ROVER ROAD
BLOCK A AND B

TITLE: RC DETAILS AND SECTIONS
OF GROUND BEAMS

SCALE AT A2: 1:50, 1:100	DATE: 05/09/13	DRAWN: DJ	CHECKED: DJ
PROJECT NO: 24567	DRAWING NO: A2/248	REVISION: C	



Modification of reinforcement table style

Table: components and layout Font color, line... Sorting and detailed options Options

Options

- ☐ Automatically adjust row height
- ☒ Autoadjust column width in the printout manager
- ☐ Table without heading
- ☐ Number of reinforcement position in label
- ☐ Hide horizontal table lines
- ☐ Hide vertical table lines
- ☒ Table with title

B.B.S

Zoom out

Zoom in

100 %

Fit

OK

Cancel

Help

List of styles:

Standard<- default


Total table width:

155.0



[mm]

Template على برنامج الـ AS

الدخول على قائمة settings

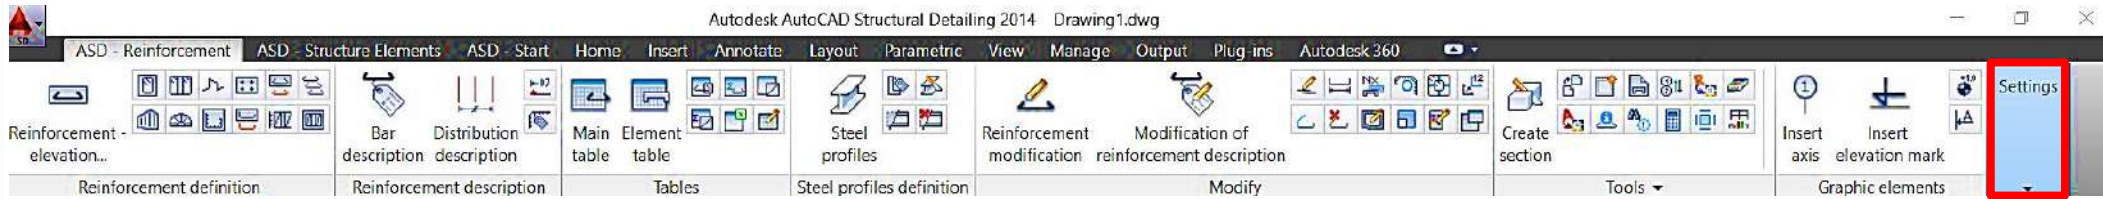

ثم اختيار قائمة Styles ونختار منها Graphic elements styles

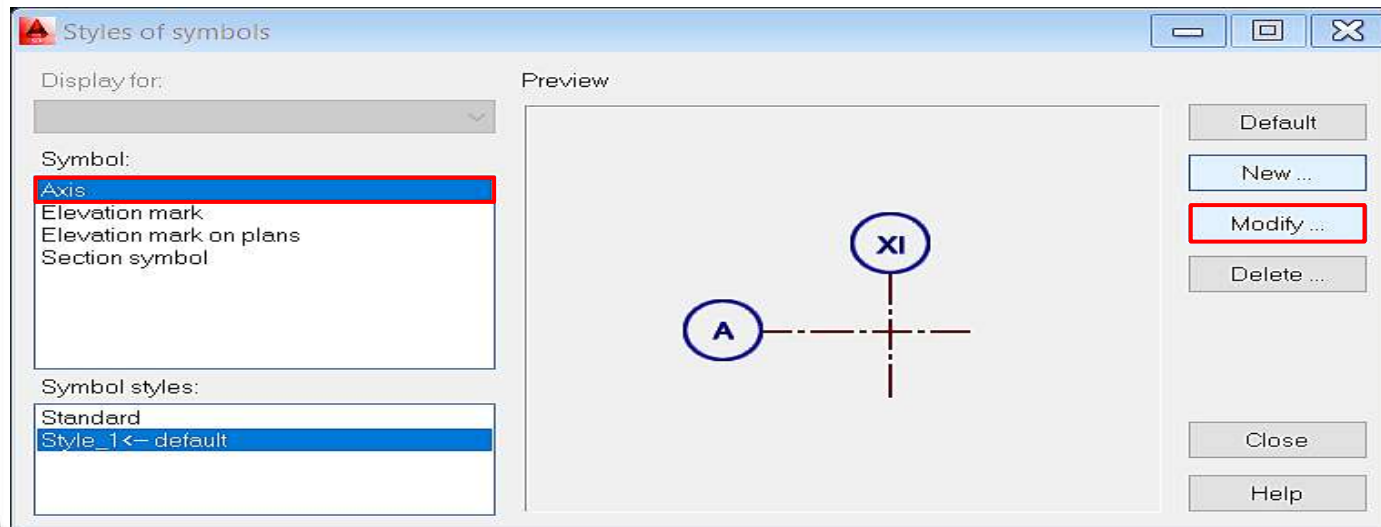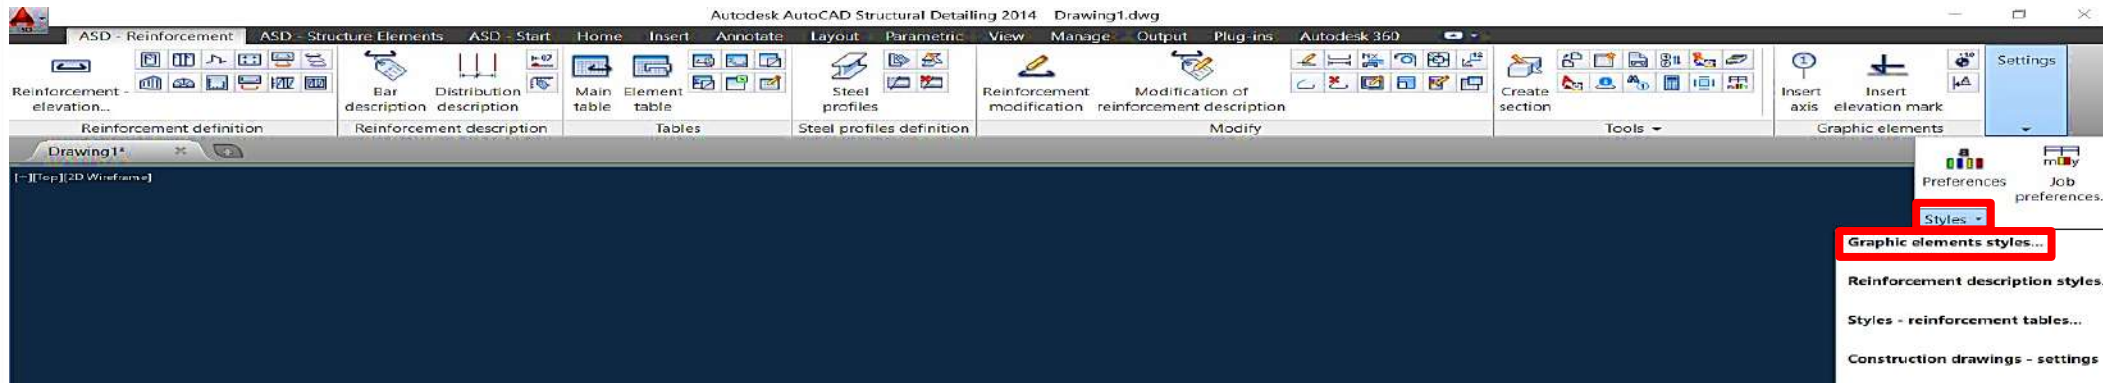

ثم اختيار قائمة Axis ونضغط علي Modify



Notes:

1. THE COPYRIGHT OF THIS DRAWING IS VESTED IN YOURSPREADSHEETS AND IT MAY NOT BE REPRODUCED IN WHOLE OR PART OR USED FOR THE MANUFACTURE OF ANY ARTICLE WITHOUT THE EXPRESS PERMISSION OF THE COPYRIGHT HOLDERS.
2. WORK TO DIMENSIONS ONLY.

Key plane

Before

Instructor :

YourSpreadsheets

Address line 1
Address line 2
Telephone line 1
Fax line 1
www.YourSpreadsheets.co.uk

CLIENT: BAH i CUENT
3 Mossadak, Ad Doqi, Dokki,
Giza Governorate, Giza,
Egypt

ARCHITECT: Amr Mamdoh
40 Mossadak, Ad Doqi, Dokki,
Giza Governorate, Giza,
Egypt

SITE: 31 ROVER ROAD
BLOCK A AND B

TITLE: RC DETAILS AND SECTIONS
OF GROUND BEAMS

SCALE AT AS: 1:50, 1:100	DATE: 05/09/13	DRAWN: DJ	CHECKED: DJ
PROJECT NO: 24567	DRAWING NO: A2/248	REVISION: C	

Template على برنامج الـ AS

ثم التعديل على قائمة Axis



Notes:

1. THE COPYRIGHT OF THIS DRAWING IS VESTED IN YOURSPREADSHEETS AND IT MAY NOT BE REPRODUCED IN WHOLE OR PART OR USED FOR THE MANUFACTURE OF ANY ARTICLE WITHOUT THE EXPRESS PERMISSION OF THE COPYRIGHT HOLDERS.
2. WORK TO FIGURED DIMENSIONS ONLY.

Key plane

Before

Instructor :

YourSpreadsheets

Address line 1
Address line 2
Telephone line 1
Fax line 1
www.YourSpreadsheets.co.uk

CLIENT: BAH I CLIENT
3 Mossadak, Ad Doqi, Dokki,
Giza Governorate, Giza,
Egypt

ARCHITECT: Amr Mamdoh
40 Mossadak, Ad Doqi, Dokki,
Giza Governorate, Giza,
Egypt

SITE: 31 ROVER ROAD
BLOCK A AND B

TITLE: RC DETAILS AND SECTIONS
OF GROUND BEAMS

SCALE AT A2: 1:50, 1:100	DATE: 05/09/13	DRAWN: DJ	CHECKED: DJ
PROJECT NO: 24567	DRAWING NO: A2/248	REVISION: C	

Axis

Axis

Line type: CENTER

Color: Red

Thickness: 0.00 mm

Label

Shape:

Size: 5.0000 [mm]

Color: Red

Line thickness: 0.00 mm

☒

Style name: Style_1

Text

Style: style1

Color: Magenta

Size: 3.0000 [mm]

Prefix:

Numbering: 1,2,3...


Index:

Add


Cancel

Help

Template على برنامج الـ AS

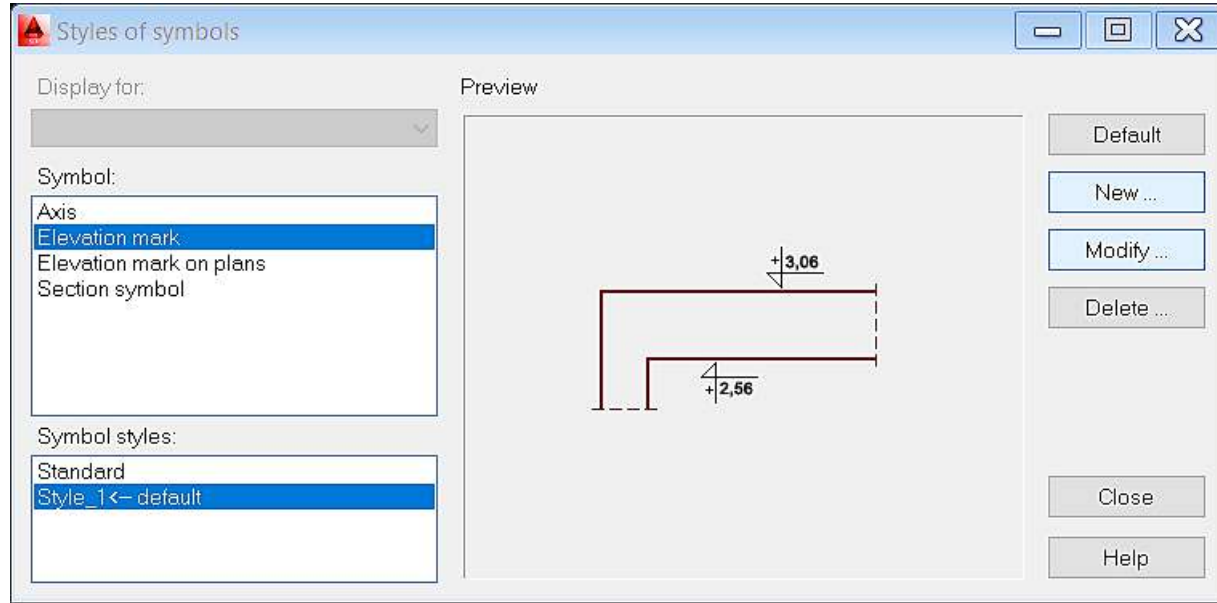

ثم اختيار قائمة Elevation mark
ونضغط على Modify

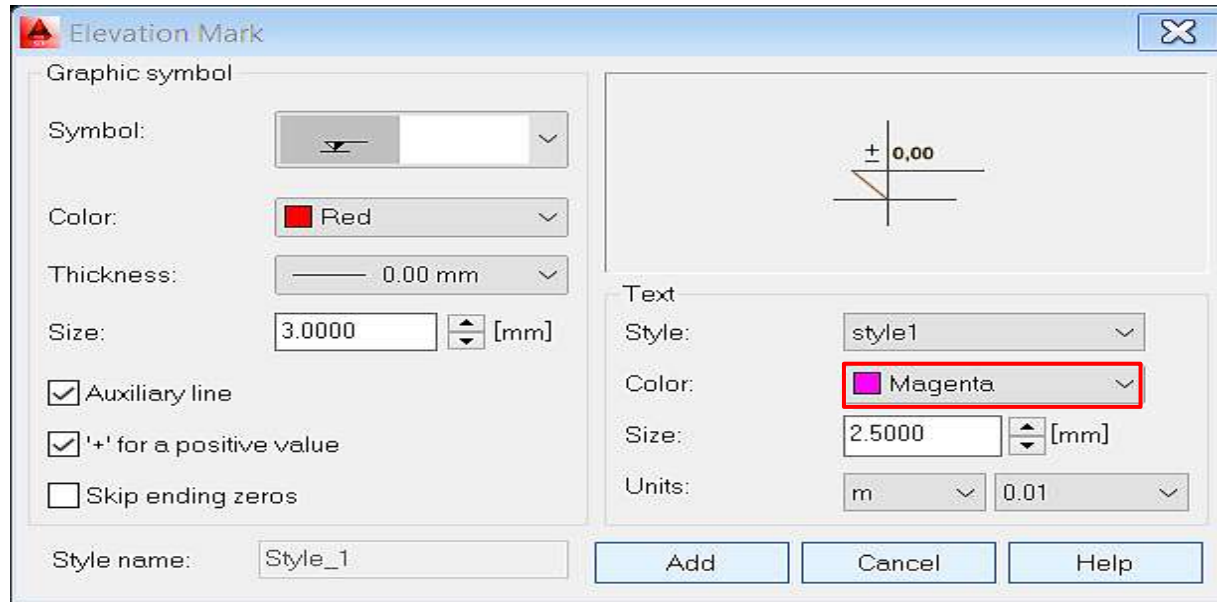

ثم التعديل على قائمة Elevation mark



Notes:

1. THE COPYRIGHT OF THIS DRAWING IS VESTED IN YOURSPREADSHEETS AND IT MAY NOT BE REPRODUCED IN WHOLE OR PART OR USED FOR THE MANUFACTURE OF ANY ARTICLE WITHOUT THE EXPRESS PERMISSION OF THE COPYRIGHT HOLDERS.
2. WORK TO DIMENSIONS ONLY.

Key plane

Before

Instructor :

YourSpreadsheets

Address line 1
Address line 2
Telephone line 1
Fax line 1
www.YourSpreadsheets.co.uk

CLIENT: BAH i CLIENT
3 Mossadak, Ad Doqi, Dokki,
Giza Governorate, Giza,
Egypt


ARCHITECT: Amr Mamdoh
40 Mossadak, Ad Doqi, Dokki,
Giza Governorate, Giza,
Egypt

SITE: 31 ROVER ROAD
BLOCK A AND B


TITLE: RC DETAILS AND SECTIONS
OF GROUND BEAMS

SCALE AT A2: 1:50, 1:100	DATE: 05/09/13	DRAWN: DJ	CHECKED: DJ
PROJECT NO: 24567	DRAWING NO: A2/248	REVISION: C	

Template على برنامج الـ AS

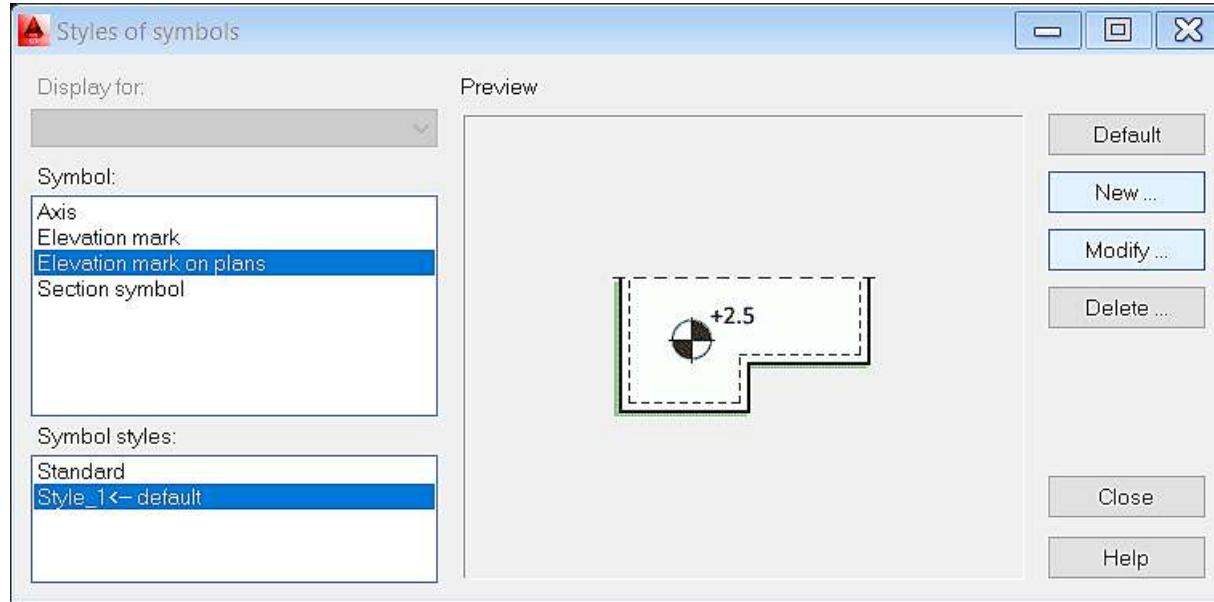

ثم اختيار قائمة Elevation mark on plans
ونضغط على Modify

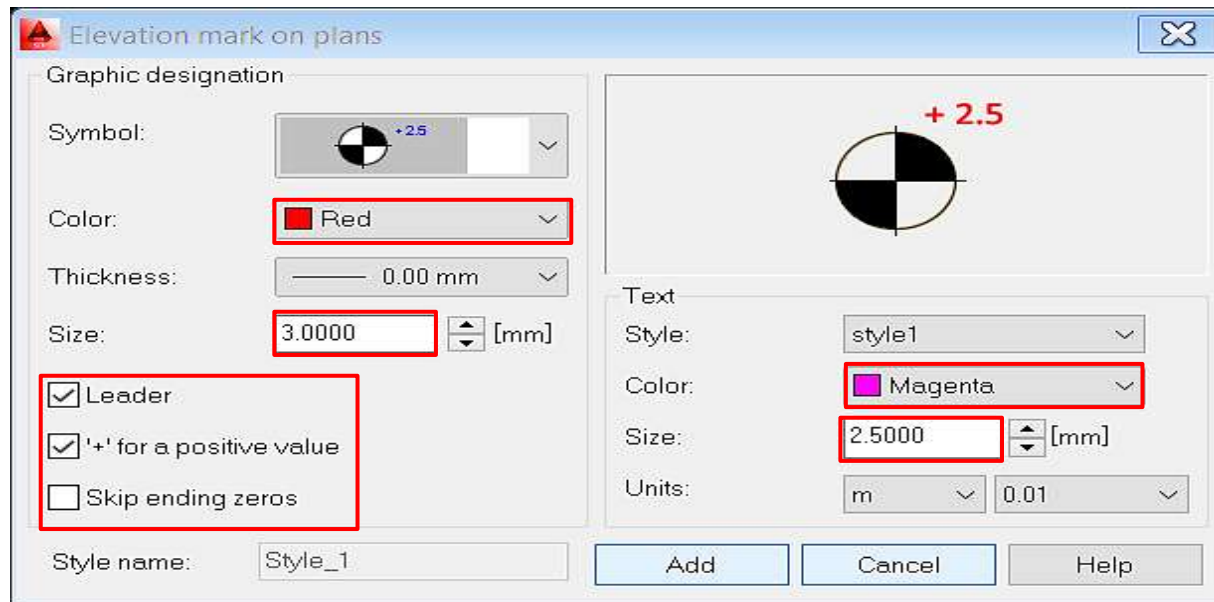

ثم التعديل على قائمة Elevation mark on plans



Notes:

1. THE COPYRIGHT OF THIS DRAWING IS VESTED IN YOURSPREADSHEETS AND IT MAY NOT BE REPRODUCED IN WHOLE OR PART OR USED FOR THE MANUFACTURE OF ANY ARTICLE WITHOUT THE EXPRESS PERMISSION OF THE COPYRIGHT HOLDERS.
2. WORK TO DIMENSIONS ONLY.

Key plane

Before

Instructor :

YourSpreadsheets

Address line 1
Address line 2
Telephone line 1
Fax line 1
www.YourSpreadsheets.co.uk

CLIENT: BAH i CLIENT
3 Mossadak, Ad Doqi, Dokki,
Giza Governorate, Giza,
Egypt


ARCHITECT: Amr Mamdoh
40 Mossadak, Ad Doqi, Dokki,
Giza Governorate, Giza,
Egypt

SITE: 31 ROVER ROAD
BLOCK A AND B


TITLE: RC DETAILS AND SECTIONS
OF GROUND BEAMS

SCALE AT A2: 1:50, 1:100	DATE: 05/09/13	DRAWN: DJ	CHECKED: DJ
PROJECT NO: 24567	DRAWING NO: A2/248	REVISION: C	

Template على برنامج الـ AS

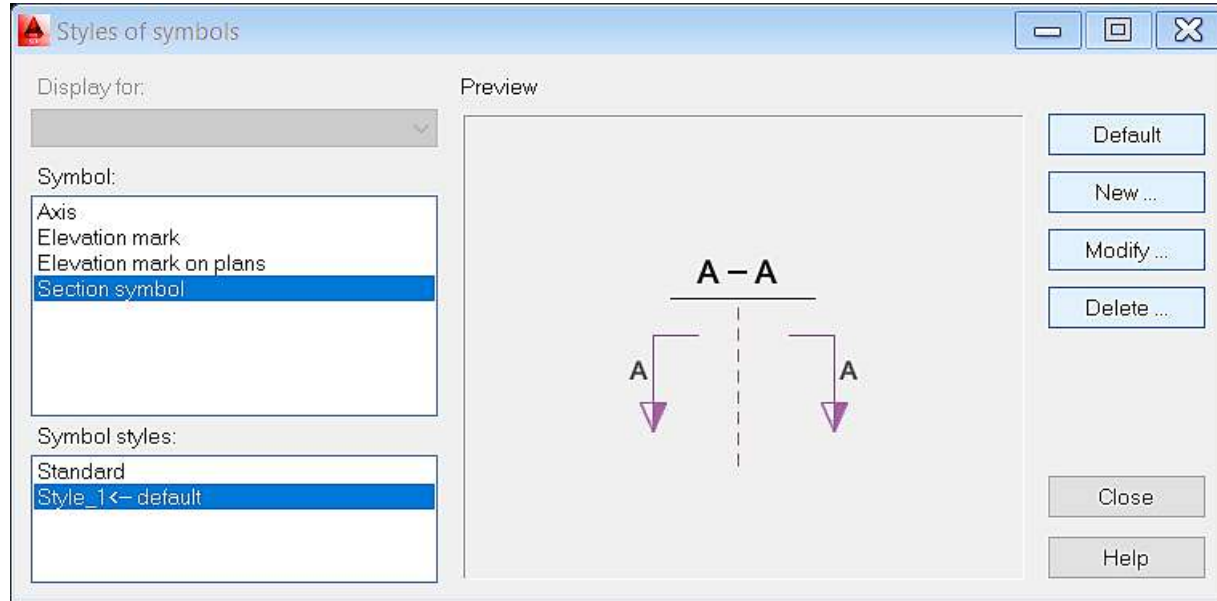

ثم اختيار قائمة Section symbol
ونضغط على Modify

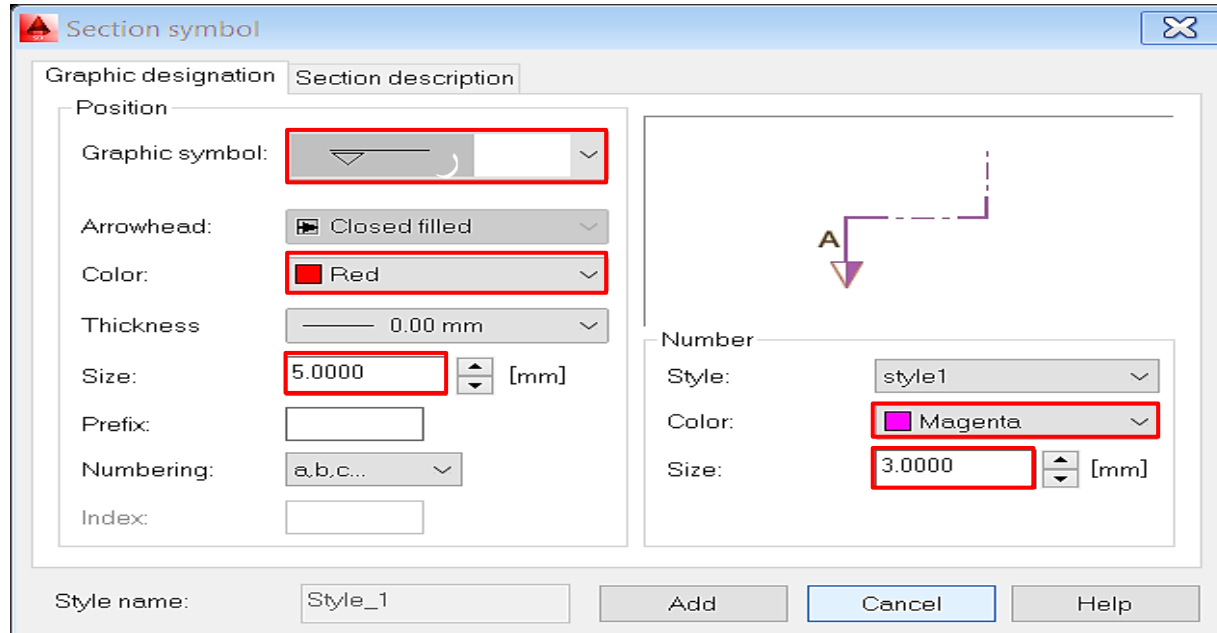

ثم اختيار قائمة Graphic designation
والتعديل



Notes:

1. THE COPYRIGHT OF THIS DRAWING IS VESTED IN YOURSPREADSHEETS AND IT MAY NOT BE REPRODUCED IN WHOLE OR PART OR USED FOR THE MANUFACTURE OF ANY ARTICLE WITHOUT THE EXPRESS PERMISSION OF THE COPYRIGHT HOLDERS.
2. WORK TO DIMENSIONED DIMENSIONS ONLY.

Key plane

Before

Instructor :

YourSpreadsheets

Address line 1
Address line 2
Telephone line 1
Fax line 1
www.YourSpreadsheets.co.uk

CLIENT: BAH I CLIENT
3 Mossadak, Ad Doqi, Dokki,
Giza Governorate, Giza,
Egypt

ARCHITECT: Amr Mamdoh
40 Mossadak, Ad Doqi, Dokki,
Giza Governorate, Giza,
Egypt

SITE: 31 ROVER ROAD
BLOCK A AND B

TITLE: RC DETAILS AND SECTIONS
OF GROUND BEAMS

SCALE AT A2: 1:50, 1:100	DATE: 05/09/13	DRAWN: DJ	CHECKED: DJ
PROJECT NO: 24567	DRAWING NO: A2/248	REVISION: C	

Template على برنامج الـ AS

Section symbol

Graphic designation | Section description

Description text

Style: style1

Color: White

Size: 4.0000 [mm]

☒ Underline

Color: Cyan

Thickness: 0.00 mm

☒ Prefix

Sec

Style name: Style_1

Add Cancel Help

Styles of symbols

Display for:

Symbol:

- Axis
- Elevation mark
- Elevation mark on plans
- Section symbol

Symbol styles:

- Standard
- Style_1 ← default

Preview

A - A

A A

Default New ... Modify ... Delete ...

Close Help

ثم اختيار قائمة Section description
والتعديل ثم الضغط على Cancel

ثم الضغط على Close



Notes:

1. THE COPYRIGHT OF THIS DRAWING IS VESTED IN YOURSPOONSHEETS AND IT MAY NOT BE REPRODUCED IN WHOLE OR PART OR USED FOR THE MANUFACTURE OF ANY ARTICLE WITHOUT THE EXPRESS PERMISSION OF THE COPYRIGHT HOLDERS.
2. WORK TO DIMENSIONS ONLY.

Key plane

Before

Instructor :

YourSpreadsheets

Address line 1
Address line 2
Telephone line 1
Fax line 1
www.YourSpreadsheets.co.uk

CLIENT: BAH i CLIENT
3 Mossadak, Ad Doqi, Dokki,
Giza Governorate, Giza,
Egypt

ARCHITECT: Amr Mamdoh
40 Mossadak, Ad Doqi, Dokki,
Giza Governorate, Giza,
Egypt


SITE: 31 ROVER ROAD
BLOCK A AND B

TITLE: RC DETAILS AND SECTIONS
OF GROUND BEAMS



SCALE AT A2: 1:50, 1:100	DATE: 05/09/13	DRAWN: DJ	CHECKED: DJ
PROJECT NO: 24567	DRAWING NO: A2/248	REVISION: C	

Template على برنامج الـ AS

الدخول على قائمة settings

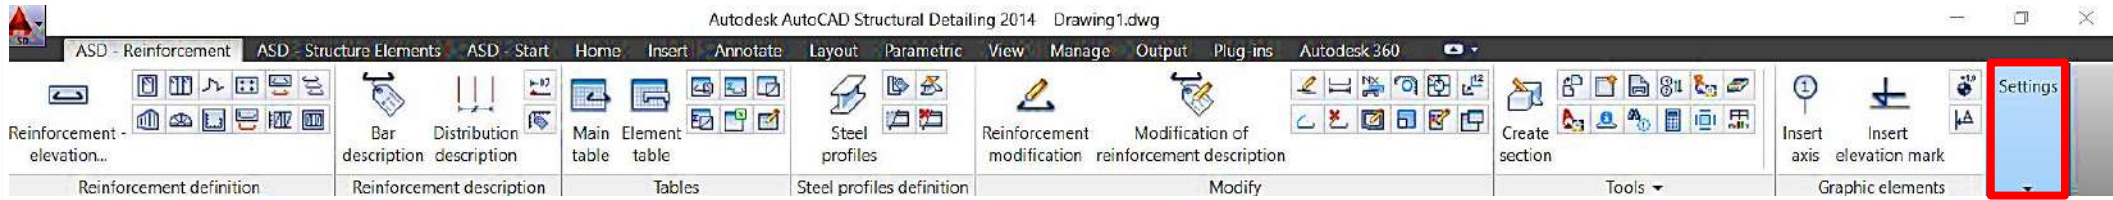

ثم اختيار قائمة Styles ونختار منها Graphic elements styles

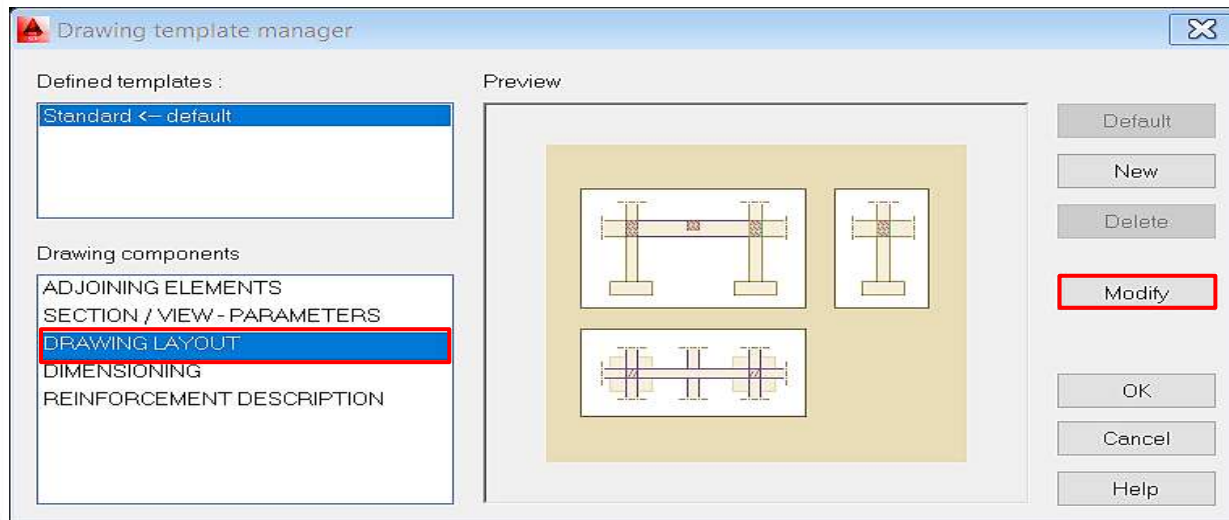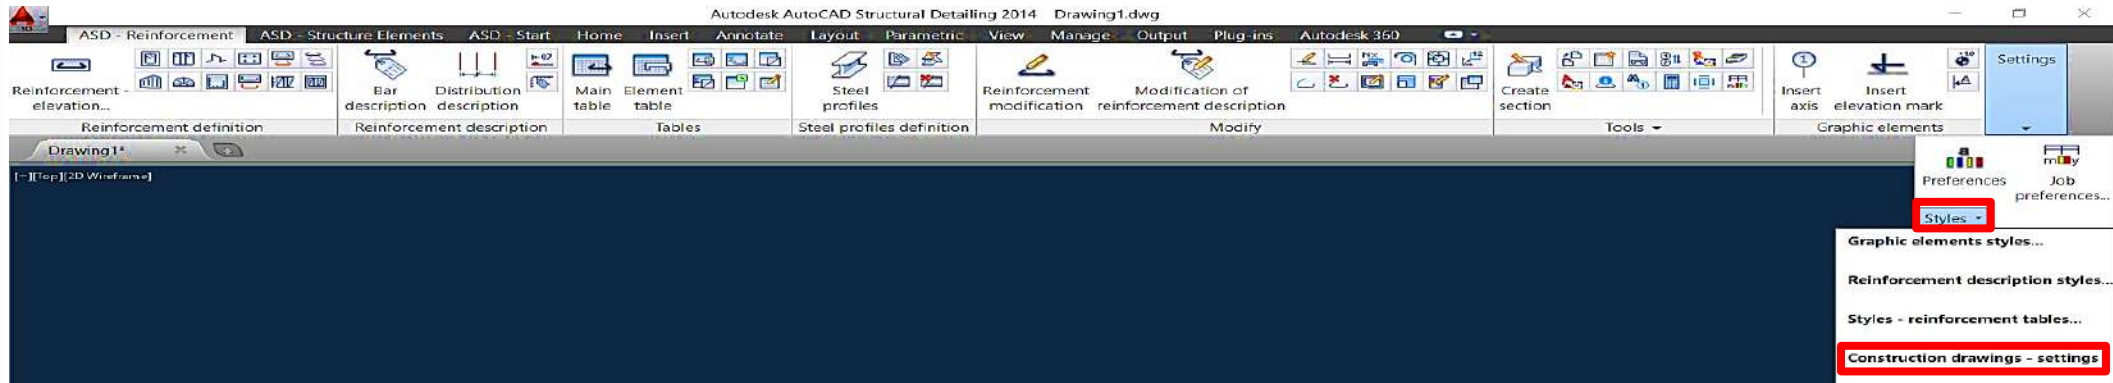

ثم اختيار قائمة DRAWING LAYOUT ونضغط على Modify



Notes:

1. THE COPYRIGHT OF THIS DRAWING IS VESTED IN YOURSPREADSHEETS AND IT MAY NOT BE REPRODUCED IN WHOLE OR PART OR USED FOR THE MANUFACTURE OF ANY ARTICLE WITHOUT THE EXPRESS PERMISSION OF THE COPYRIGHT HOLDERS.
2. WORK TO DIMENSIONS ONLY.

Key plane

Before

Instructor :

YourSpreadsheets

Address line 1
Address line 2
Telephone line 1
Fax line 1
www.YourSpreadsheets.co.uk

CLIENT: BAH i CLIENT
3 Mossadak, Ad Doqi, Dokki,
Giza Governorate, Giza,
Egypt

ARCHITECT: Amr Mamdoh
40 Mossadak, Ad Doqi, Dokki,
Giza Governorate, Giza,
Egypt

SITE: 31 ROVER ROAD
BLOCK A AND B
TITLE: RC DETAILS AND SECTIONS
OF GROUND BEAMS
SCALE AT A2: 1:50, 1:100
DATE: 05/09/13
DRAWN: DJ
CHECKED: DJ
PROJECT NO: 24567
DRAWING NO: A2/248
REVISION: C

Template على برنامج الـ AS

تعديل Scale



Notes:

1. THE COPYRIGHT OF THIS DRAWING IS VESTED IN YOURSPREADSHEETS AND IT MAY NOT BE REPRODUCED IN WHOLE OR PART OR USED FOR THE MANUFACTURE OF ANY ARTICLE WITHOUT THE EXPRESS PERMISSION OF THE COPYRIGHT HOLDERS.
2. WORK TO DIMENSIONS ONLY.

Key plane

Before

Instructor :

YourSpreadsheets

Address line 1
Address line 2
Telephone line 1
Fax line 1
www.YourSpreadsheets.co.uk

CLIENT: **BAHI CLIENT**
3 Mossadak, Ad Doqi, Dokki,
Giza Governorate, Giza,
Egypt

ARCHITECT: **Amr Mamdoh**
40 Mossadak, Ad Doqi, Dokki,
Giza Governorate, Giza,
Egypt

SITE: **31 ROVER ROAD
BLOCK A AND B**

TITLE: **RC DETAILS AND SECTIONS
OF GROUND BEAMS**

SCALE AT A2: 1:50, 1:100	DATE: 05/09/13	DRAWN: DJ	CHECKED: DJ
PROJECT NO: 24567	DRAWING NO: A2/248	REVISION: C	

Drawing layout

Element type: Column

1 : 25

1 : 25

Style name: Standard

OK Cancel Help

Drawing layout

Element type: Beam

1 : 25

1 : 25

Style name: Standard

OK Cancel Help

Drawing layout

Element type: Spread footing

1 : 25

1 : 25

1 : 25

Style name: Standard

OK Cancel Help

Drawing layout

Element type: Arbitrary element

1 : 25


1 : 25

Style name: Standard



OK Cancel Help

Template على برنامج الـ AS

الدخول على قائمة Tools

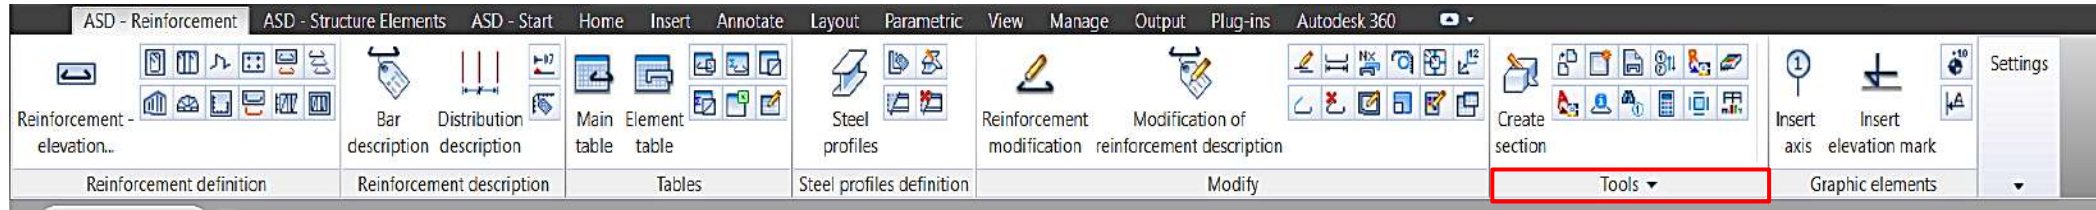

ثم اختيار show - Object inspector من قائمة Tools لإظهار الشريط الجانبي

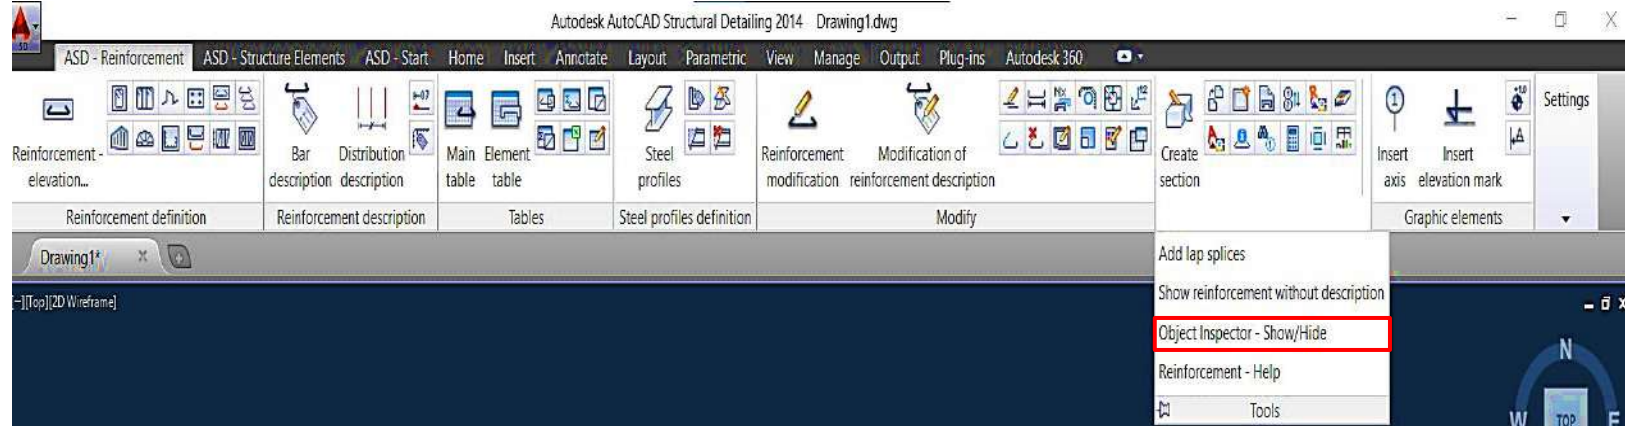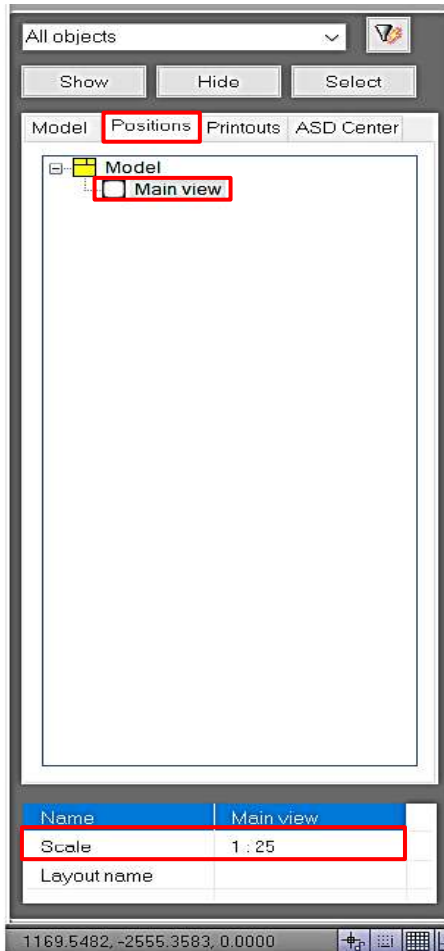

ثم تعديل Scale من الشريط الجانبي



Notes:

1. THE COPYRIGHT OF THIS DRAWING IS VESTED IN YOURSPREADSHEETS AND IT MAY NOT BE REPRODUCED IN WHOLE OR PART OR USED FOR THE MANUFACTURE OF ANY ARTICLE WITHOUT THE EXPRESS PERMISSION OF THE COPYRIGHT HOLDERS.
2. WORK TO DIMENSIONS ONLY.

Key plane

Before

Instructor :

YourSpreadsheets

Address line 1
Address line 2
Telephone line 1
Fax line 1
www.YourSpreadsheets.co.uk

CLIENT: BAH i CLIENT
3 Mossadak, Ad Doqi, Dokki,
Giza Governorate, Giza,
Egypt

ARCHITECT: Amr Mamdoh
40 Mossadak, Ad Doqi, Dokki,
Giza Governorate, Giza,
Egypt

SITE: 31 ROVER ROAD
BLOCK A AND B

TITLE: RC DETAILS AND SECTIONS
OF GROUND BEAMS

SCALE AT AS:	DATE:	DRAWN:	CHECKED:
1:50, 1:100	05/09/13	DJ	DJ
PROJECT NO:	DRAWING NO:	REVISION:	
24567	A2/248	C	

Template على برنامج الـ AS

تعديل أقطار الأسياخ



Notes:

1. THE COPYRIGHT OF THIS DRAWING IS VESTED IN YOURSPREADSHEETS AND IT MAY NOT BE REPRODUCED IN WHOLE OR PART OR USED FOR THE MANUFACTURE OF ANY ARTICLE WITHOUT THE EXPRESS PERMISSION OF THE COPYRIGHT HOLDERS.
2. WORK TO DIMENSIONS ONLY.

Key plane

Before

Instructor :

YourSpreadsheets

Address line 1
Address line 2
Telephone line 1
Fax line 1
www.YourSpreadsheets.co.uk



CLIENT: BAH I CLIENT
3 Mossadak, Ad Doqi, Dokki,
Giza Governorate, Giza,
Egypt

ARCHITECT: Amr Mamdoh
40 Mossadak, Ad Doqi, Dokki,
Giza Governorate, Giza,
Egypt

SITE: 31 ROVER ROAD
BLOCK A AND B

TITLE: RC DETAILS AND SECTIONS
OF GROUND BEAMS

SCALE AT AS: 1:50, 1:100	DATE: 05/09/13	DRAWN: DJ	CHECKED: DJ
PROJECT NO: 24567	DRAWING NO: A2/248	REVISION: C	

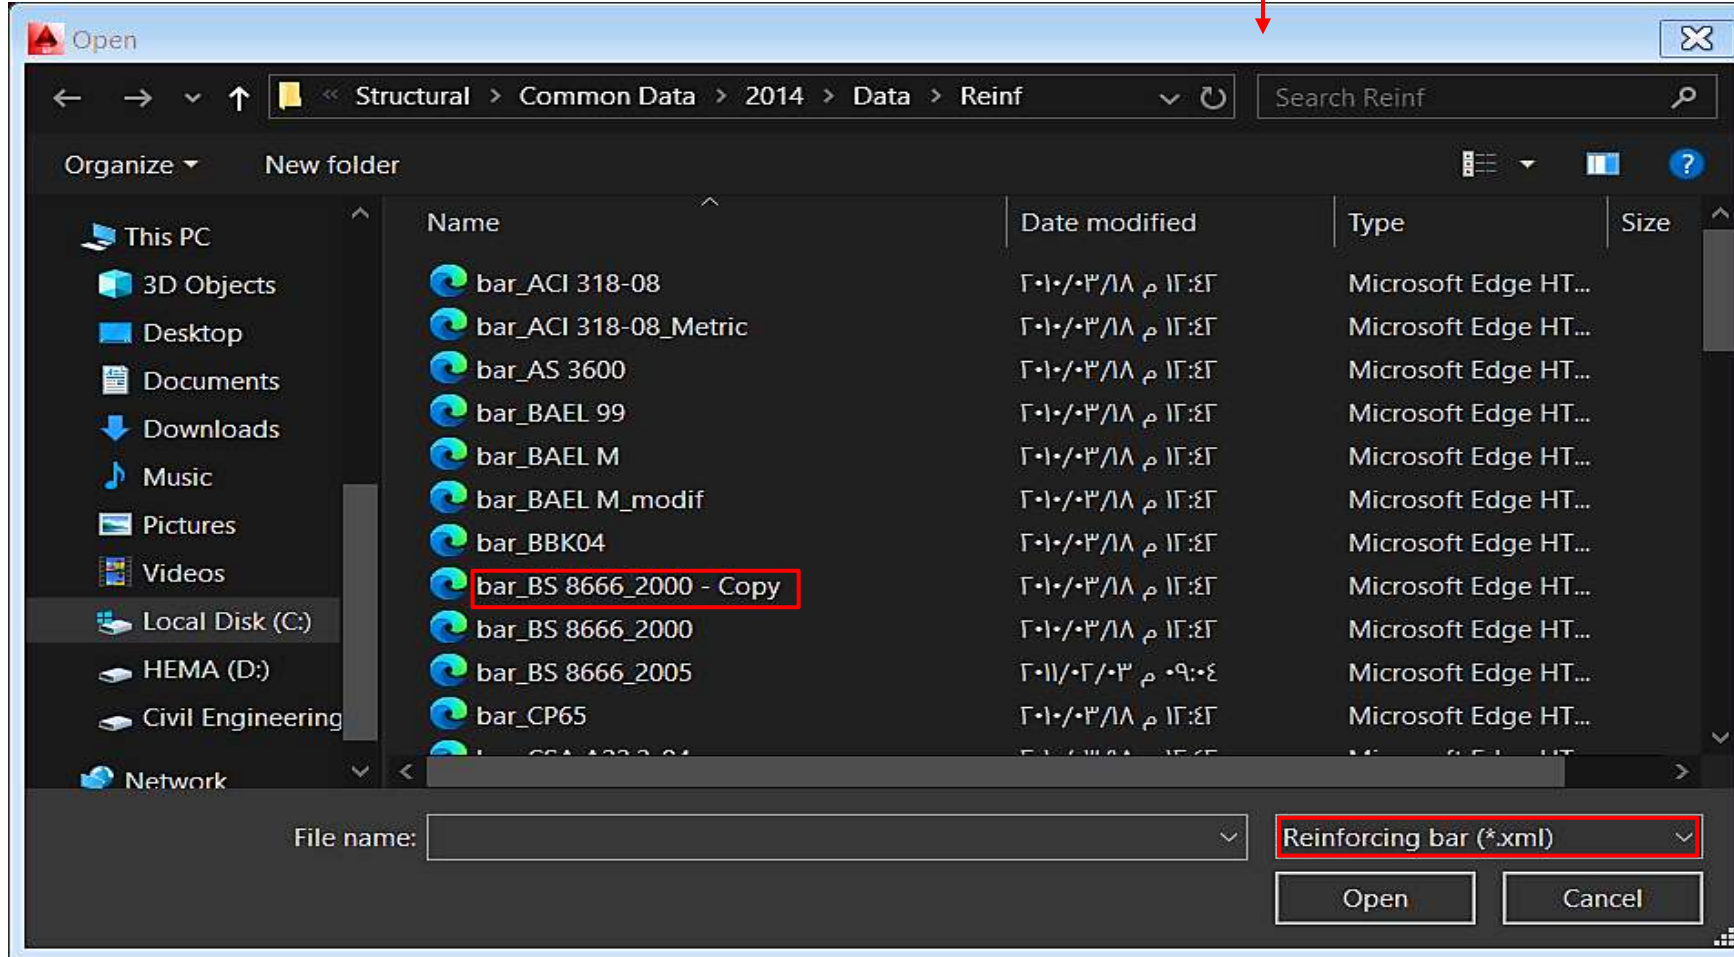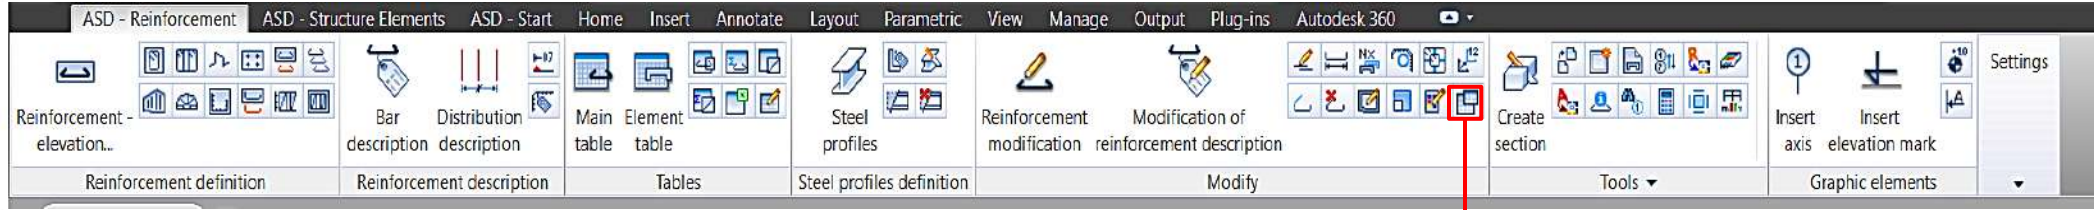

Template على برنامج الـ AS

جدول أقطار الأسياخ



Notes:

1. THE COPYRIGHT OF THIS DRAWING IS VESTED IN YOURSPREADSHEETS AND IT MAY NOT BE REPRODUCED IN WHOLE OR PART OR USED FOR THE MANUFACTURE OF ANY ARTICLE WITHOUT THE EXPRESS PERMISSION OF THE COPYRIGHT HOLDERS.
2. WORK TO DIMENSIONS ONLY.

Key plane

Before

Instructor :

YourSpreadsheets

Address line 1
Address line 2
Telephone line 1
Fax line 1
www.YourSpreadsheets.co.uk

CLIENT: BAH i CLIENT
3 Mossadak, Ad Doqi, Dokki,
Giza Governorate, Giza,
Egypt

ARCHITECT: Amr Mamdoh
40 Mossadak, Ad Doqi, Dokki,
Giza Governorate, Giza,
Egypt

SITE: 31 ROVER ROAD
BLOCK A AND B

TITLE: RC DETAILS AND SECTIONS
OF GROUND BEAMS

SCALE AT AS: 1:50, 1:100	DATE: 05/09/13	DRAWN: DJ	CHECKED: DJ
PROJECT NO: 24567	DRAWING NO: A2/248	REVISION: C	

C:\Users\kareem\AppData\Roaming\Autodesk\Structural\Common Data\2014\bar_BS 8666_2000 - Copy.xml



No	Steel	Diameter	Diameter Real	MaxLength	Mass	HookLen 90	HookLen 135	HookLen 180	StirrupBendFormer Diam	HookBendFormer Diam	BarBendFormerDiam	CharacteristicYield Stress	PlainBar	BarSize
1	R	6	6	12	0.222	12	7	4	24	24	24	50000000	☒	6
2	R	8	8	12	0.395	12	7	4	32	32	32	50000000	☒	8
3	T	10	10	12	0.617	12	7	6	60	60	60	60000000	☐	10
4	T	12	12	12	0.888	12	7	6	72	72	72	60000000	☐	12
5	T	16	16	12	1.58	12	7	6	96	96	96	60000000	☐	16
6	T	20	20	12	2.47	12	7	6	120	120	120	60000000	☐	20
7	T	25	25	12	3.85	12	7	6	150	150	150	60000000	☐	25
8	T	32	32	12	6.31	12	7	8	256	256	256	60000000	☐	32
9	T	40	40	12	9.87	12	7	8	320	320	320	60000000	☐	40
10	T	18	18	12	2	12	7	6	192	192	192	60000000	☐	32
*														


Bar definition / Formula / Hooks / Description / Info /

OK

Cancel

Template على برنامج الـ AS

حفظ Template

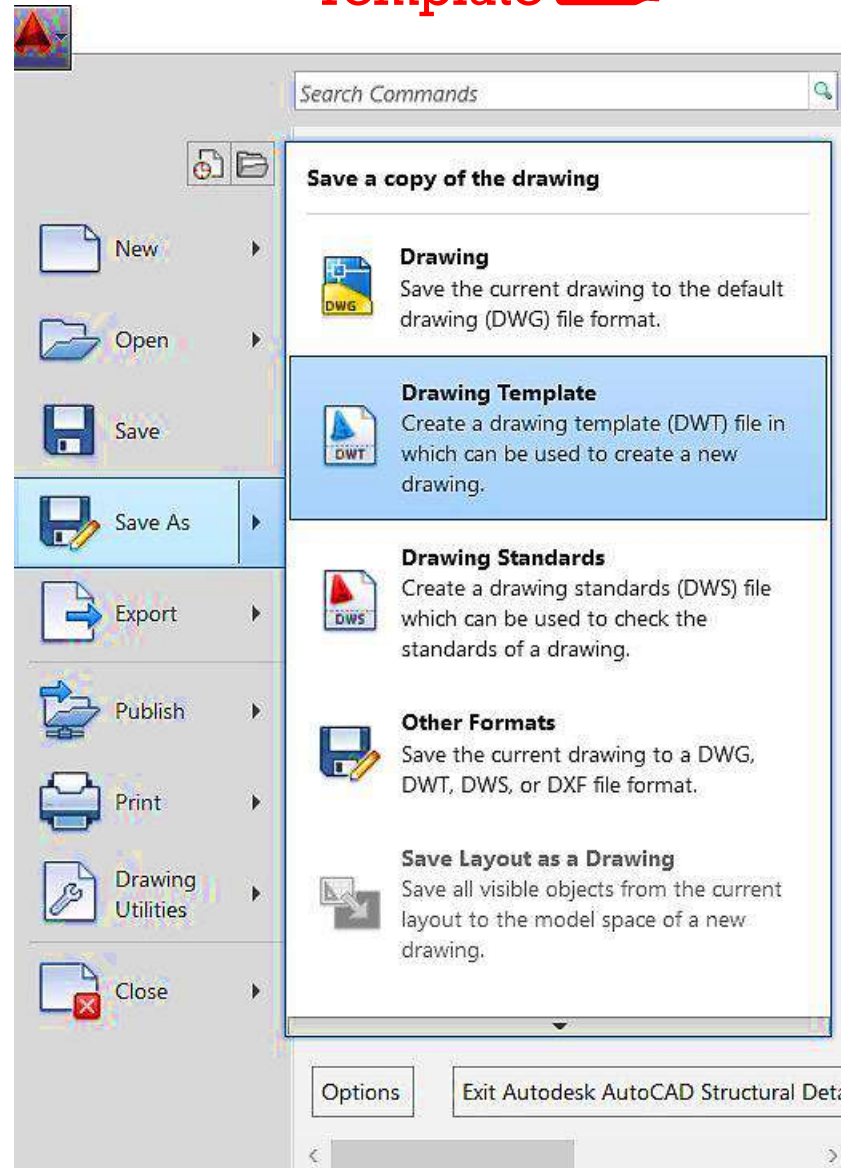

Notes:

1. THE COPYRIGHT OF THIS DRAWING IS VESTED IN YOURSPREADSHEETS AND IT MAY NOT BE REPRODUCED IN WHOLE OR PART OR USED FOR THE MANUFACTURE OF ANY ARTICLE WITHOUT THE EXPRESS PERMISSION OF THE COPYRIGHT HOLDERS.
2. WORK TO FINISHED DIMENSIONS ONLY.

Key plane

Before

Instructor :

YourSpreadsheets

Address line 1
Address line 2
Telephone line 1
Fax line 1
www.YourSpreadsheets.co.uk

CLIENT: **BAHI CLIENT**
3 Mossadak, Ad Doqi, Dokki,
Giza Governorate, Giza,
Egypt

ARCHITECT: **Amr Mamdoh**
40 Mossadak, Ad Doqi, Dokki,
Giza Governorate, Giza,
Egypt

SITE: **31 ROVER ROAD
BLOCK A AND B**

TITLE: **RC DETAILS AND SECTIONS
OF GROUND BEAMS**

SCALE AT A2: 1:50, 1:100	DATE: 05/09/13	DRAWN: DJ	CHECKED: DJ
PROJECT NO: 24567	DRAWING NO: A2/248	REVISION: C	

THE END

COURSE: TECHNICAL OFFICE G46

Name: Ibrahim Mohamed Read

Eng: Amr Mamdouh

Lecture: 15



Task: 12

الحصر الهندسي لحديد القواعد المسلحة وأشابر الأعمدة باستخدام برنامج ASD

حصر حديد القواعد المنفصلة مانيوال

نموذج القاعدة	الكود	القطر	عدد الأسياخ في المتر	مسافة التوزيع	العدد المطلوب	طول السيخ	اجمالي الأطوال	وزن المتر الطولي	عدد العناصر	الوزن
f1	١	١٦	٠,٢	١,٢٠٠	٢,٠٠٠	١,٨٣٦	٣,٦٧٢	١,٥٨٠	٢,٠٠٠	١١,٦٠٥٣٣٣٣
	٢	١٦	٠,٢	١,٢٠٠	٢,٠٠٠	١,٨٣٦	٣,٦٧٢	١,٥٨٠	٢,٠٠٠	١١,٦٠٥٣٣٣٣

الإتجاه الطويل هو نفس الإتجاه القصير وذلك لان الطول والعرض لهما نفس القيمة ١,٢٥ م

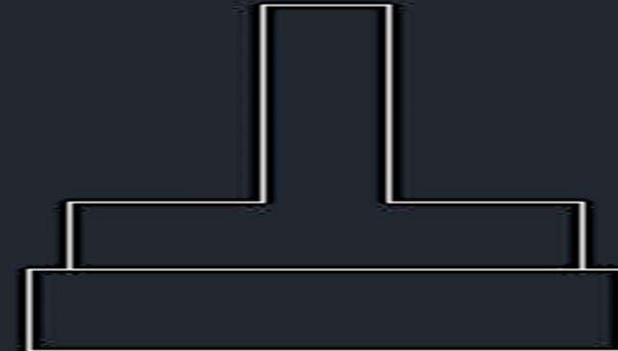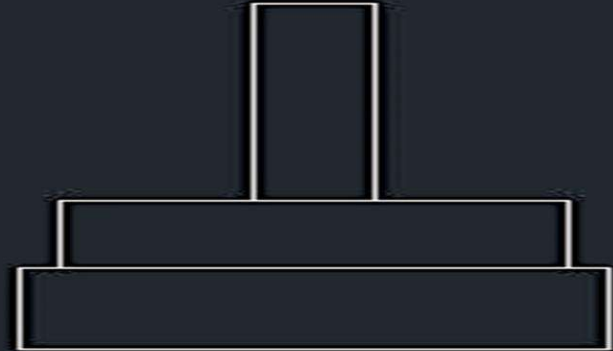

Notes:

1. THE COPYRIGHT OF THIS DRAWING IS VESTED IN YOURSPREADSHEETS AND IT MAY NOT BE REPRODUCED IN WHOLE OR PART OR USED FOR THE MANUFACTURE OF ANY ARTICLE WITHOUT THE EXPRESS PERMISSION OF THE COPYRIGHT HOLDERS.
2. WORK TO DIMENSIONS ONLY.

Key plane

Before

Instructor :

YourSpreadsheets

Address line 1
Address line 2
Telephone line 1
Fax line 1
www.YourSpreadsheets.co.uk

CLIENT: BAH i CLIENT
3 Mossadak, Ad Doqi, Dokki,
Giza Governorate, Giza,
Egypt

ARCHITECT: Amr Mamdoh
40 Mossadak, Ad Doqi, Dokki,
Giza Governorate, Giza,
Egypt

SITE: 31 ROVER ROAD
BLOCK A AND B

TITLE: RC DETAILS AND SECTIONS
OF GROUND BEAMS

SCALE AT A2: 1:50, 1:100	DATE: 05/09/13	DRAWN: DJ	CHECKED: DJ
PROJECT NO: 24567	DRAWING NO: A2/248	REVISION: C	

الحصر الهندسي لحديد القواعد المسلحة وأشابر الأعمدة باستخدام برنامج ASD



Notes:

1. THE COPYRIGHT OF THIS DRAWING IS VESTED IN YOURSPREADSHEETS AND IT MAY NOT BE REPRODUCED IN WHOLE OR PART OR USED FOR THE MANUFACTURE OF ANY ARTICLE WITHOUT THE EXPRESS PERMISSION OF THE COPYRIGHT HOLDERS.
2. WORK TO FIGURED DIMENSIONS ONLY.

Key plane

Before

B.B.S

Number

Position	Diameter	in the element	of elements	Symbol (m)	Length (m)	Total mass (kg)
01	16	2	2		1.9	11.69
02	16	2	2		1.9	11.85
03	10	1	2		4.7	5.74
05	16	1	2		1.8	5.69

B.B.S

T	Ø 10	Ø 16
Unit weight (kg/m)	0.62	1.58
Total length (m)	9.3	18.5
Total weight (kg)	5.74	29.23

Instructor :

YourSpreadsheets

Address line 1
Address line 2
Telephone line 1
Fax line 1
www.YourSpreadsheets.co.uk

CLIENT: BAH i CLIENT
3 Mossadak, Ad Doqi, Dokki,
Giza Governorate, Giza,
Egypt

ARCHITECT: Amr Mamdoh
40 Mossadak, Ad Doqi, Dokki,
Giza Governorate, Giza,
Egypt

SITE: 31 ROVER ROAD
BLOCK A AND B

TITLE: RC DETAILS AND SECTIONS
OF GROUND BEAMS

SCALE AT A2: 1:50, 1:100	DATE: 05/09/13	DRAWN: DJ	CHECKED: DJ
PROJECT NO: 24567	DRAWING NO: A2/248	REVISION: C	

الحصر الهندسي لحديد القواعد المسلحة واشارات الأعمدة باستخدام برنامج ASD



Notes:

1. THE COPYRIGHT OF THIS DRAWING IS VESTED IN YOURSPREADSHEETS AND IT MAY NOT BE REPRODUCED IN WHOLE OR PART OR USED FOR THE MANUFACTURE OF ANY ARTICLE WITHOUT THE EXPRESS PERMISSION OF THE COPYRIGHT HOLDERS.
2. WORK TO DIMENSIONED DIMENSIONS ONLY.

Key plane

Before

Instructor :

YourSpreadsheets

Address line 1
Address line 2
Telephone line 1
Fax line 1
www.YourSpreadsheets.co.uk






CLIENT: BAH i CLIENT
3 Mossadak, Ad Doqi, Dokki,
Giza Governorate, Giza,
Egypt

ARCHITECT: Amr Mamdoh
40 Mossadak, Ad Doqi, Dokki,
Giza Governorate, Giza,
Egypt

SITE: 31 ROVER ROAD
BLOCK A AND B

TITLE: RC DETAILS AND SECTIONS
OF GROUND BEAMS

SCALE AT AS: 1:50, 1:100	DATE: 05/09/13	DRAWN: DJ	CHECKED: DJ
PROJECT NO: 24567	DRAWING NO: A2/248	REVISION: C	

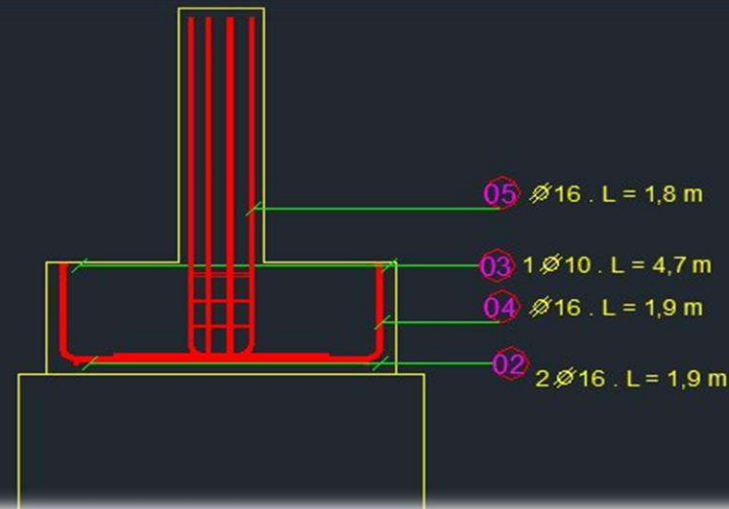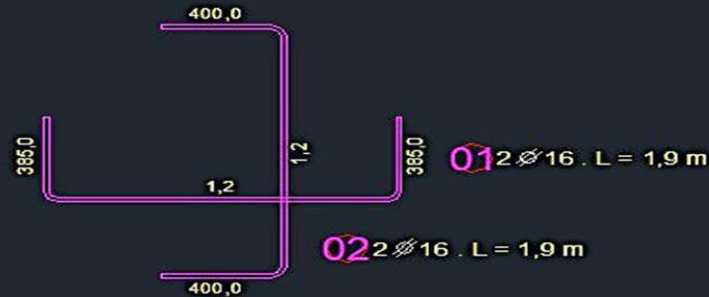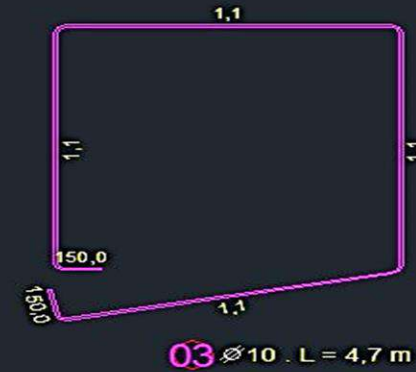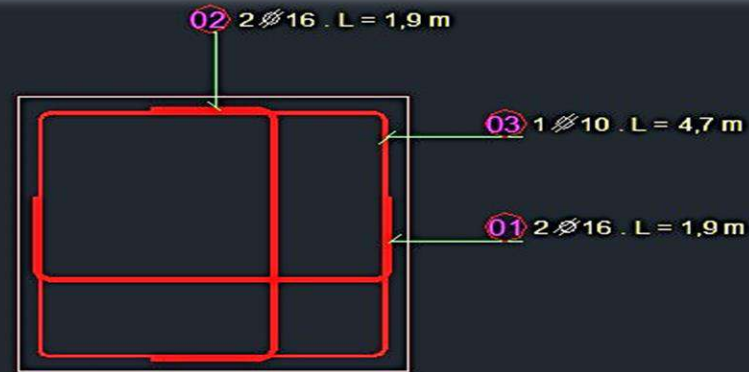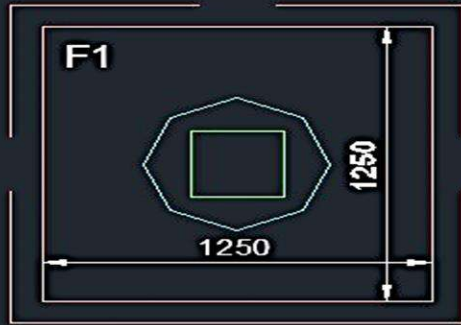

لوحة الحصر الهندسي لحديد القواعد المسلحة وأشائر الأعمدة باستخدام برنامج ASD



Notes:

1. THE COPYRIGHT OF THIS DRAWING IS VESTED IN YOURSPREADSHEETS AND IT MAY NOT BE REPRODUCED IN WHOLE OR PART OR USED FOR THE MANUFACTURE OF ANY ARTICLE WITHOUT THE EXPRESS PERMISSION OF THE COPYRIGHT HOLDERS.
2. WORK TO FIGURED DIMENSIONS ONLY.

Key plane

Before

Instructor :

YourSpreadsheets

Address line 1
Address line 2
Telephone line 1
Fax line 1
www.YourSpreadsheets.co.uk


CLIENT: BAH i CLIENT
3 Mossadak, Ad Doqi, Dokki,
Giza Governorate, Giza,
Egypt

ARCHITECT: Amr Mamdoh
40 Mossadak, Ad Doqi, Dokki,
Giza Governorate, Giza,
Egypt

SITE: 31 ROVER ROAD
BLOCK A AND B

TITLE: RC DETAILS AND SECTIONS
OF GROUND BEAMS

SCALE AT AS:	DATE:	DRAWN:	CHECKED:
1:50, 1:100	05/09/13	DJ	DJ
PROJECT NO:	DRAWING NO:	REVISION:	
24567	A2/248	C	

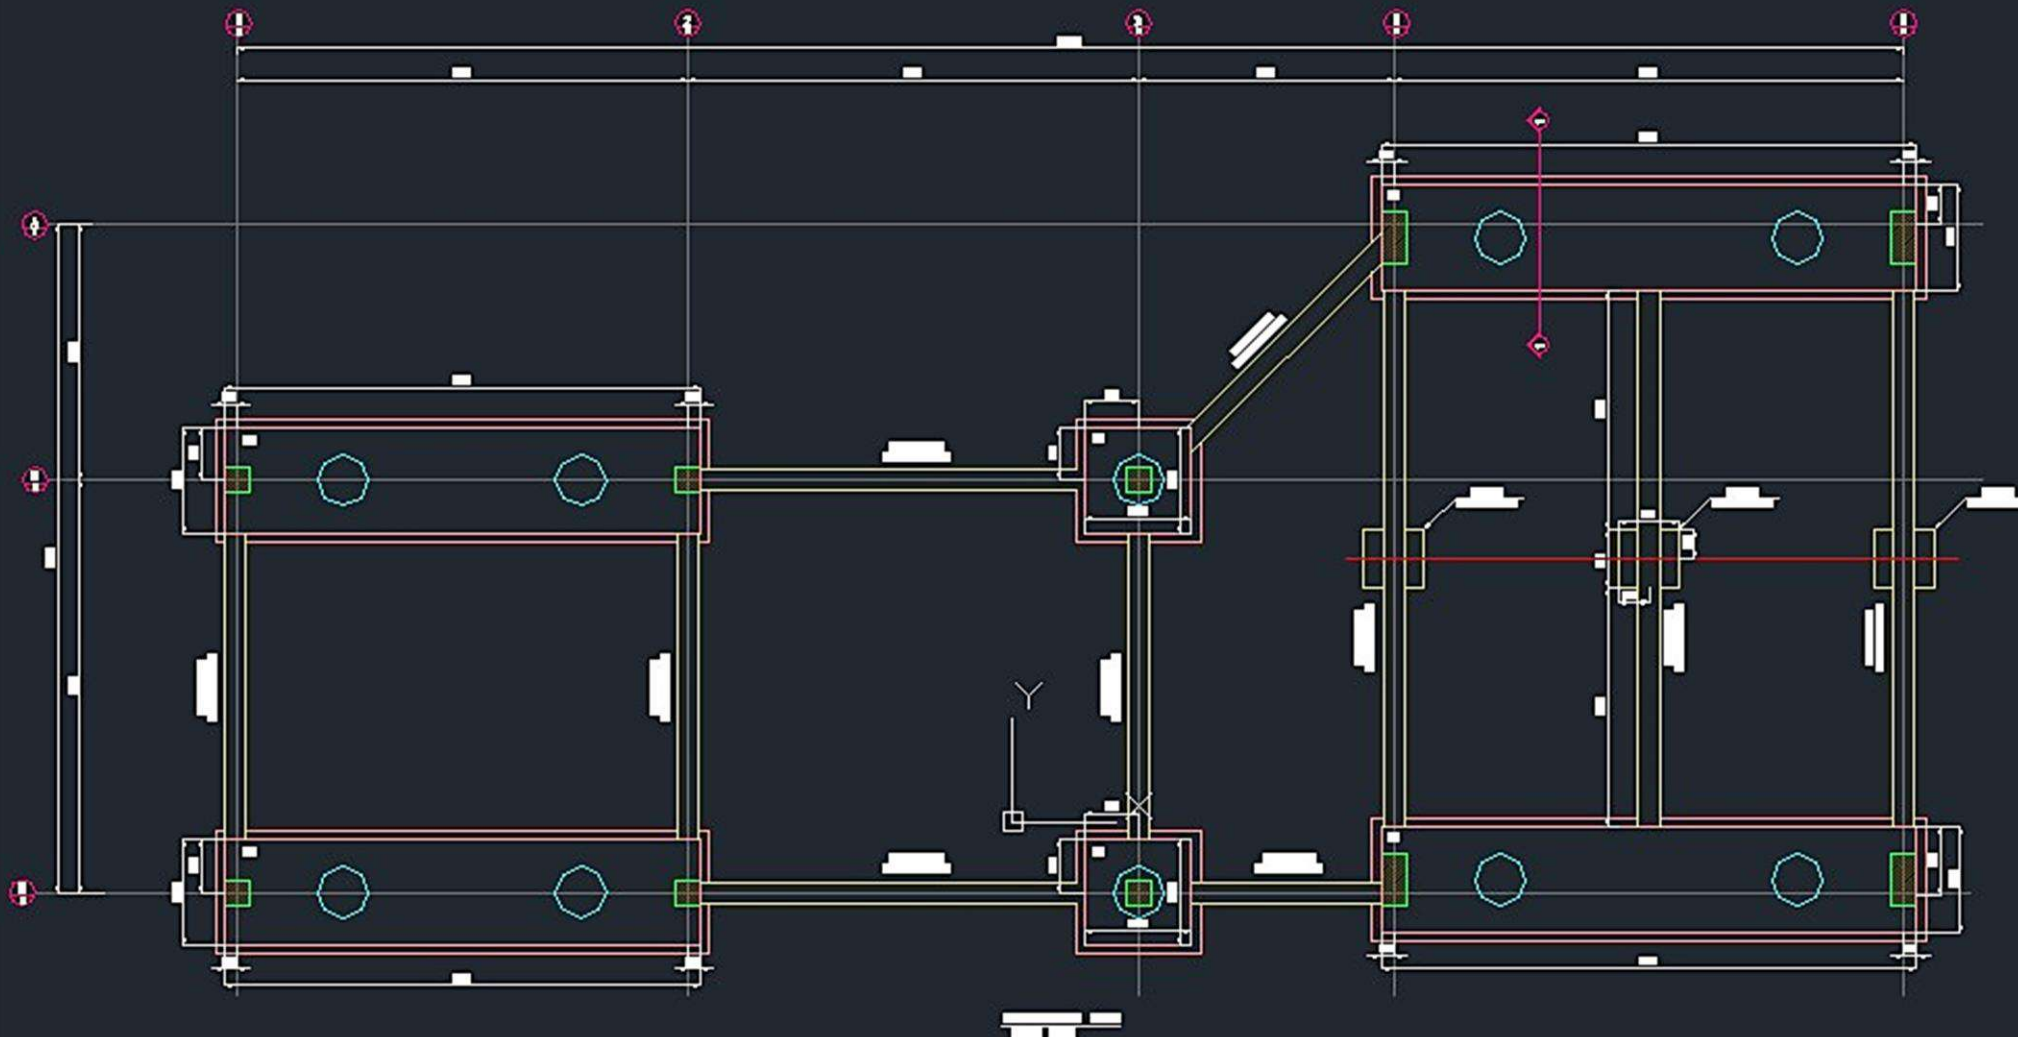

THE END

COURSE: TECHNICAL OFFICE G46

Name: Ibrahim Mohamed Read

Eng: Amr Mamdouh

Lecture: 16

Task: 13

Arvil Group
CONSTRUCTION & TRAINING COMPANY

1. THE COPYRIGHT OF THIS DRAWING IS VESTED IN TONSPOODSHEET AND IT MAY NOT BE REPRODUCED IN WHOLE OR PART OR USED FOR THE MANUFACTURE OF ANY ARTICLE WITHOUT THE EXPRESS PERMISSION OF THE COPYRIGHT HOLDERS.

2. WORK TO FIGURED DIMENSIONS ONLY.

Technical drawing of a reinforced concrete slab for a rectangular room. The drawing includes a plan view (top left), a section view (top right), and a detail view (bottom left).

Plan View (Top Left): Shows the slab dimensions: 5.8m by 5.8m. The reinforcement is labeled with numbers and dimensions:

- 01 5ø16 . L = 6,4 m
- 02 7ø18 . L = 6,5 m
- 03 5ø16 . L = 2,1 m
- 04 29ø16 . L = 2,0 m
- 05 7ø18 . L = 6,4 m
- 06 1ø12 . L = 5,6 m
- 07 6ø16 . L = 1,5 m
- 08 8ø16 . L = 1,6 m
- 09 2ø10 . L = 14,5 m

Section View (Top Right): Shows the slab thickness of 14cm and the reinforcement layout. The reinforcement is labeled with numbers and dimensions:

- 10 ø16 . L = 1,6 m
- 11 ø16 . L = 1,6 m

Detail View (Bottom Left): Shows the reinforcement layout for a corner. The reinforcement is labeled with numbers and dimensions:

- 03 5ø16 . L = 2,1 m
- 04 29ø16 . L = 2,0 m
- 05 7ø18 . L = 6,4 m
- 06 1ø12 . L = 5,6 m
- 07 6ø16 . L = 1,5 m
- 08 8ø16 . L = 1,6 m
- 09 2ø10 . L = 14,5 m

Address line 1
Address line 2
Telephone line 1
Fax line 1
www.YourSpreadsheets.co.uk

CLIENT: **BAH i CLIENT**
3 Mossadak, Ad Doqi, Dokki,
Giza Governorate, Giza,
Egypt

ARCHITECT: Amr Mamdoh
40 Mossadak, Ad Doqi, Dokki,
Giza Governorate, Giza,
Egypt

SITE: 31 ROVER ROAD
BLOCK A AND B

TITLE: RC DETAILS AND SECTIONS
OF GROUND BEAMS

SCALE AT A2:
1:50, 1:100

DATE:
05/09/13

DRAWN: DJ	CHECKED: DJ
--------------	----------------

PROJECT NO:
24567

DRAWING NO:
A2/248

REVISION:	C
-----------	---

الحصر الهندسي لحديد القواعد المسلحة وأشابر الأعمدة باستخدام برنامج ASD



Notes:

1. THE COPYRIGHT OF THIS DRAWING IS VESTED IN YOURSPREADSHEETS AND IT MAY NOT BE REPRODUCED IN WHOLE OR PART OR USED FOR THE MANUFACTURE OF ANY ARTICLE WITHOUT THE EXPRESS PERMISSION OF THE COPYRIGHT HOLDERS.
2. WORK TO FIGURED DIMENSIONS ONLY.

Key plane

Before

Instructor :

YourSpreadsheets

Address line 1
Address line 2
Telephone line 1
Fax line 1
www.YourSpreadsheets.co.uk

CLIENT: **BAHI CLIENT**
3 Mossadak, Ad Doqi, Dokki,
Giza Governorate, Giza,
Egypt

ARCHITECT: **Amr Mamdoh**
40 Mossadak, Ad Doqi, Dokki,
Giza Governorate, Giza,
Egypt

SITE: **31 ROVER ROAD
BLOCK A AND B**

TITLE: **RC DETAILS AND SECTIONS
OF GROUND BEAMS**

SCALE AT A2: 1:50, 1:100	DATE: 05/09/13	DRAWN: DJ	CHECKED: DJ
PROJECT NO: 24567	DRAWING NO: A2/248	REVISION: C	

B.B.S

Number

Position	Diameter	in the element	of elements	Symbol (m)	Length (m)	Total mass (kg)
01	16	5	2		6.4	101.52
02	18	7	2		6.5	180.60
03	16	5	2		2.0	32.39
04	16	29	2		2.0	185.57
06	12	1	2		5.6	9.99
07	16	6	2		1.5	28.91
08	16	8	2		1.6	39.82
09	10	2	2		14.5	35.72

B.B.S

T	Ø 10	Ø 12	Ø 16	Ø 18
Unit weight (kg/m)	0.62	0.89	1.58	2.00
Total length (m)	57.9	11.3	245.7	90.3
Total weight (kg)	35.72	9.99	388.21	180.60

لوحة الحصر الهندسي لتحديد القواعد المسلحة وأشاور الأعمدة باستخدام برنامج ASD

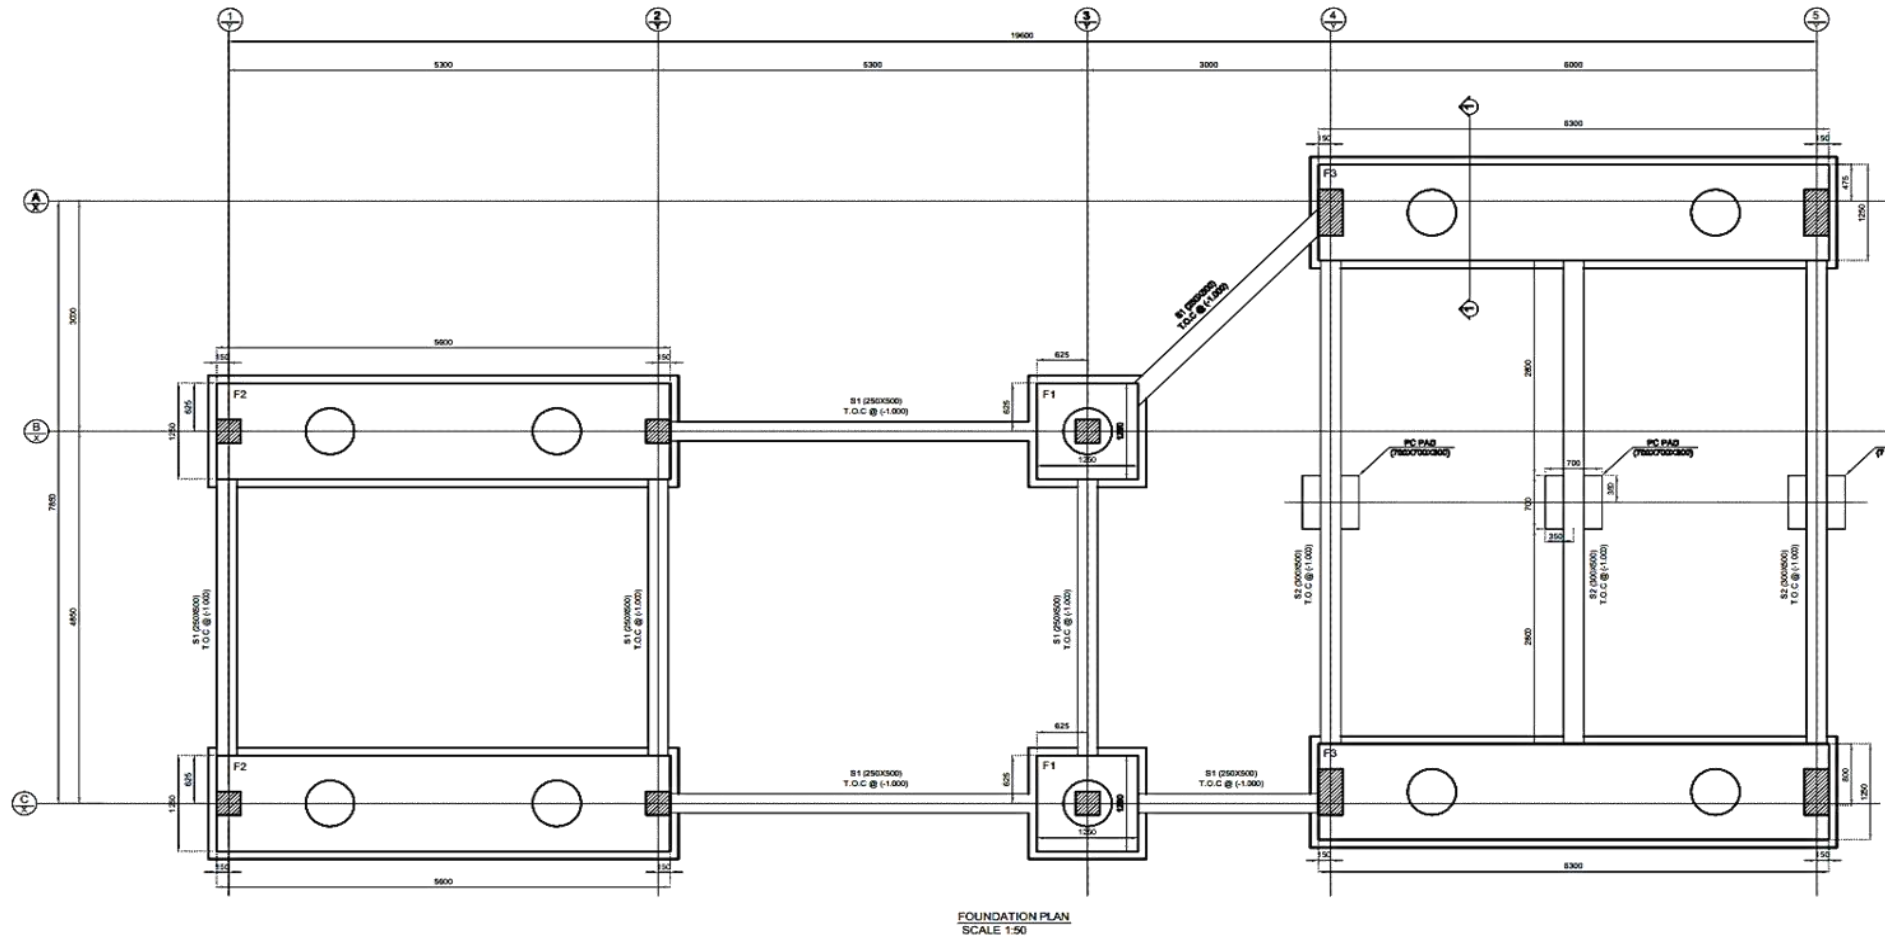


TABLE 1 PILE CAPS REINFORCEMENT AND DIMENSIONS

MODEL	P.C				R.C				TOP RFT.		BOTTOM RFT.		REMARKS
	LENGTH	BREDTH	DEPTH	T.O.PC	LENGTH	BREDTH	DEPTH	T.O.C	TRANSVERSAL	LONGITUDINAL	TRANSVERSAL	LONGITUDINAL	
F1	1450	1450	100	(-1.50)	1250	1250	500	(-1.00)	Ø 16 @ 200 mm	Ø 16 @ 200 mm	Ø 16 @ 200 mm	Ø 16 @ 200 mm	-----
F2	1450	5800	100	(-1.50)	1250	5600	500	(-1.00)	Ø 16 @ 200 mm	Ø 18 @ 100 mm	Ø 16 @ 200 mm	Ø 16 @ 200 mm	-----
F3	1450	6500	100	(-1.50)	1250	6300	500	(-1.00)	Ø 16 @ 200 mm	Ø 18 @ 100 mm	Ø 16 @ 200 mm	Ø 16 @ 200 mm	-----



Notes:

1. THE COPYRIGHT OF THIS DRAWING IS VESTED IN YOURSPREADSHEETS AND IT MAY NOT BE REPRODUCED IN WHOLE OR PART OR USED FOR THE MANUFACTURE OF ANY ARTICLE WITHOUT THE EXPRESS PERMISSION OF THE COPYRIGHT HOLDERS.
2. WORK TO FIGURED DIMENSIONS ONLY.

Key plane

Before

Instructor :

YourSpreadsheets

Address line 1
Address line 2
Telephone line 1
Fax line 1
www.YourSpreadsheets.co.uk

CLIENT: BAHİ CLIENT
3 Mossadak, Ad Doqi, Dokki,
Giza Governorate, Giza,
Egypt

ARCHITECT: Amr Mamdoh
40 Mossadak, Ad Doqi, Dokki,
Giza Governorate, Giza,
Egypt

SITE: 31 ROVER ROAD
BLOCK A AND B

TITLE: RC DETAILS AND SECTIONS
OF GROUND BEAMS

SCALE AT A2: 1:50, 1:100
DATE: 05/09/13
DRAWN: DJ
PROJECT NO: 24567
DRAWING NO: A2/248
CHECKED: DJ
REVISION: C

THE END

COURSE: TECHNICAL OFFICE G46

Name: Ibrahim Mohamed Read

Eng: Amr Mamdouh


Lecture: 17 +

first Part 1 Lec: 18

Task: 14

الحصر الهندسي لحديد السملات باستخدام برنامج ASD

الحصر الهندسي لحديد سمل S1 على مشروع Car Shed باستخدام برنامج ASD

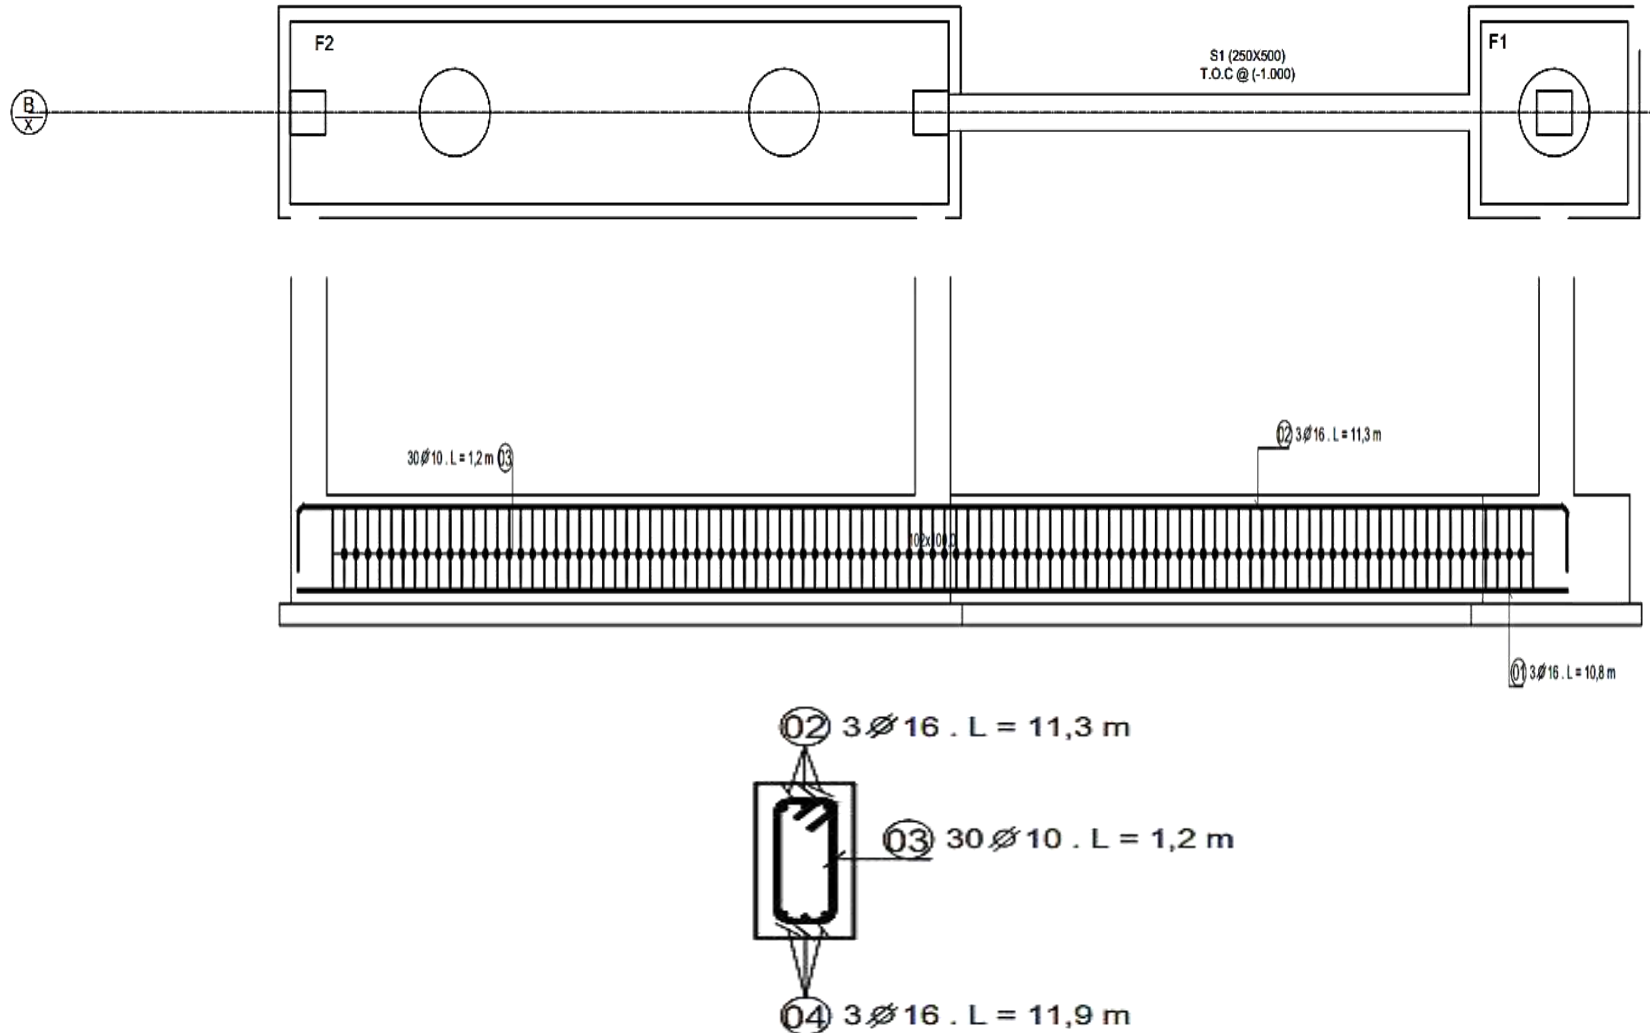

Notes:

1. THE COPYRIGHT OF THIS DRAWING IS VESTED IN YOURSPREADSHEETS AND IT MAY NOT BE REPRODUCED IN WHOLE OR PART OR USED FOR THE MANUFACTURE OF ANY ARTICLE WITHOUT THE EXPRESS PERMISSION OF THE COPYRIGHT HOLDERS.
2. WORK TO FIGURED DIMENSIONS ONLY.

Key plane

Before

Instructor :

YourSpreadsheets

Address line 1
Address line 2
Telephone line 1
Fax line 1
www.YourSpreadsheets.co.uk

CLIENT: **BAHI CLIENT**
3 Mossadak, Ad Doqi, Dokki,
Giza Governorate, Giza,
Egypt

ARCHITECT: **Amr Mamdoh**
40 Mossadak, Ad Doqi, Dokki,
Giza Governorate, Giza,
Egypt

SITE: **31 ROVER ROAD
BLOCK A AND B**

TITLE: **RC DETAILS AND SECTIONS
OF GROUND BEAMS**

SCALE AT AS:	DATE:	DRAWN:	CHECKED:
1:50, 1:100	05/09/13	DJ	DJ
PROJECT NO:	DRAWING NO:	REVISION:	
24567	A2/248	C	

الحصر الهندسي لحديد السملات باستخدام برنامج ASD



Notes:

1. THE COPYRIGHT OF THIS DRAWING IS VESTED IN YOURSPREADSHEETS AND IT MAY NOT BE REPRODUCED IN WHOLE OR PART OR USED FOR THE MANUFACTURE OF ANY ARTICLE WITHOUT THE EXPRESS PERMISSION OF THE COPYRIGHT HOLDERS.
2. WORK TO DIMENSIONS ONLY.

Key plane

Before

Instructor :

YourSpreadsheets

Address line 1
Address line 2
Telephone line 1
Fax line 1
www.YourSpreadsheets.co.uk

CLIENT: BAH i CLIENT
3 Mossadak, Ad Doqi, Dokki,
Giza Governorate, Giza,
Egypt

ARCHITECT: Amr Mamdoh
40 Mossadak, Ad Doqi, Dokki,
Giza Governorate, Giza,
Egypt

SITE: 31 ROVER ROAD
BLOCK A AND B

TITLE: RC DETAILS AND SECTIONS
OF GROUND BEAMS

SCALE AT AS: 1:50, 1:100	DATE: 05/09/13	DRAWN: DJ	CHECKED: DJ
PROJECT NO: 24567	DRAWING NO: A2/248	REVISION: C	

B.B.S

Number

Position	Diameter	in the element	of elements	Symbol (m)	Length (m)	Total mass (kg)
01	16	3	7	10,8	10.8	358.34
02	16	3	7	300,0 10,8	11.3	375.76
03	10	30	7	100,0 400,0 150,0	1.2	158.72

B.B.S

T	Ø 10	Ø 16
Unit weight (kg/m)	0.62	1.58
Total length (m)	257.3	464.6
Total weight (kg)	158.72	734.11

الحصر الهندسي لحديد السملات باستخدام برنامج ASD



Notes:

1. THE COPYRIGHT OF THIS DRAWING IS VESTED IN YOURSPREADSHEETS AND IT MAY NOT BE REPRODUCED IN WHOLE OR PART OR USED FOR THE MANUFACTURE OF ANY ARTICLE WITHOUT THE EXPRESS PERMISSION OF THE COPYRIGHT HOLDERS.
2. WORK TO DIMENSIONS ONLY.

Key plane

Before

Instructor :

YourSpreadsheets

Address line 1
Address line 2
Telephone line 1
Fax line 1
www.YourSpreadsheets.co.uk


CLIENT: BAH i CLIENT
3 Mossadak, Ad Doqi, Dokki,
Giza Governorate, Giza,
Egypt

ARCHITECT: Amr Mamdoh
40 Mossadak, Ad Doqi, Dokki,
Giza Governorate, Giza,
Egypt

SITE: 31 ROVER ROAD
BLOCK A AND B

TITLE: RC DETAILS AND SECTIONS
OF GROUND BEAMS

SCALE AT AS: 1:50, 1:100	DATE: 05/09/13	DRAWN: DJ	CHECKED: DJ
PROJECT NO: 24567	DRAWING NO: A2/248	REVISION: C	

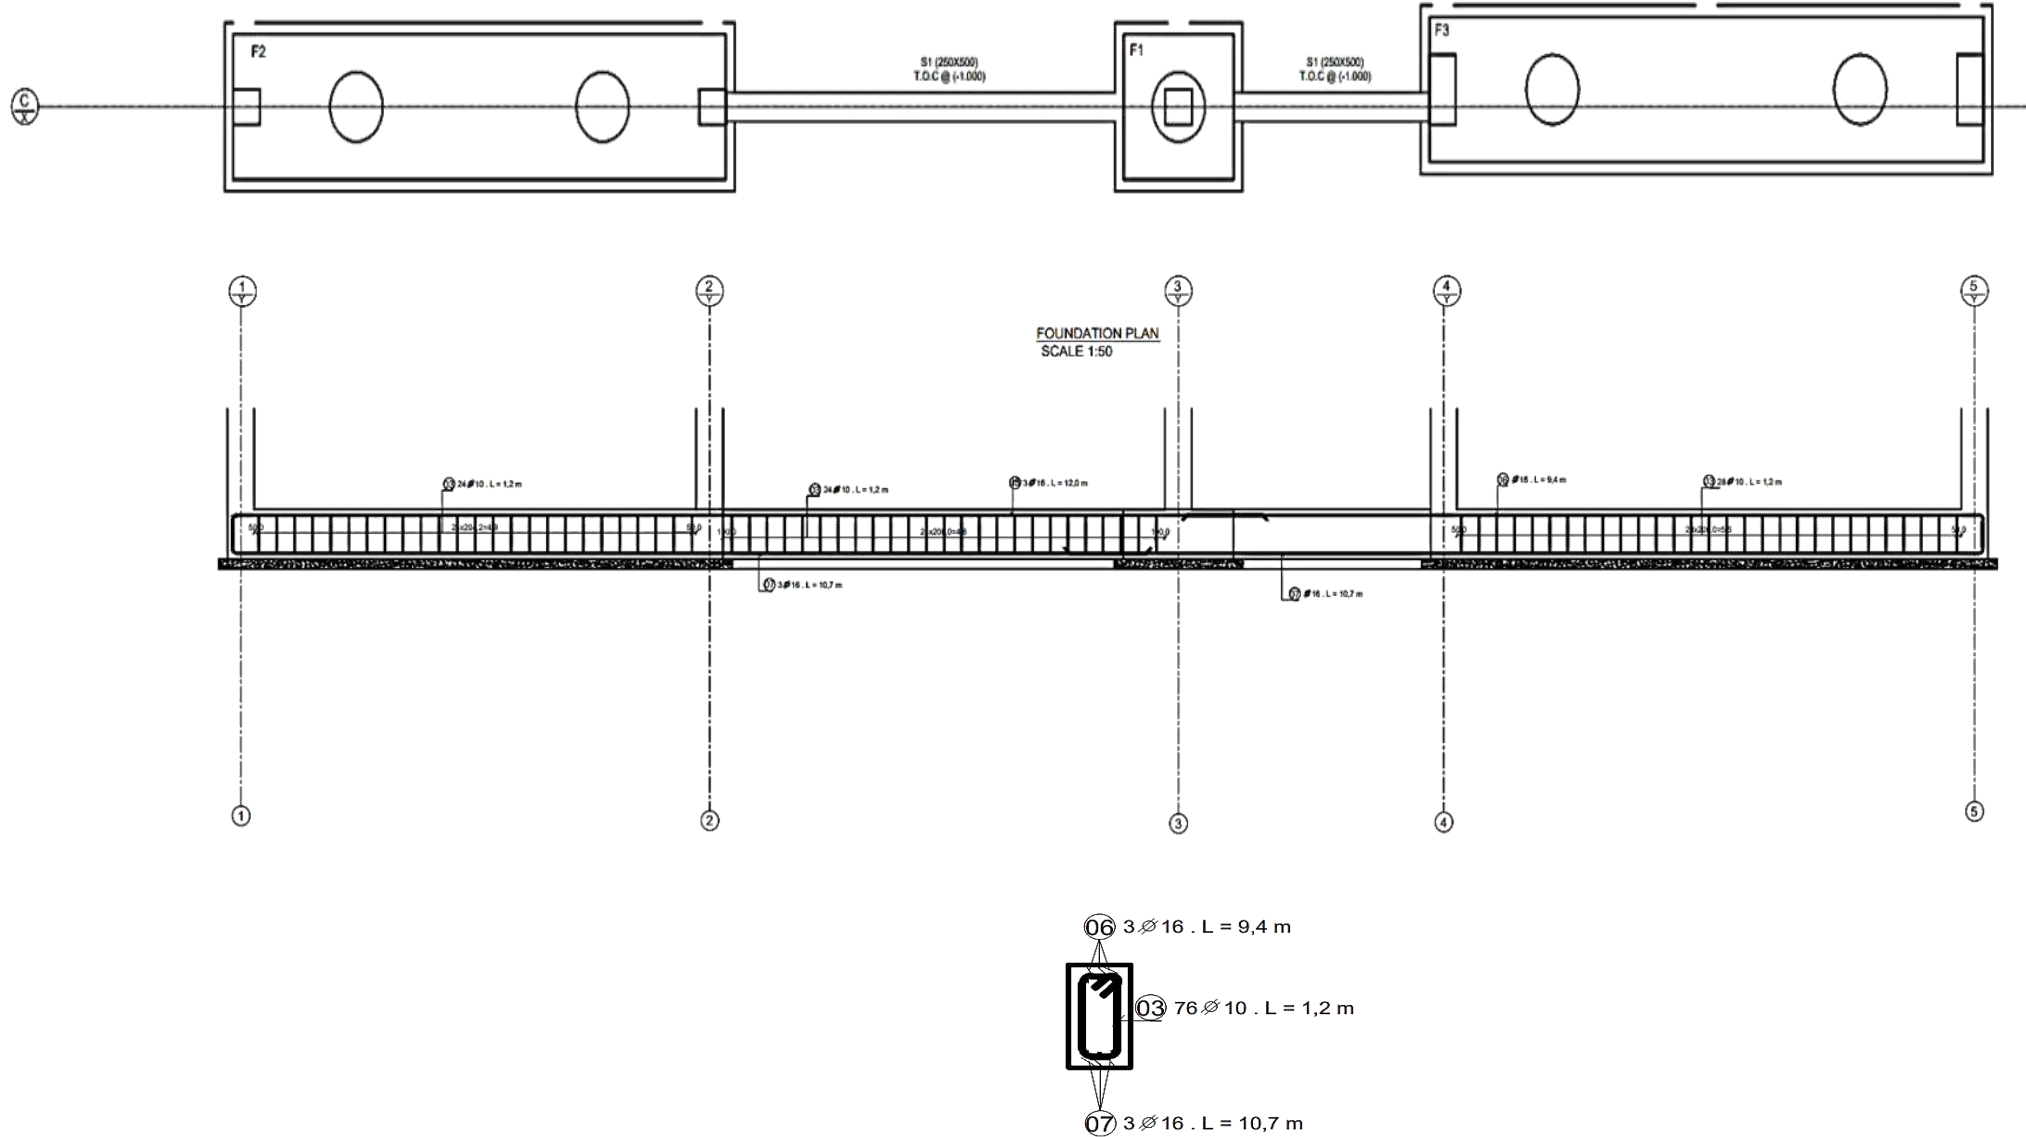

الحصر الهندسي لحديد السملات باستخدام برنامج ASD



Notes:

1. THE COPYRIGHT OF THIS DRAWING IS VESTED IN YOURSPREADSHEETS AND IT MAY NOT BE REPRODUCED IN WHOLE OR PART OR USED FOR THE MANUFACTURE OF ANY ARTICLE WITHOUT THE EXPRESS PERMISSION OF THE COPYRIGHT HOLDERS.
2. WORK TO DIMENSIONED DIMENSIONS ONLY.

Key plane

Before

Instructor :

YourSpreadsheets

Address line 1
Address line 2
Telephone line 1
Fax line 1
www.YourSpreadsheets.co.uk

CLIENT: BAH i CLIENT
3 Mossadak, Ad Doqi, Dokki,
Giza Governorate, Giza,
Egypt

ARCHITECT: Amr Mamdoh
40 Mossadak, Ad Doqi, Dokki,
Giza Governorate, Giza,
Egypt

SITE: 31 ROVER ROAD
BLOCK A AND B

TITLE: RC DETAILS AND SECTIONS
OF GROUND BEAMS

SCALE AT AS: 1:50, 1:100	DATE: 05/09/13	DRAWN: DJ	CHECKED: DJ
PROJECT NO: 24567	DRAWING NO: A2/248	REVISION: C	

B.B.S

Number

Position	Diameter	in the element	of elements	Symbol (m)	Length (m)	Total mass (kg)
03	10	106	1		1.2	80.12
05	16	3	1		12.3	58.42
06	16	1	1		9.7	15.29
07	16	4	1		11.0	69.52

B.B.S

T	10	16
Unit weight (kg/m)	0.62	1.58
Total length (m)	129.8	88.0
Total weight (kg)	80.12	139.12

الحصر الهندسي لحديد السملات باستخدام برنامج ASD



Notes:

1. THE COPYRIGHT OF THIS DRAWING IS VESTED IN YOURSPREADSHEETS AND IT MAY NOT BE REPRODUCED IN WHOLE OR PART OR USED FOR THE MANUFACTURE OF ANY ARTICLE WITHOUT THE EXPRESS PERMISSION OF THE COPYRIGHT HOLDERS.
2. WORK TO FIGURED DIMENSIONS ONLY.

Key plane

Before

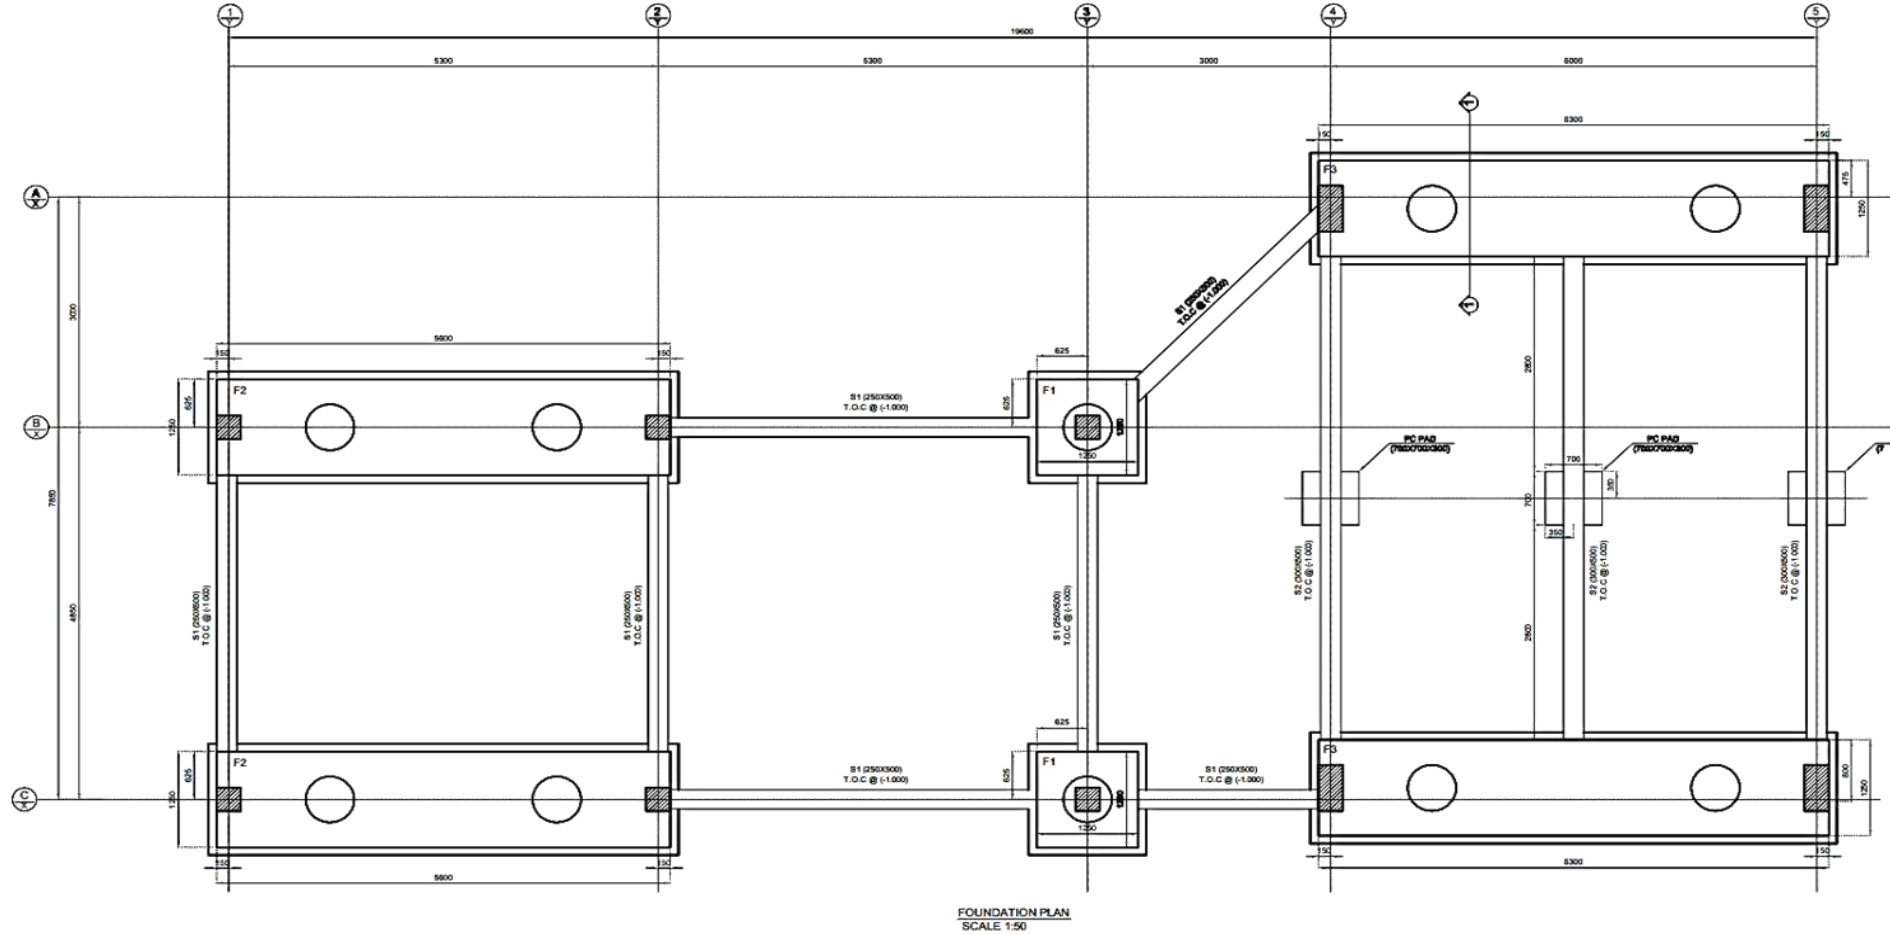


TABLE 1 PILE CAPS REINFORCEMENT AND DIMENSIONS

MODEL	P.C				R.C				TOP RFT.		BOTTOM RFT.		REMARKS
	LENGTH	BREDTH	DEPTH	T.O.PC	LENGTH	BREDTH	DEPTH	T.O.C	TRANSVERSAL	LONGITUDINAL	TRANSVERSAL	LONGITUDINAL	
F1	1450	1450	100	(-1.50)	1250	1250	500	(-1.00)	Ø 16 @ 200 mm	Ø 16 @ 200 mm	Ø 16 @ 200 mm	Ø 16 @ 200 mm	-----
F2	1450	5800	100	(-1.50)	1250	5600	500	(-1.00)	Ø 16 @ 200 mm	Ø 18 @ 100 mm	Ø 16 @ 200 mm	Ø 16 @ 200 mm	-----
F3	1450	6500	100	(-1.50)	1250	6300	500	(-1.00)	Ø 16 @ 200 mm	Ø 18 @ 100 mm	Ø 16 @ 200 mm	Ø 16 @ 200 mm	-----

Instructor :

YourSpreadsheets

Address line 1
Address line 2
Telephone line 1
Fax line 1
www.YourSpreadsheets.co.uk

CLIENT: BAH i CLIENT
3 Mossadak, Ad Doqi, Dokki,
Giza Governorate, Giza,
Egypt

ARCHITECT: Amr Mamdoh
40 Mossadak, Ad Doqi, Dokki,
Giza Governorate, Giza,
Egypt

SITE: 31 ROVER ROAD
BLOCK A AND B

TITLE: RC DETAILS AND SECTIONS
OF GROUND BEAMS

SCALE AT A2: 1:50, 1:100
DATE: 05/09/13
DRAWN: DJ
PROJECT NO: 24567
DRAWING NO: A2/248
CHECKED: DJ
REVISION: C

THE END

COURSE: TECHNICAL OFFICE G46

Name: Ibrahim Mohamed Read

Eng: Amr Mamdouh

Lecture: 18

Task: 15

لوحة الحصر الهندسي لتحديد الأعمدة باستخدام برنامج ASD



Notes:

1. THE COPYRIGHT OF THIS DRAWING IS VESTED IN YOURSPREADSHEETS AND IT MAY NOT BE REPRODUCED IN WHOLE OR PART OR USED FOR THE MANUFACTURE OF ANY ARTICLE WITHOUT THE EXPRESS PERMISSION OF THE COPYRIGHT HOLDERS.
2. WORK TO FIGURED DIMENSIONS ONLY.

Key plane

Before

Instructor :

YourSpreadsheets

Address line 1
Address line 2
Telephone line 1
Fax line 1
www.YourSpreadsheets.co.uk



CLIENT:
BAHI CLIENT
3 Mossadak, Ad Doqi, Dokki,
Giza Governorate, Giza,
Egypt

ARCHITECT:
Amr Mamdoh
40 Mossadak, Ad Doqi, Dokki,
Giza Governorate, Giza,
Egypt

SITE:
31 ROVER ROAD
BLOCK A AND B

TITLE:
RC DETAILS AND SECTIONS
OF GROUND BEAMS

SCALE AT A2: 1:50, 1:100	DATE: 05/09/13	DRAWN: DJ	CHECKED: DJ
PROJECT NO: 24567	DRAWING NO: A2/248	REVISION: C	

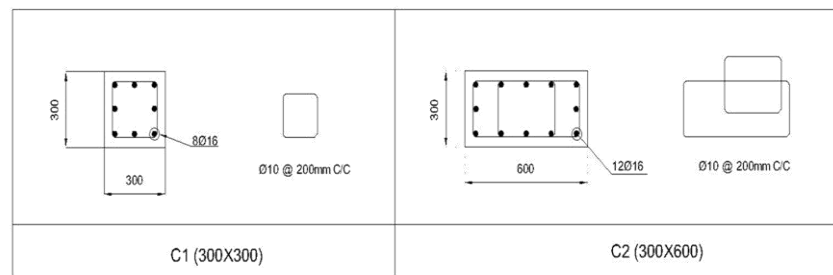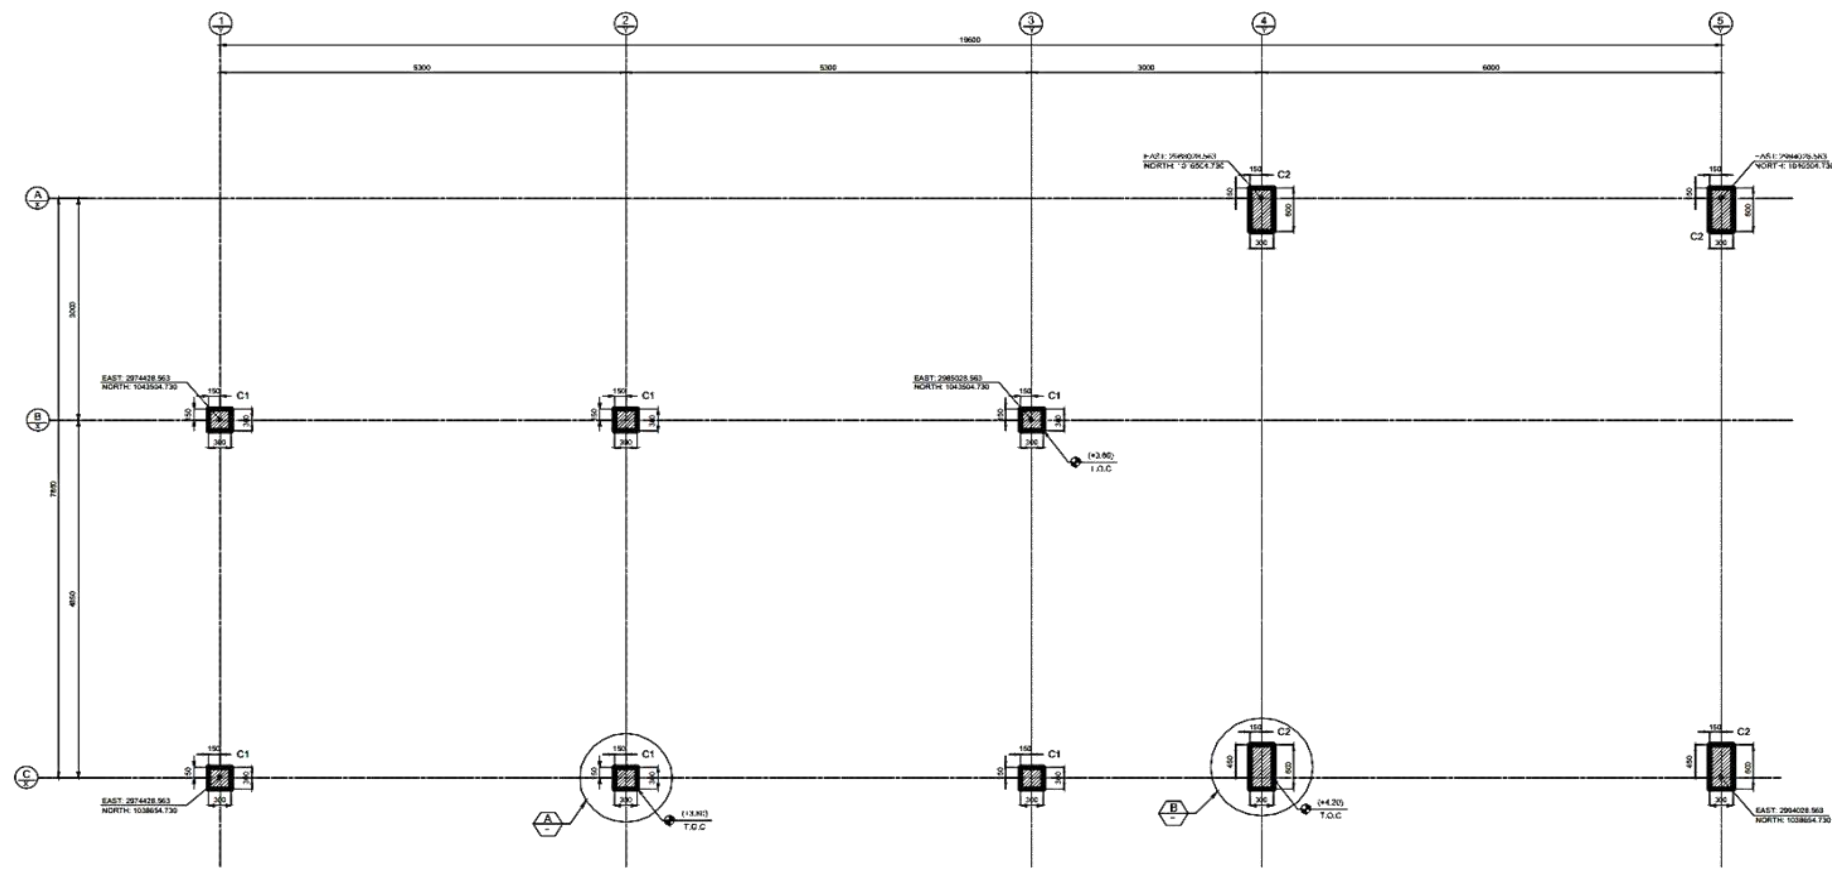

A DETAIL (C1)
Scale 1 : 25

B DETAIL (C2)
Scale 1 : 25

الحصر الهندسي لحديد الأعمدة باستخدام برنامج ASD




Notes:

1. THE COPYRIGHT OF THIS DRAWING IS VESTED IN YOURSPREADSHEETS AND IT MAY NOT BE REPRODUCED IN WHOLE OR PART OR USED FOR THE MANUFACTURE OF ANY ARTICLE WITHOUT THE EXPRESS PERMISSION OF THE COPYRIGHT HOLDERS.
2. WORK TO DIMENSIONS ONLY.

Key plane

Before

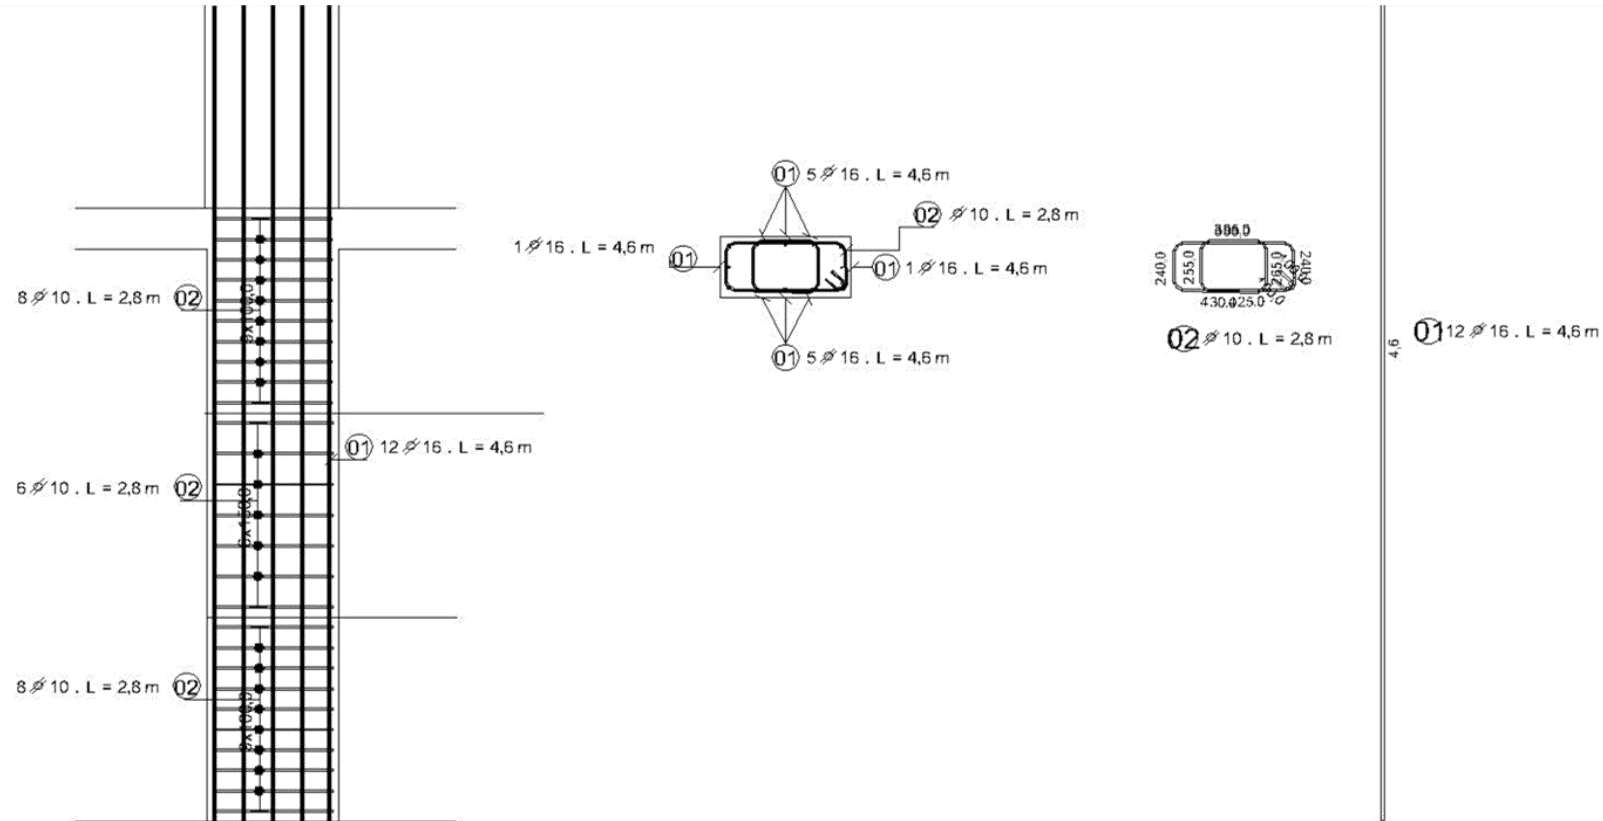

B.B.S					
Position	Diameter	Number		Symbol (m)	Length (m)
		in the element	of elements		
01	16	24	1	—	4.6
02	10	2	1		3.0

B.B.S		
T	$\varnothing 10$	$\varnothing 16$
Unit weight (kg/m)	0.62	1.58
Total length (m)	7.8	175.0
Total weight (kg)	4.78	276.50

Instructor :

YourSpreadsheets

Address line 1
Address line 2
Telephone line 1
Fax line 1
www.YourSpreadsheets.co.uk

CLIENT: **BAHI CLIENT**
3 Mossadak, Ad Doqi, Dokki,
Giza Governorate, Giza,
Egypt


ARCHITECT: **Amr Mamdoh**
40 Mossadak, Ad Doqi, Dokki,
Giza Governorate, Giza,
Egypt

SITE: **31 ROVER ROAD
BLOCK A AND B**

TITLE: **RC DETAILS AND SECTIONS
OF GROUND BEAMS**

SCALE AT A2: 1:50, 1:100	DATE: 05/09/13	DRAWN: DJ	CHECKED: DJ
PROJECT NO: 24567	DRAWING NO: A2/248	REVISION: C	

الحصر الهندسي لحديد الأعمدة باستخدام برنامج ASD

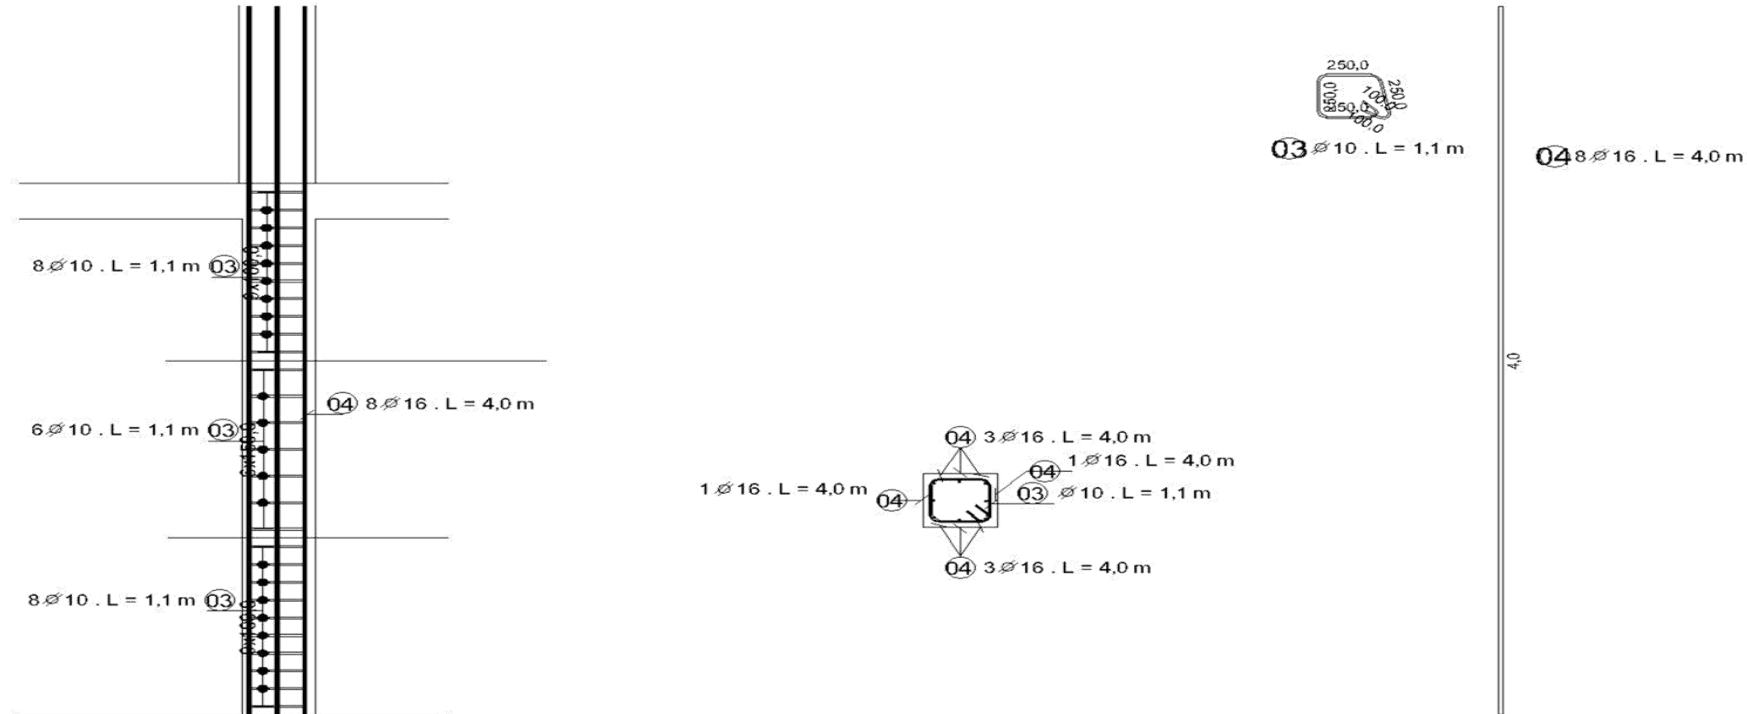

B.B.S						
Position	Diameter	Number		Symbol (m)	Length (m)	Total mass (kg)
		in the element	of elements			
03	10	2	1		1.1	1.39
04	16	16	1		4.0	101.12

B.B.S		
T	Ø 10	Ø 16
Unit weight (kg/m)	0.62	1.58
Total length (m)	7.8	175.0
Total weight (kg)	4.78	276.50



Notes:

1. THE COPYRIGHT OF THIS DRAWING IS VESTED IN YOURSPREADSHEETS AND IT MAY NOT BE REPRODUCED IN WHOLE OR PART OR USED FOR THE MANUFACTURE OF ANY ARTICLE WITHOUT THE EXPRESS PERMISSION OF THE COPYRIGHT HOLDERS.
2. WORK TO FIGURED DIMENSIONS ONLY.

Key plane

Before

Instructor :

YourSpreadsheets

Address line 1
Address line 2
Telephone line 1
Fax line 1
www.YourSpreadsheets.co.uk

CLIENT: **BAHI CLIENT**
3 Mossadak, Ad Doqi, Dokki,
Giza Governorate, Giza,
Egypt

ARCHITECT: **Amr Mamdoh**
40 Mossadak, Ad Doqi, Dokki,
Giza Governorate, Giza,
Egypt

SITE: **31 ROVER ROAD
BLOCK A AND B**

TITLE: **RC DETAILS AND SECTIONS
OF GROUND BEAMS**

SCALE AT A2: 1:50, 1:100	DATE: 05/09/13	DRAWN: DJ	CHECKED: DJ
PROJECT NO: 24567	DRAWING NO: A2/248	REVISION: C	

الحصر الهندسي لحديد الأعمدة باستخدام برنامج ASD



Notes:

1. THE COPYRIGHT OF THIS DRAWING IS VESTED IN YOURSPREADSHEETS AND IT MAY NOT BE REPRODUCED IN WHOLE OR PART OR USED FOR THE MANUFACTURE OF ANY ARTICLE WITHOUT THE EXPRESS PERMISSION OF THE COPYRIGHT HOLDERS.
2. WORK TO FIGURED DIMENSIONS ONLY.

Key plane

Before

Instructor :

YourSpreadsheets

Address line 1
Address line 2
Telephone line 1
Fax line 1
www.YourSpreadsheets.co.uk


CLIENT: **BAHI CLIENT**
3 Mossadak, Ad Doqi, Dokki,
Giza Governorate, Giza,
Egypt

ARCHITECT: **Amr Mamdoh**
40 Mossadak, Ad Doqi, Dokki,
Giza Governorate, Giza,
Egypt

SITE: **31 ROVER ROAD
BLOCK A AND B**

TITLE: **RC DETAILS AND SECTIONS
OF GROUND BEAMS**

SCALE AT A2: 1:50, 1:100	DATE: 05/09/13	DRAWN: DJ	CHECKED: DJ
PROJECT NO: 24567	DRAWING NO: A2/248	REVISION: C	

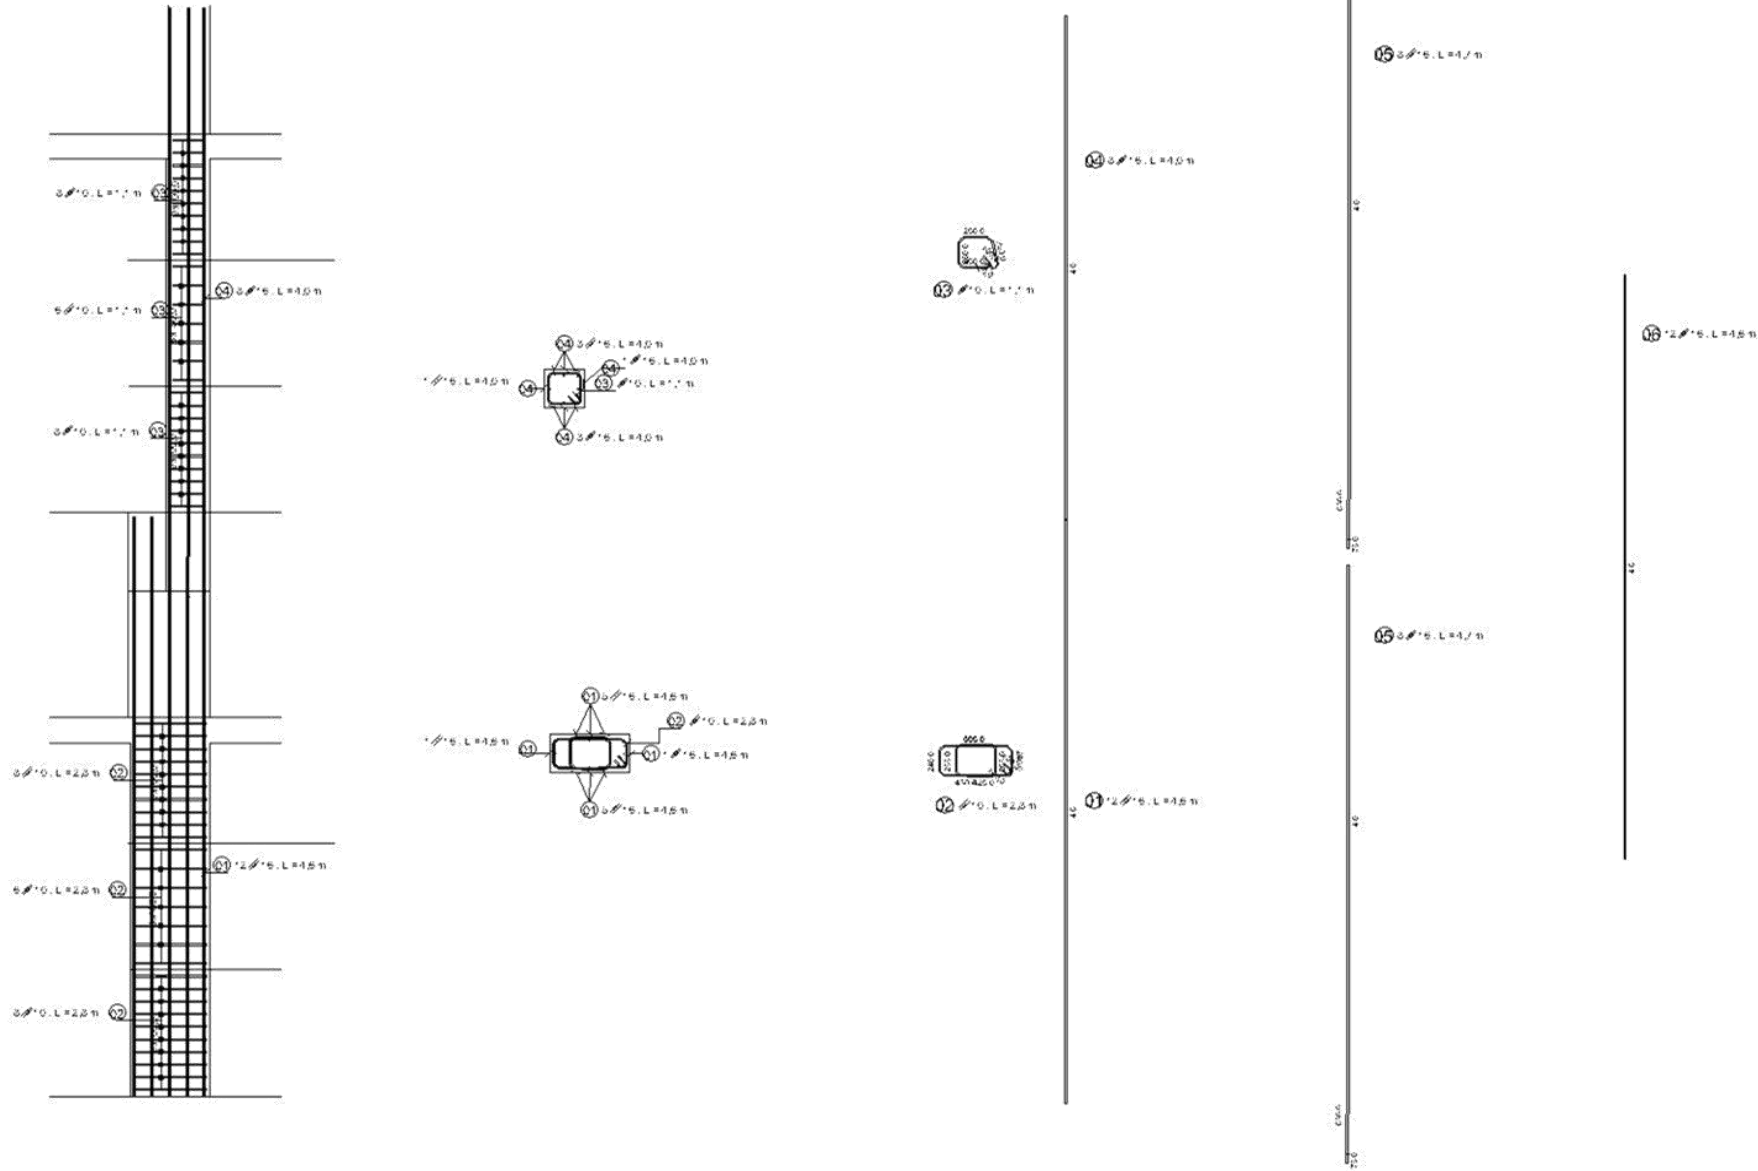

الحصر الهندسي لحديد الأعمدة باستخدام برنامج ASD



Notes:

1. THE COPYRIGHT OF THIS DRAWING IS VESTED IN YOURSPREADSHEETS AND IT MAY NOT BE REPRODUCED IN WHOLE OR PART OR USED FOR THE MANUFACTURE OF ANY ARTICLE WITHOUT THE EXPRESS PERMISSION OF THE COPYRIGHT HOLDERS.
2. WORK TO DIMENSIONS ONLY.

Key plane

Before

Instructor :

YourSpreadsheets

Address line 1
Address line 2
Telephone line 1
Fax line 1
www.YourSpreadsheets.co.uk

CLIENT: BAHİ CLIENT
3 Mossadak, Ad Doqi, Dokki,
Giza Governorate, Giza,
Egypt

ARCHITECT: Amr Mamdoh
40 Mossadak, Ad Doqi, Dokki,
Giza Governorate, Giza,
Egypt

SITE: 31 ROVER ROAD
BLOCK A AND B

TITLE: RC DETAILS AND SECTIONS
OF GROUND BEAMS

SCALE AT AS: 1:50, 1:100	DATE: 05/09/13	DRAWN: DJ	CHECKED: DJ
PROJECT NO: 24567	DRAWING NO: A2/248	REVISION: C	

B.B.S						
Position	Diameter	Number		Symbol (m)	Length (m)	Total mass (kg)
		in the element	of elements			
01	16	24	1		4.6	175.38
02	10	2	1		3.0	3.64
03	10	2	1		1.1	1.39
04	16	16	1		4.0	101.12

B.B.S		
T	10	16
Unit weight (kg/m)	0.62	1.58
Total length (m)	7.8	175.0
Total weight (kg)	4.78	276.50

THE END

COURSE: TECHNICAL OFFICE G46

Name: Ibrahim Mohamed Read

Eng: Amr Mamdouh

Lecture: 19

Task: 16

لوحة الحصر الهندسي لحديد Solid Slab باستخدام برنامج ASD

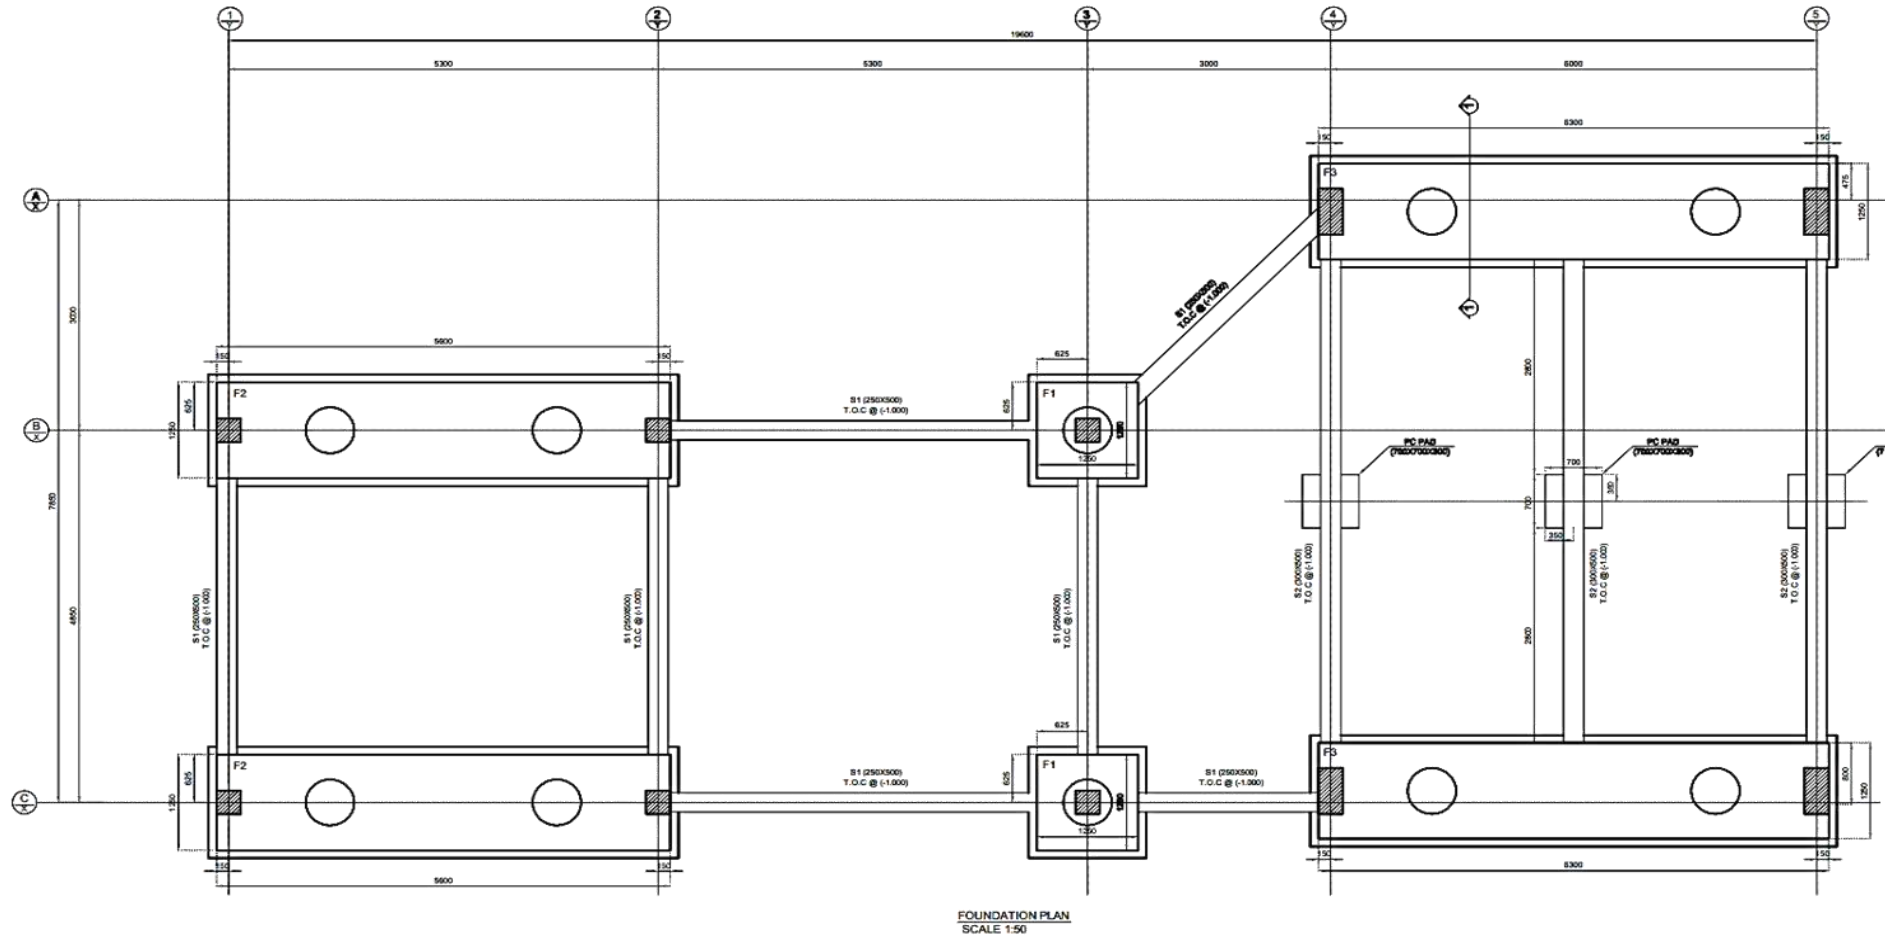


TABLE 1 PILE CAPS REINFORCEMENT AND DIMENSIONS

MODEL	P.C				R.C				TOP RFT.		BOTTOM RFT.		REMARKS
	LENGTH	BREDTH	DEPTH	T.O.PC	LENGTH	BREDTH	DEPTH	T.O.C	TRANSVERSAL	LONGITUDINAL	TRANSVERSAL	LONGITUDINAL	
F1	1450	1450	100	(-1.50)	1250	1250	500	(-1.00)	Ø 16 @ 200 mm	Ø 16 @ 200 mm	Ø 16 @ 200 mm	Ø 16 @ 200 mm	-----
F2	1450	5800	100	(-1.50)	1250	5600	500	(-1.00)	Ø 16 @ 200 mm	Ø 18 @ 100 mm	Ø 16 @ 200 mm	Ø 16 @ 200 mm	-----
F3	1450	6500	100	(-1.50)	1250	6300	500	(-1.00)	Ø 16 @ 200 mm	Ø 18 @ 100 mm	Ø 16 @ 200 mm	Ø 16 @ 200 mm	-----



Notes:

1. THE COPYRIGHT OF THIS DRAWING IS VESTED IN YOURSPREADSHEETS AND IT MAY NOT BE REPRODUCED IN WHOLE OR PART OR USED FOR THE MANUFACTURE OF ANY ARTICLE WITHOUT THE EXPRESS PERMISSION OF THE COPYRIGHT HOLDERS.
2. WORK TO FIGURED DIMENSIONS ONLY.

Key plane

Before

Instructor :

YourSpreadsheets

Address line 1
Address line 2
Telephone line 1
Fax line 1
www.YourSpreadsheets.co.uk

CLIENT: BAHİ CLIENT
3 Mossadak, Ad Doqi, Dokki,
Giza Governorate, Giza,
Egypt

ARCHITECT: Amr Mamdoh
40 Mossadak, Ad Doqi, Dokki,
Giza Governorate, Giza,
Egypt

SITE: 31 ROVER ROAD
BLOCK A AND B

TITLE: RC DETAILS AND SECTIONS
OF GROUND BEAMS

SCALE AT A2: 1:50, 1:100
DATE: 05/09/13
DRAWN: DJ
CHECKED: DJ
PROJECT NO: 24567
DRAWING NO: A2/248
REVISION: C

الحصر الهندسي لحديد Solid Slab باستخدام برنامج ASD




Notes:

1. THE COPYRIGHT OF THIS DRAWING IS VESTED IN YOURSPREADSHEETS AND IT MAY NOT BE REPRODUCED IN WHOLE OR PART OR USED FOR THE MANUFACTURE OF ANY ARTICLE WITHOUT THE EXPRESS PERMISSION OF THE COPYRIGHT HOLDERS.
2. WORK TO FIGURED DIMENSIONS ONLY.

Key plane

Before

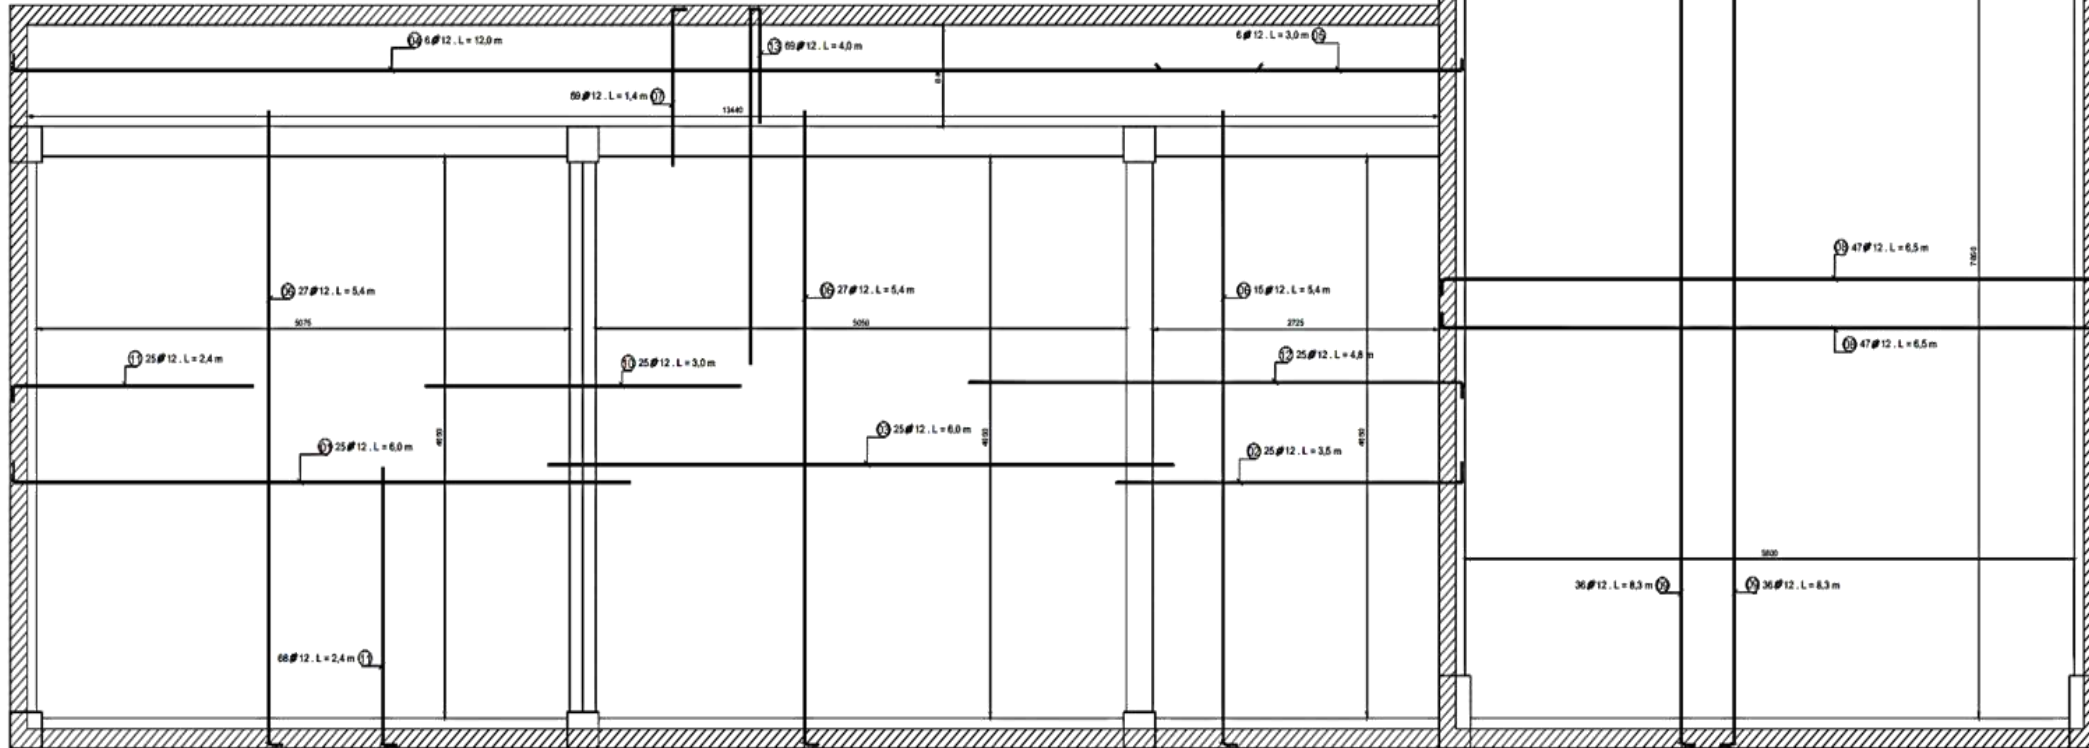

Instructor :

YourSpreadsheets

Address line 1
Address line 2
Telephone line 1
Fax line 1
www.YourSpreadsheets.co.uk

CLIENT: BAH i CUENT
3 Mossadak, Ad Doqi, Dokki,
Giza Governorate, Giza,
Egypt

ARCHITECT: Amr Mamdoh
40 Mossadak, Ad Doqi, Dokki,
Giza Governorate, Giza,
Egypt

SITE: 31 ROVER ROAD
BLOCK A AND B

TITLE: RC DETAILS AND SECTIONS
OF GROUND BEAMS

SCALE AT AS: 1:50, 1:100	DATE: 05/09/13	DRAWN: DJ	CHECKED: DJ
PROJECT NO: 24567	DRAWING NO: A2/248	REVISION: C	

الحصر الهندسي لحديد Solid Slab باستخدام برنامج ASD



Notes:

1. THE COPYRIGHT OF THIS DRAWING IS VESTED IN YOURSPREADSHEETS AND IT MAY NOT BE REPRODUCED IN WHOLE OR PART OR USED FOR THE MANUFACTURE OF ANY ARTICLE WITHOUT THE EXPRESS PERMISSION OF THE COPYRIGHT HOLDERS.
2. WORK TO DIMENSIONS ONLY.

Key plane

Before

Instructor :

YourSpreadsheets

Address line 1
Address line 2
Telephone line 1
Fax line 1
www.YourSpreadsheets.co.uk

CLIENT: BAH I CLIENT
3 Mossadak, Ad Doqi, Dokki,
Giza Governorate, Giza,
Egypt

ARCHITECT: Amr Mamdoh
40 Mossadak, Ad Doqi, Dokki,
Giza Governorate, Giza,
Egypt

SITE: 31 ROVER ROAD
BLOCK A AND B

TITLE: RC DETAILS AND SECTIONS
OF GROUND BEAMS

SCALE AT AS: 1:50, 1:100	DATE: 05/09/13	DRAWN: DJ	CHECKED: DJ
PROJECT NO: 24567	DRAWING NO: A2/248	REVISION: C	

B.B.S						
Position	Diameter	Number		Symbol (m)	Length (m)	Total mass (kg)
		in the element	of elements			
01	12	25	1	180,0 5,9	6.0	133.76
02	12	25	1	180,0 3,3	3.5	76.59
03	12	25	1	6,0	6.0	132.09
04	12	6	1	135,0 11,9	12.0	63.94
05	12	6	1	2,9 100,0	3.0	15.85
06	12	69	1	135,0 5,3	5.4	327.81
07	12	69	1	135,0 1,3	1.4	85.78
08	12	94	1	135,0 6,3	6.5	540.48
09	12	72	1	135,0 8,1	8.3	532.27
10	12	25	1	3,0	3.0	66.60
11	12	93	1	135,0 2,3	2.4	198.20
12	12	25	1	135,0 4,7	4.8	106.56
13	12	69	1	950,0 100,0 3,0	4.0	242.02

THE END

COURSE: TECHNICAL OFFICE G46


Name: Ibrahim Mohamed Read

Eng: Amr Mamdouh

Lecture: 20

Task: 17

لوحة الحصر الهندسي لحديد Flat Slab باستخدام برنامج ASD

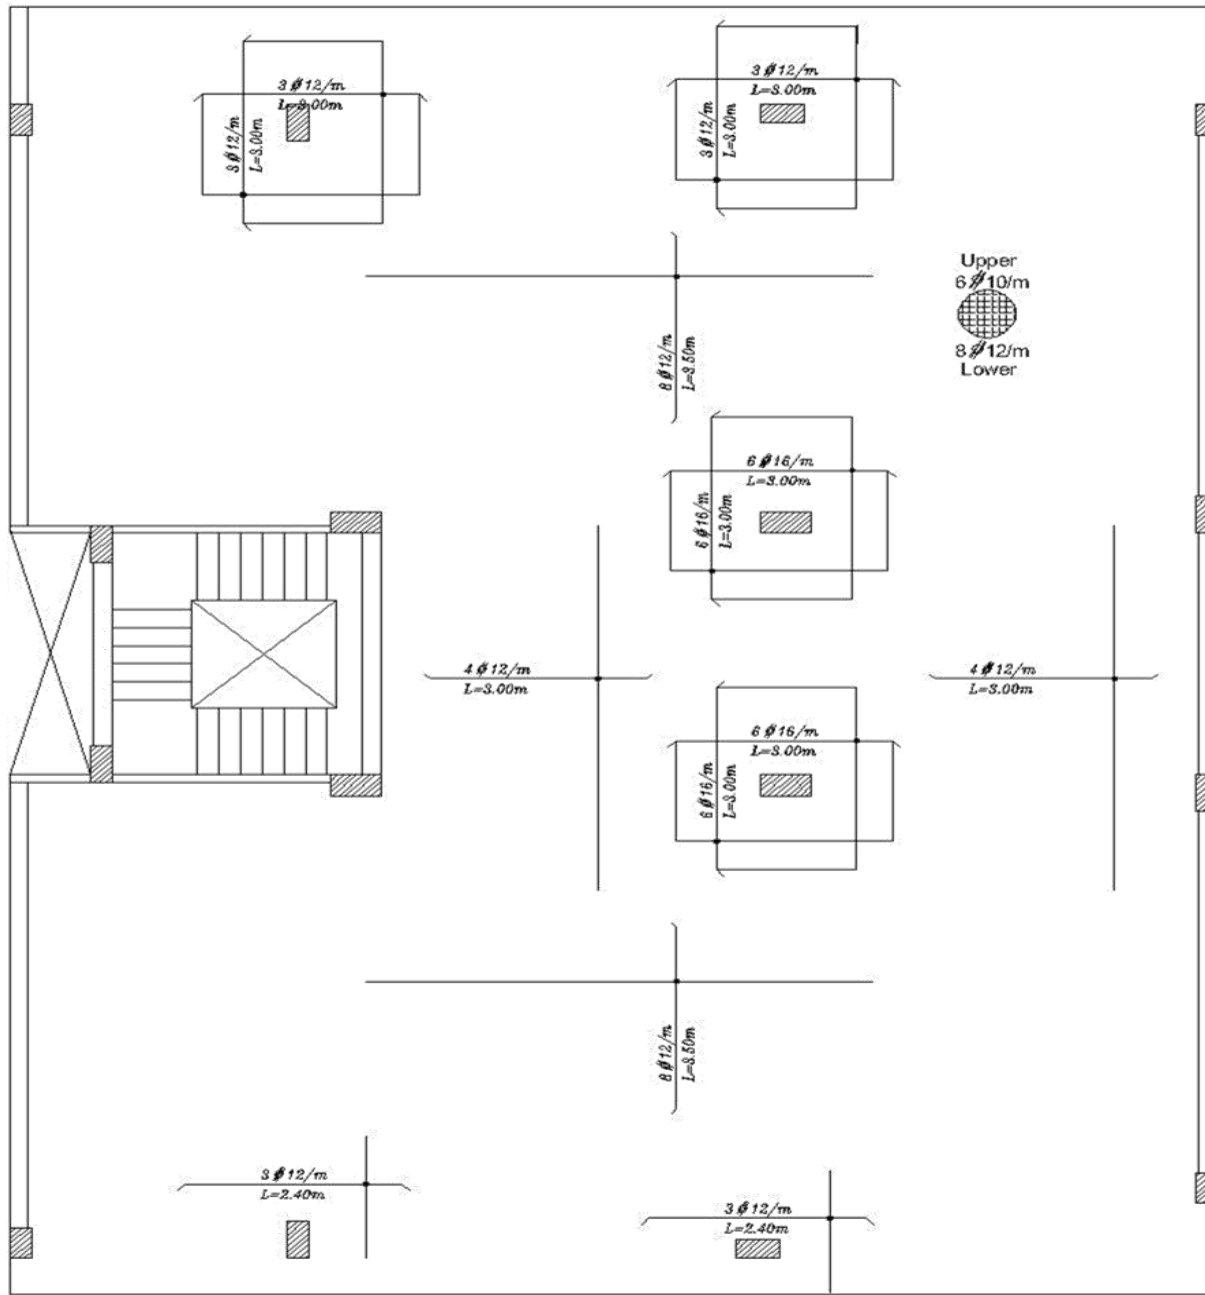

Notes:

1. THE COPYRIGHT OF THIS DRAWING IS VESTED IN YOURSPREADSHEETS AND IT MAY NOT BE REPRODUCED IN WHOLE OR PART OR USED FOR THE MANUFACTURE OF ANY ARTICLE WITHOUT THE EXPRESS PERMISSION OF THE COPYRIGHT HOLDERS.
2. WORK TO PROVIDED DIMENSIONS ONLY.

Key plane

Before

Instructor :

YourSpreadsheets

Address line 1
Address line 2
Telephone line 1
Fax line 1
www.YourSpreadsheets.co.uk

CLIENT: **BAHI CUENT**
3 Mossadok, Ad Doqi, Dokki,
Giza Governorate, Giza,
Egypt


ARCHITECT: **Amr Mamdoh**
40 Mossadok, Ad Doqi, Dokki,
Giza Governorate, Giza,
Egypt

SITE: **31 ROVER ROAD**
BLOCK A AND B

TITLE: **RC DETAILS AND SECTIONS**
OF GROUND BEAMS

SCALE AT A2:	DATE:	DRAWN:	CHECKED:
1:50, 1:100	05/09/13	DJ	DJ
PROJECT NO:	DRAWING NO:	REVISION:	
24567	A2/248	C	

الحصر الهندسي لحديد Flat Slab باستخدام برنامج ASD حصر اضافي سفلي وعلوي في اتجاه x واتجاه y

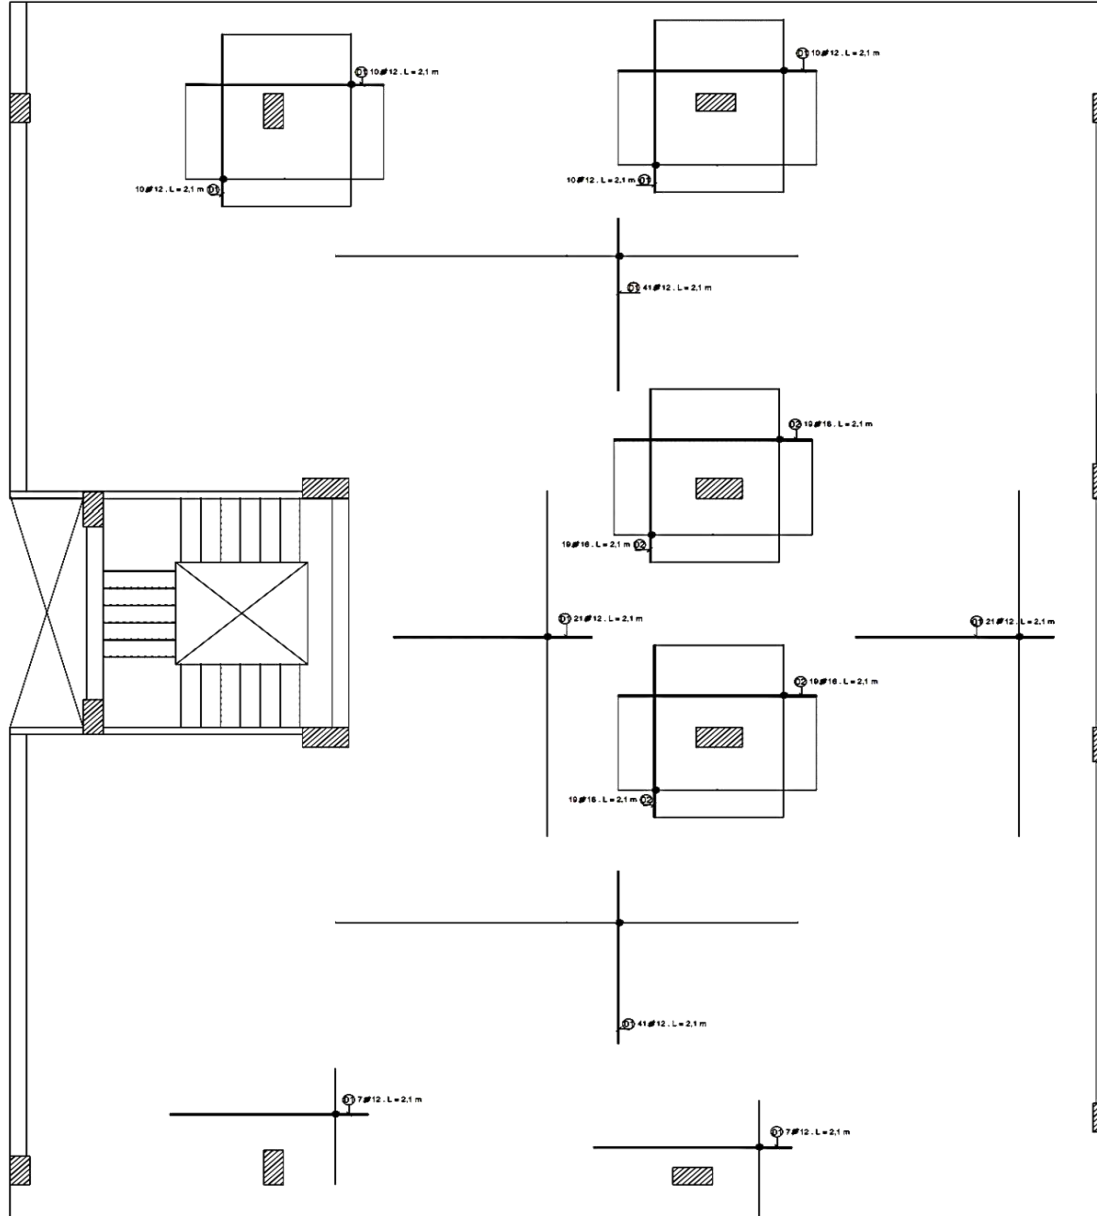

Notes:

1. THE COPYRIGHT OF THIS DRAWING IS VESTED IN YOURSPREADSHEETS AND IT MAY NOT BE REPRODUCED IN WHOLE OR PART OR USED FOR THE MANUFACTURE OF ANY ARTICLE WITHOUT THE EXPRESS PERMISSION OF THE COPYRIGHT HOLDERS.
2. WORK TO POURED DIMENSIONS ONLY.

Key plane

Before

Instructor :

YourSpreadsheets

Address line 1
Address line 2
Telephone line 1
Fax line 1
www.YourSpreadsheets.co.uk

CLIENT: **BAH i CUENT**
3 Mossadak, Ad Doqi, Dokki,
Giza Governorate, Giza,
EGYPT


ARCHITECT: **Amr Mamdoh**
40 Mossadak, Ad Doqi, Dokki,
Giza Governorate, Giza,
EGYPT

SITE: **31 ROVER ROAD
BLOCK A AND B**

TITLE: **RC DETAILS AND SECTIONS
OF GROUND BEAMS**

SCALE AT A2: 1:50, 1:100	DATE: 05/09/13	DRAWN: DJ	CHECKED: DJ
PROJECT NO: 24567	DRAWING NO: A2/248	REVISION: C	

الحصر الهندسي لحديد Flat Slab باستخدام برنامج ASD حصر شبكة التسليح السفلي

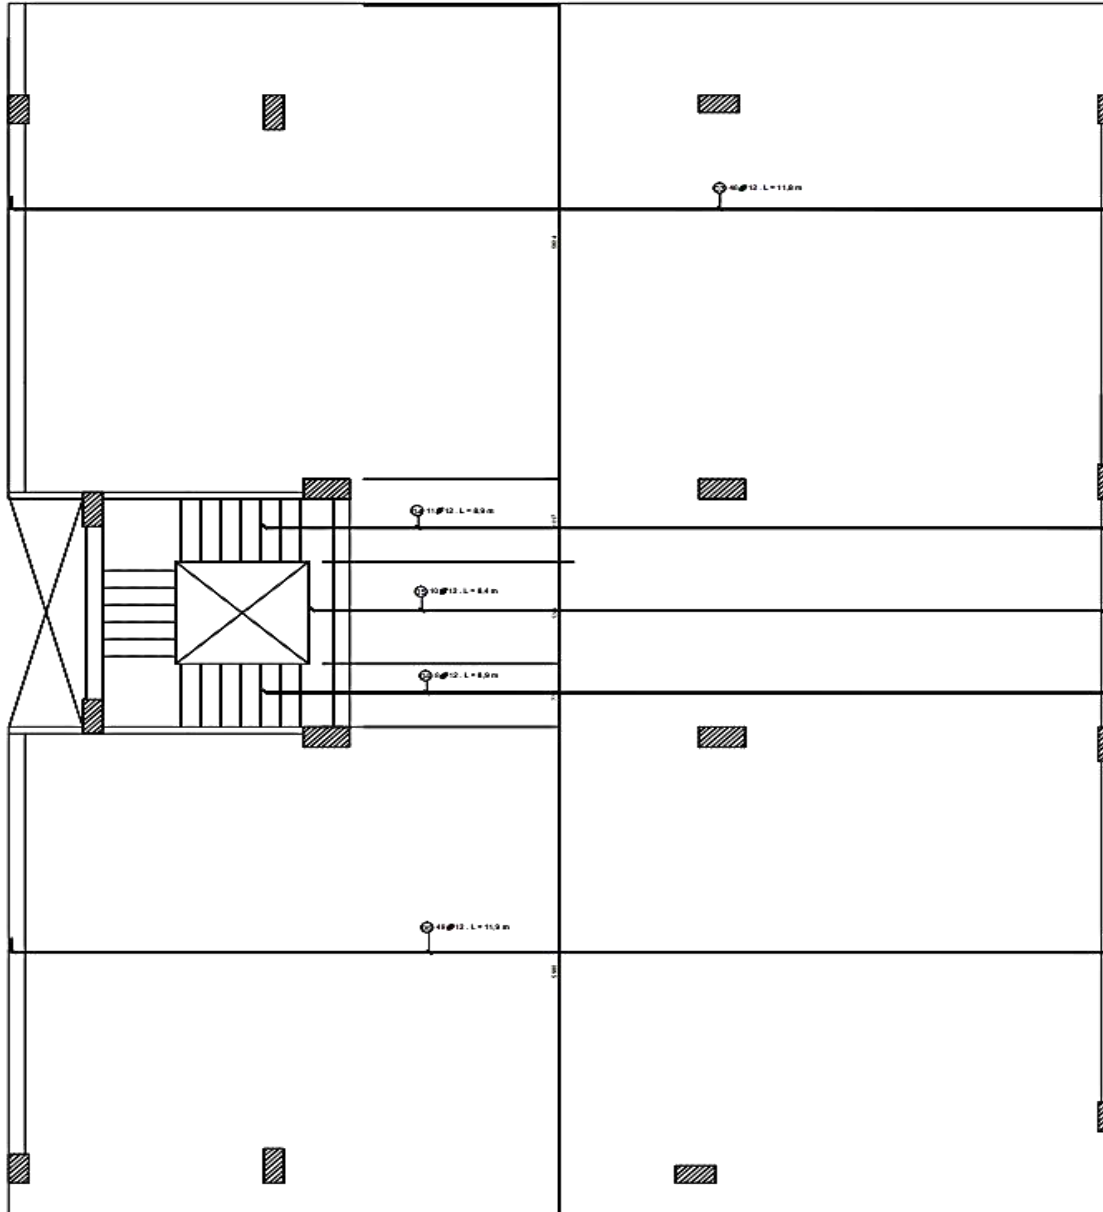

Notes:

1. THE COPYRIGHT OF THIS DRAWING IS VESTED IN YOURSPREADSHEETS AND IT MAY NOT BE REPRODUCED IN WHOLE OR PART OR USED FOR THE MANUFACTURE OF ANY ARTICLE WITHOUT THE EXPRESS PERMISSION OF THE COPYRIGHT HOLDERS.
2. WORK TO PROVIDED DIMENSIONS ONLY.

Key plane

Before

Instructor :

YourSpreadsheets

Address line 1
Address line 2
Telephone line 1
Fax line 1
www.YourSpreadsheets.co.uk

CLIENT: **BAHI CUENT**
3 Mossadah, Ad Doqi, Dokki,
Giza Governorate, Giza,
Egypt


ARCHITECT: **Amr Mamdoh**
40 Mossadah, Ad Doqi, Dokki,
Giza Governorate, Giza,
Egypt

SITE: **31 ROVER ROAD
BLOCK A AND B**

TITLE: **RC DETAILS AND SECTIONS
OF GROUND BEAMS**

SCALE AT A2: 1:50, 1:100	DATE: 05/09/13	DRAWN: DJ	CHECKED: DJ
PROJECT NO: 24567	DRAWING NO: A2/248	REVISION: C	

الحصر الهندسي لحديد Flat Slab باستخدام برنامج ASD حصر شبكة تسليح علوي

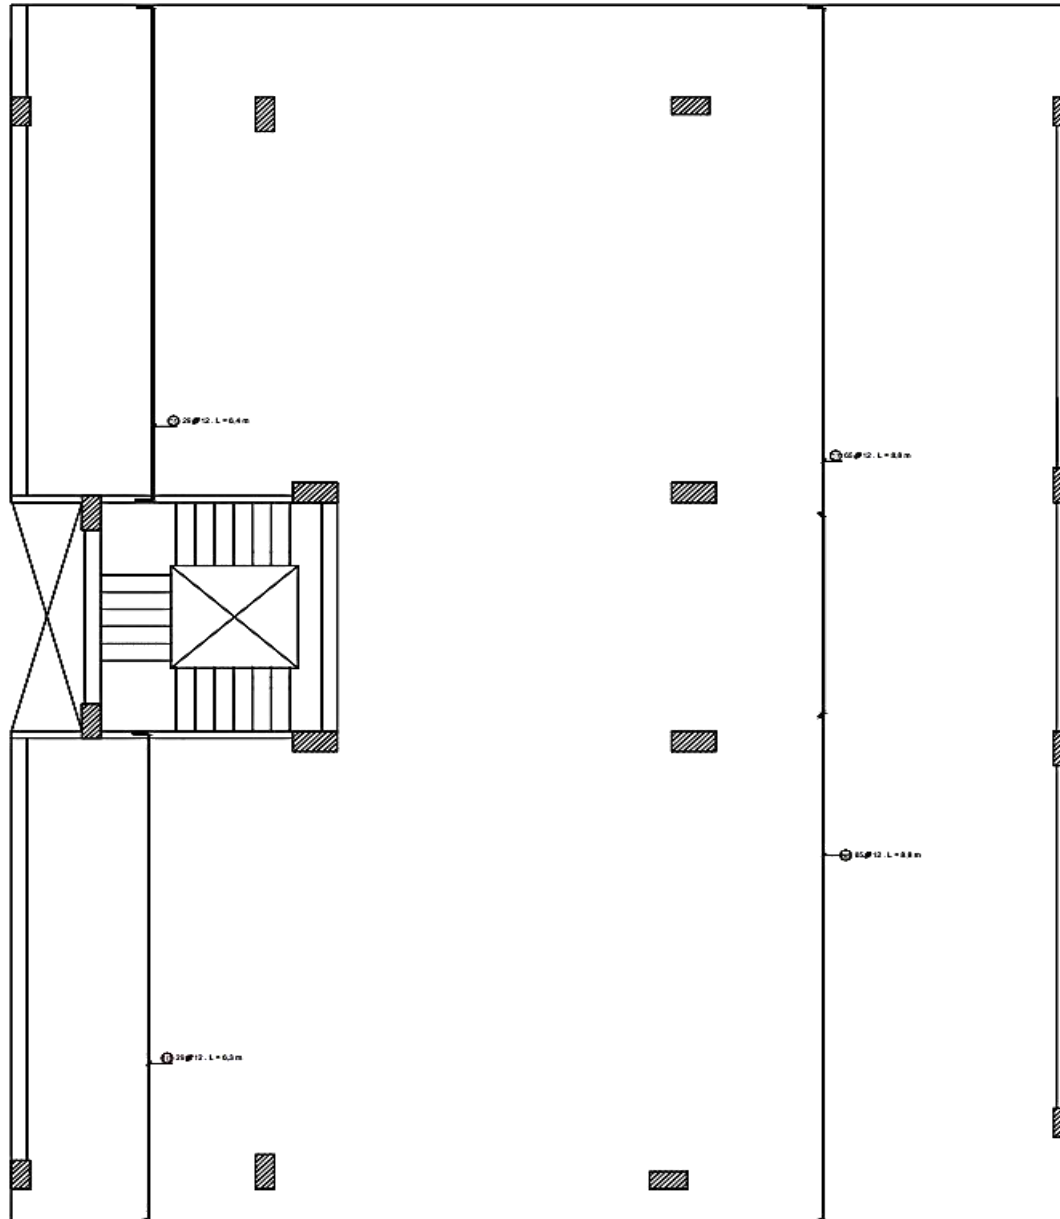

Notes:

1. THE COPYRIGHT OF THIS DRAWING IS VESTED IN YOURSPREADSHEETS AND IT MAY NOT BE REPRODUCED IN WHOLE OR PART OR USED FOR THE MANUFACTURE OF ANY ARTICLE WITHOUT THE EXPRESS PERMISSION OF THE COPYRIGHT HOLDERS.
2. WORK TO PROVIDED DIMENSIONS ONLY.

Key plane

Before

Instructor :

YourSpreadsheets

Address line 1
Address line 2
Telephone line 1
Fax line 1
www.YourSpreadsheets.co.uk

CLIENT: BAH i CUENT
3 Mossadakh, Ad Doqi, Dokki,
Giza Governorate, Giza,
EGYPT

ARCHITECT: Amr Mamdoh
40 Mossadakh, Ad Doqi, Dokki,
Giza Governorate, Giza,
EGYPT

SITE: 31 ROVER ROAD
BLOCK A AND B

TITLE: RC DETAILS AND SECTIONS
OF GROUND BEAMS

SCALE AT A2: 1:50, 1:100	DATE: 05/09/13	DRAWN: DJ	CHECKED: DJ
PROJECT NO: 24567	DRAWING NO: A2/248	REVISION: C	

الحصر الهندسي لحديد Flat Slab باستخدام برنامج ASD
جدول الحصر



Notes:

1. THE COPYRIGHT OF THIS DRAWING IS VESTED IN YOURSPREADSHEETS AND IT MAY NOT BE REPRODUCED IN WHOLE OR PART OR USED FOR THE MANUFACTURE OF ANY ARTICLE WITHOUT THE EXPRESS PERMISSION OF THE COPYRIGHT HOLDERS.
2. WORK TO DIMENSIONS ONLY.

Key plane

Before

Instructor :

YourSpreadsheets

Address line 1
Address line 2
Telephone line 1
Fax line 1
www.YourSpreadsheets.co.uk

CLIENT: **BAHI CUENT**
3 Mossadakh, Ad Doqi, Dokki,
Giza Governorate, Giza,
Egypt

ARCHITECT: **Amr Mamdoh**
40 Mossadakh, Ad Doqi, Dokki,
Giza Governorate, Giza,
Egypt

SITE: **31 ROVER ROAD**
BLOCK A AND B

TITLE: **RC DETAILS AND SECTIONS**
OF GROUND BEAMS

SCALE AT A2: 1:50, 1:100	DATE: 05/09/13	DRAWN: DJ	CHECKED: DJ
PROJECT NO: 24567	DRAWING NO: A2/248	REVISION: C	

B.B.S						
Position	Diameter	Number		Symbol (m)	Length (m)	Total mass (kg)
		in the element	of elements			
01	12	178	1		2.1	331.93
02	16	76	1		2.1	252.17
03	12	48	1		11.8	504.03
04	12	19	1		8.9	150.58
05	12	10	1		8.4	74.59
06	12	49	1		11.8	517.79
07	12	65	1		8.7	509.38
08	12	65	1		8.7	509.38
09	12	29	1		6.0	163.53
10	12	29	1		6.0	161.59

B.B.S		
T	Ø 12	Ø 16
Unit weight (kg/m)	0.89	1.58
Total length (m)	3291.5	159.6
Total weight (kg)	2922.81	252.17

THE END

COURSE: TECHNICAL OFFICE G46

Name: Ibrahim Mohamed Read

Eng: Amr Mamdouh

Lecture: 20

Task: 18

لوحة الحصر الهندسي اللبشة (Raft) باستخدام برنامج ASD



Notes:

1. THE COPYRIGHT OF THIS DRAWING IS VESTED IN YOURSPREADSHEETS AND IT MAY NOT BE REPRODUCED IN WHOLE OR PART OR USED FOR THE MANUFACTURE OF ANY ARTICLE WITHOUT THE EXPRESS PERMISSION OF THE COPYRIGHT HOLDERS.
2. WORK TO PROVIDED DIMENSIONS ONLY.

Key plane

Before

Instructor :

YourSpreadsheets

Address line 1
Address line 2
Telephone line 1
Fax line 1
www.YourSpreadsheets.co.uk


CLIENT: **BAHI CUENT**
3 Mossadakh, Ad Doqi, Dokki,
Giza Governorate, Giza,
EGYPT

ARCHITECT: **Amr Mamdoh**
40 Mossadakh, Ad Doqi, Dokki,
Giza Governorate, Giza,
EGYPT

SITE: **31 ROVER ROAD
BLOCK A AND B**

TITLE: **RC DETAILS AND SECTIONS
OF GROUND BEAMS**

SCALE AT A2: 1:50, 1:100	DATE: 05/09/13	DRAWN: DJ	CHECKED: DJ
PROJECT NO: 24567	DRAWING NO: A2/248	REVISION:	C

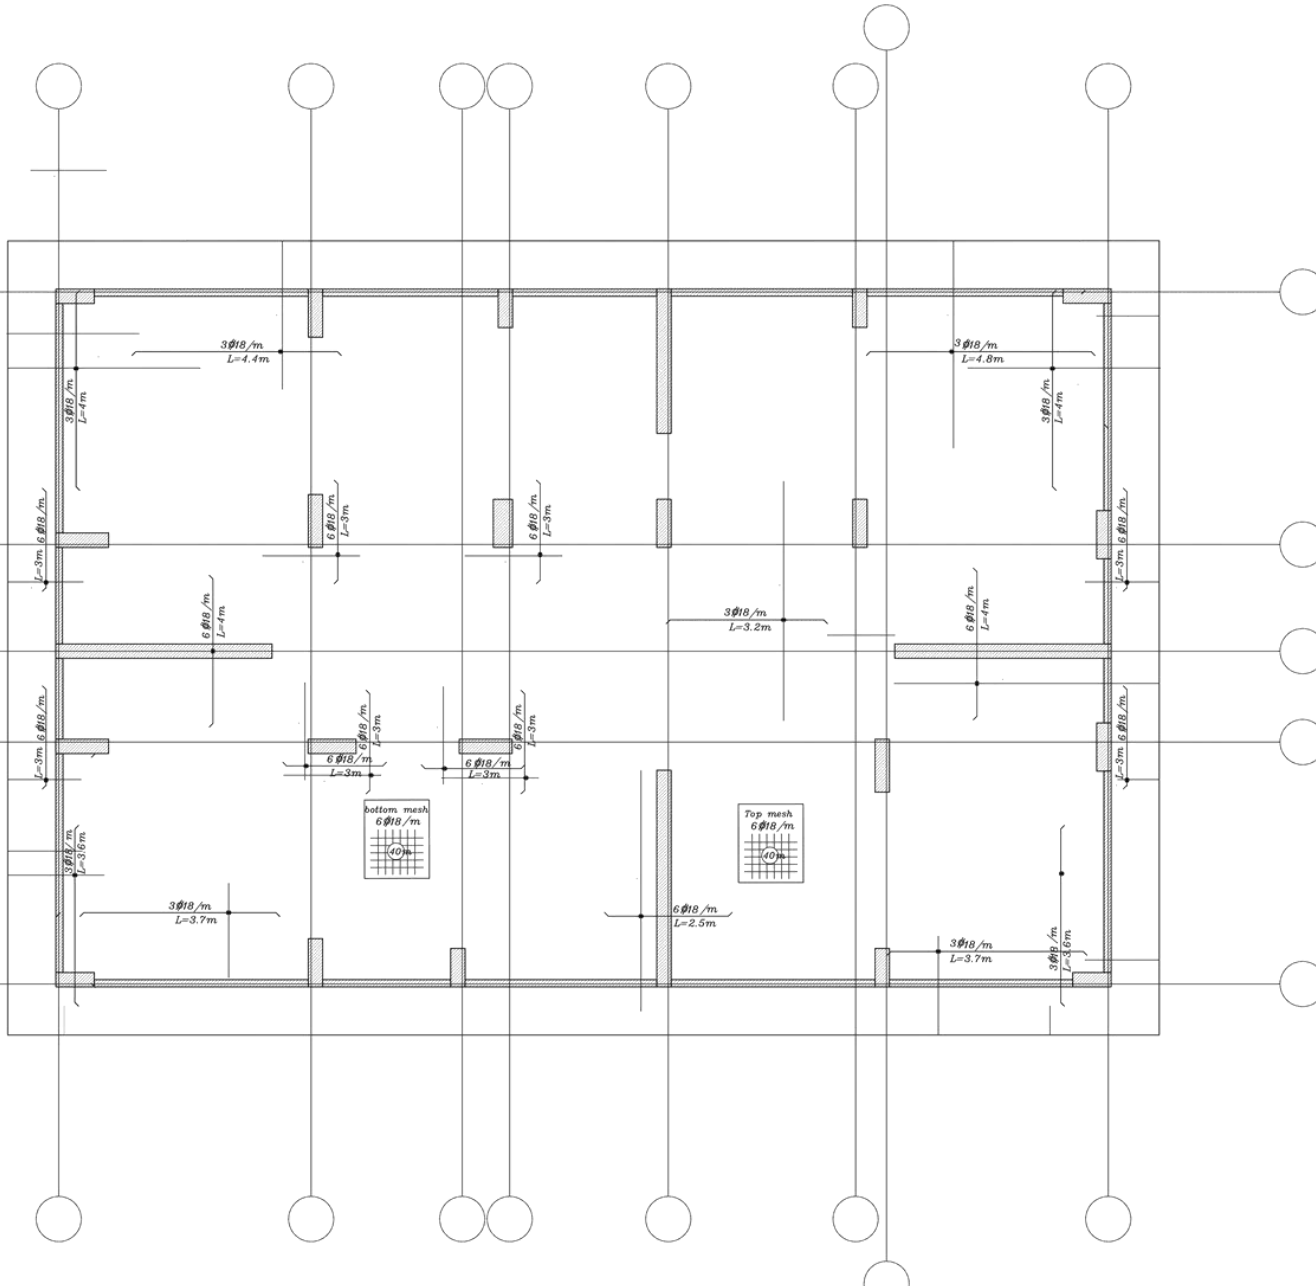

الحصر الهندسي اللبشة (Raft) باستخدام برنامج ASD



Notes:

1. THE COPYRIGHT OF THIS DRAWING IS VESTED IN YOURSPREADSHEETS AND IT MAY NOT BE REPRODUCED IN WHOLE OR PART OR USED FOR THE MANUFACTURE OF ANY ARTICLE WITHOUT THE EXPRESS PERMISSION OF THE COPYRIGHT HOLDERS.
2. WORK TO PROVIDED DIMENSIONS ONLY.

Key plane

Before

Instructor :

YourSpreadsheets

Address line 1
Address line 2
Telephone line 1
Fax line 1
www.YourSpreadsheets.co.uk


CLIENT: **BAHI CUENT**
3 Mossadakh, Ad Doqi, Dokki,
Giza Governorate, Giza,
EGYPT

ARCHITECT: **Amr Mamdoh**
40 Mossadakh, Ad Doqi, Dokki,
Giza Governorate, Giza,
EGYPT

SITE: **31 ROVER ROAD**
BLOCK A AND B

TITLE: **RC DETAILS AND SECTIONS**
OF GROUND BEAMS

SCALE AT A2: 1:50, 1:100	DATE: 05/09/13	DRAWN: DJ	CHECKED: DJ
PROJECT NO: 24567	DRAWING NO: A2/248	REVISION: C	

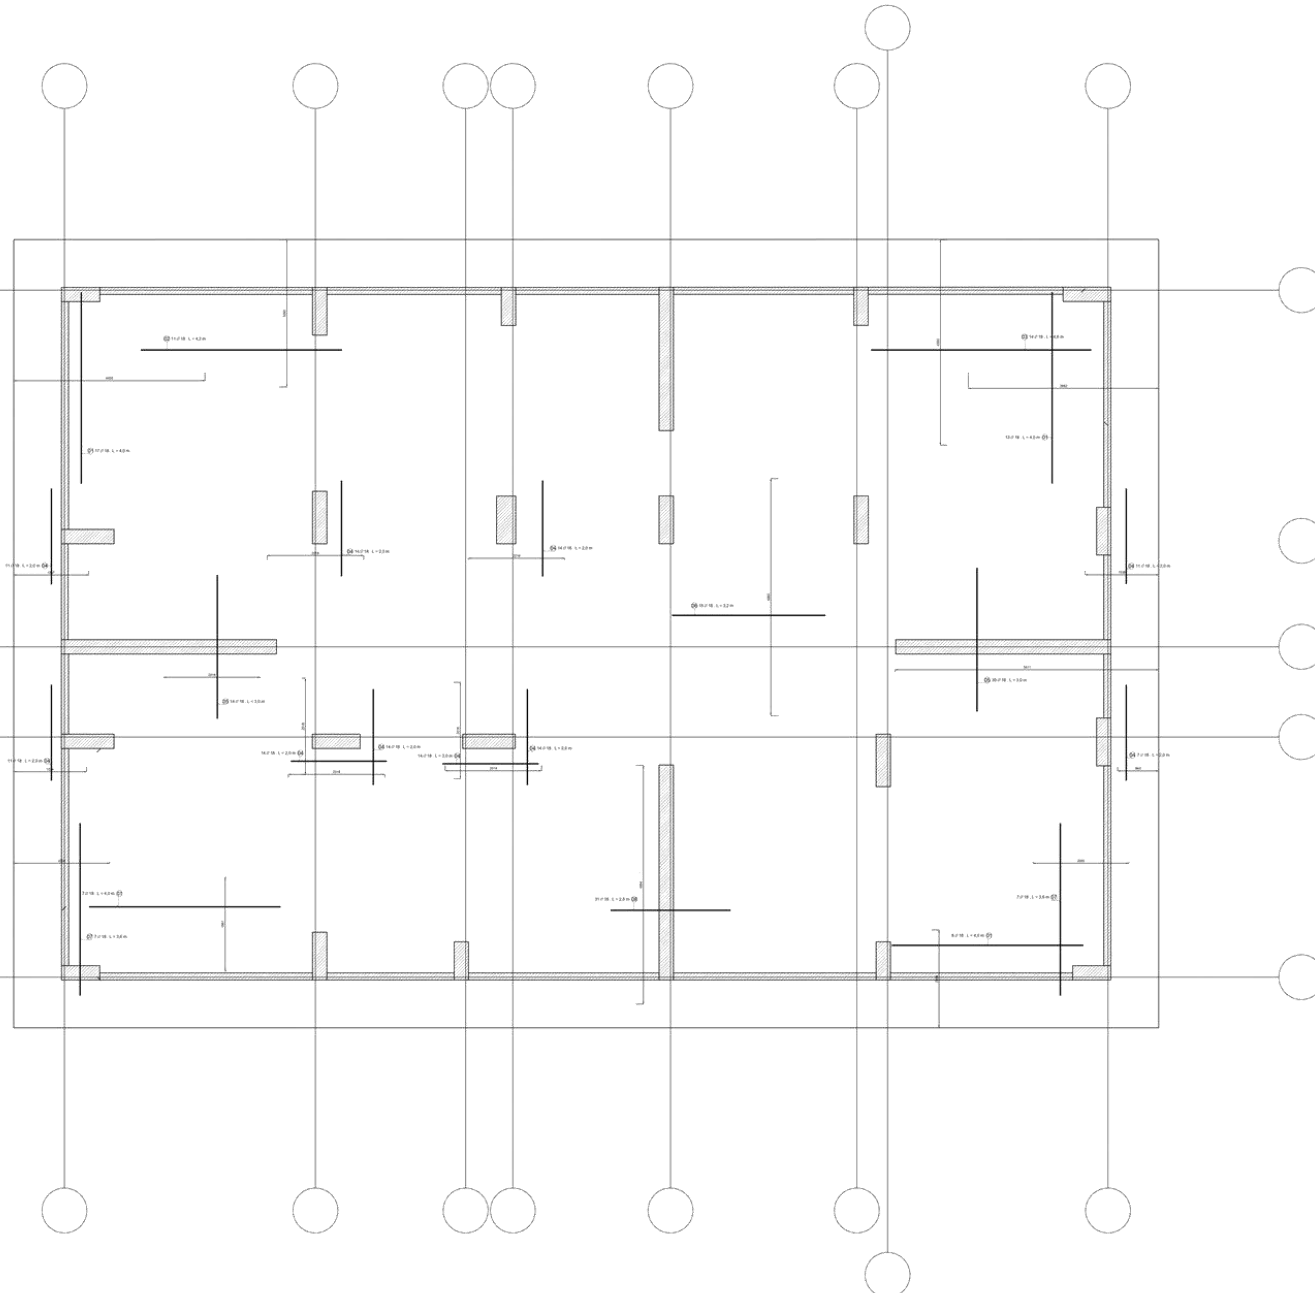

الحصر الهندسي اللبشة (Raft) باستخدام برنامج ASD




Notes:

1. THE COPYRIGHT OF THIS DRAWING IS VESTED IN YOURSPREADSHEETS AND IT MAY NOT BE REPRODUCED IN WHOLE OR PART OR USED FOR THE MANUFACTURE OF ANY ARTICLE WITHOUT THE EXPRESS PERMISSION OF THE COPYRIGHT HOLDERS.
2. WORK TO DIMENSIONED DIMENSIONS ONLY.

Key plane

Before

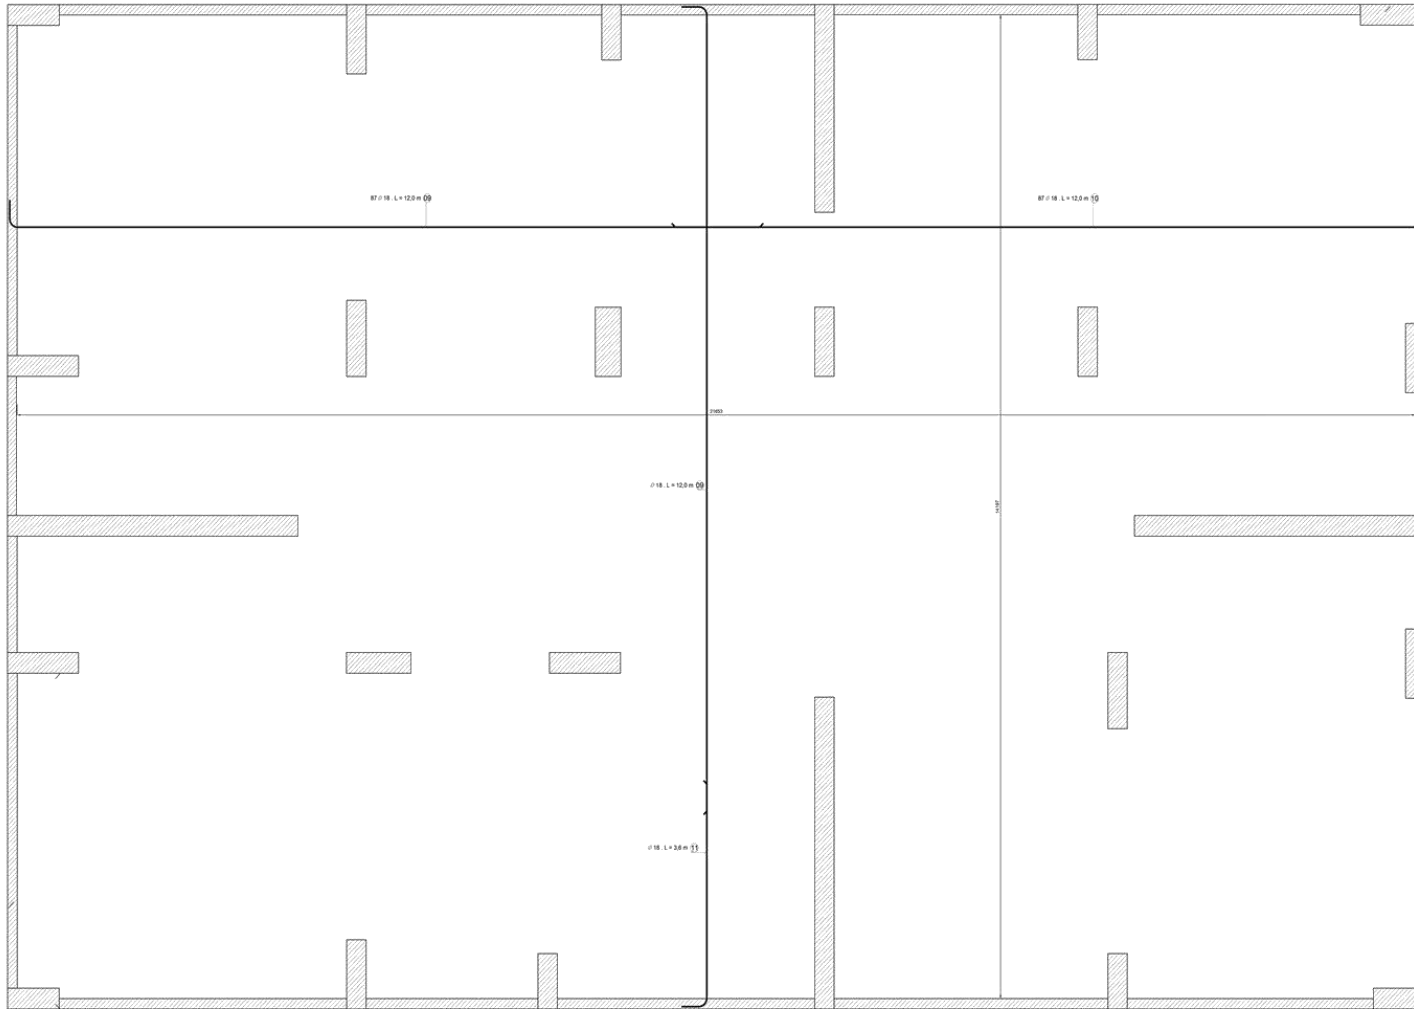

Instructor :

YourSpreadsheets

Address line 1
Address line 2
Telephone line 1
Fax line 1
www.YourSpreadsheets.co.uk

CLIENT: **BAHI CUENT**
3 Mossadak, Ad Doqi, Dokki,
Giza Governorate, Giza,
EGYPT

ARCHITECT: **Amr Mamdoh**
40 Mossadak, Ad Doqi, Dokki,
Giza Governorate, Giza,
EGYPT

SITE: **31 ROVER ROAD
BLOCK A AND B**

TITLE: **RC DETAILS AND SECTIONS
OF GROUND BEAMS**

SCALE AT A2: 1:50, 1:100	DATE: 05/09/13	DRAWN: DJ	CHECKED: DJ
PROJECT NO: 24567	DRAWING NO: A2/248	REVISION: C	

الحصر الهندسي للبشة (Raft) باستخدام برنامج ASD



Notes:

1. THE COPYRIGHT OF THIS DRAWING IS VESTED IN YOURSPREADSHEETS AND IT MAY NOT BE REPRODUCED IN WHOLE OR PART OR USED FOR THE MANUFACTURE OF ANY ARTICLE WITHOUT THE EXPRESS PERMISSION OF THE COPYRIGHT HOLDERS.
2. WORK TO DIMENSIONED DIMENSIONS ONLY.

Key plane

Before

Instructor :

YourSpreadsheets

Address line 1
Address line 2
Telephone line 1
Fax line 1
www.YourSpreadsheets.co.uk


CLIENT: **BAHI CUENT**
3 Mossadak, Ad Doqi, Dokki,
Giza Governorate, Giza,
EGYPT

ARCHITECT: **Amr Mamdoh**
40 Mossadak, Ad Doqi, Dokki,
Giza Governorate, Giza,
EGYPT

SITE: **31 ROVER ROAD
BLOCK A AND B**

TITLE: **RC DETAILS AND SECTIONS
OF GROUND BEAMS**

SCALE AT A2: 1:50, 1:100	DATE: 05/09/13	DRAWN: DJ	CHECKED: DJ
PROJECT NO: 24567	DRAWING NO: A2/248	REVISION: C	

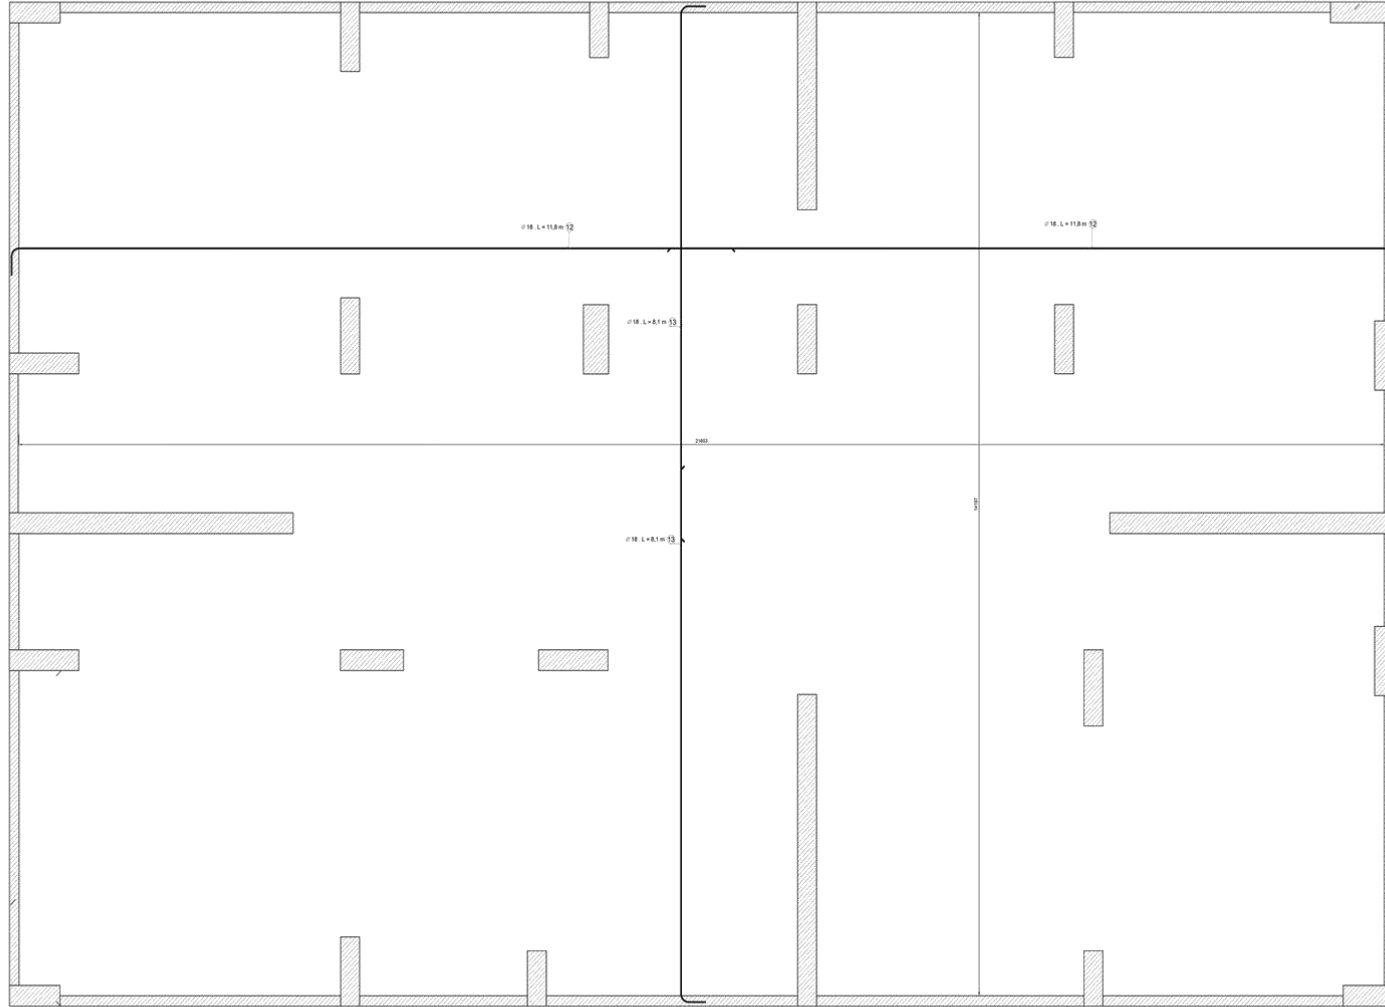

الحصر الهندسي لللبشة (Raft) باستخدام برنامج ASD



Notes:

1. THE COPYRIGHT OF THIS DRAWING IS VESTED IN YOURSPREADSHEETS AND IT MAY NOT BE REPRODUCED IN WHOLE OR PART OR USED FOR THE MANUFACTURE OF ANY ARTICLE WITHOUT THE EXPRESS PERMISSION OF THE COPYRIGHT HOLDERS.
2. WORK TO DIMENSIONS ONLY.

Key plane

Before

Instructor :

YourSpreadsheets

Address line 1
Address line 2
Telephone line 1
Fax line 1
www.YourSpreadsheets.co.uk

CLIENT: BAH i CUENT
3 Mossadakh, Ad Doqi, Dokki,
Giza Governorate, Giza,
Egypt

ARCHITECT: Amr Mamdoh
40 Mossadakh, Ad Doqi, Dokki,
Giza Governorate, Giza,
Egypt

SITE: 31 ROVER ROAD
BLOCK A AND B

TITLE: RC DETAILS AND SECTIONS
OF GROUND BEAMS

SCALE AT A2: 1:50, 1:100	DATE: 05/09/13	DRAWN: DJ	CHECKED: DJ
PROJECT NO: 24567	DRAWING NO: A2/248	REVISION: C	

B.B.S

Position	Diameter	Number		Symbol (m)	Length (m)	Total mass (kg)
		In the element	of elements			
01	18	45	1	4.0	4.0	360.00
02	18	11	1	4.2	4.2	92.40
03	18	14	1	4.6	4.6	128.80
04	18	124	1	2.0	2.0	496.00
05	18	49	1	3.0	3.0	294.00
06	18	15	1	3.2	3.2	96.00
07	18	14	1	3.6	3.6	100.80
08	18	31	1	2.5	2.5	155.00
09	18	88	1	400.0 11.7	12.4	2182.40
10	18	87	1	11.5 400.0	12.4	2148.90
11	18	1	1	3.3 400.0	4.0	8.00
12	18	2	1	400.0 11.5	12.2	48.90
13	18	2	1	400.0 7.7	8.5	33.90

B.B.S

T	Ø 18
Unit weight (kg/m)	2.00
Total length (m)	3000.6
Total weight (kg)	6001.10

THE END